




Dit plan is een bijlage bij het advies van de dienst wonen dat werd uitgebracht in functie van de woonkwaliteit binnen deze aanvraag tot omgevingsvergunning.

Het betreft dus geen vergund plan.

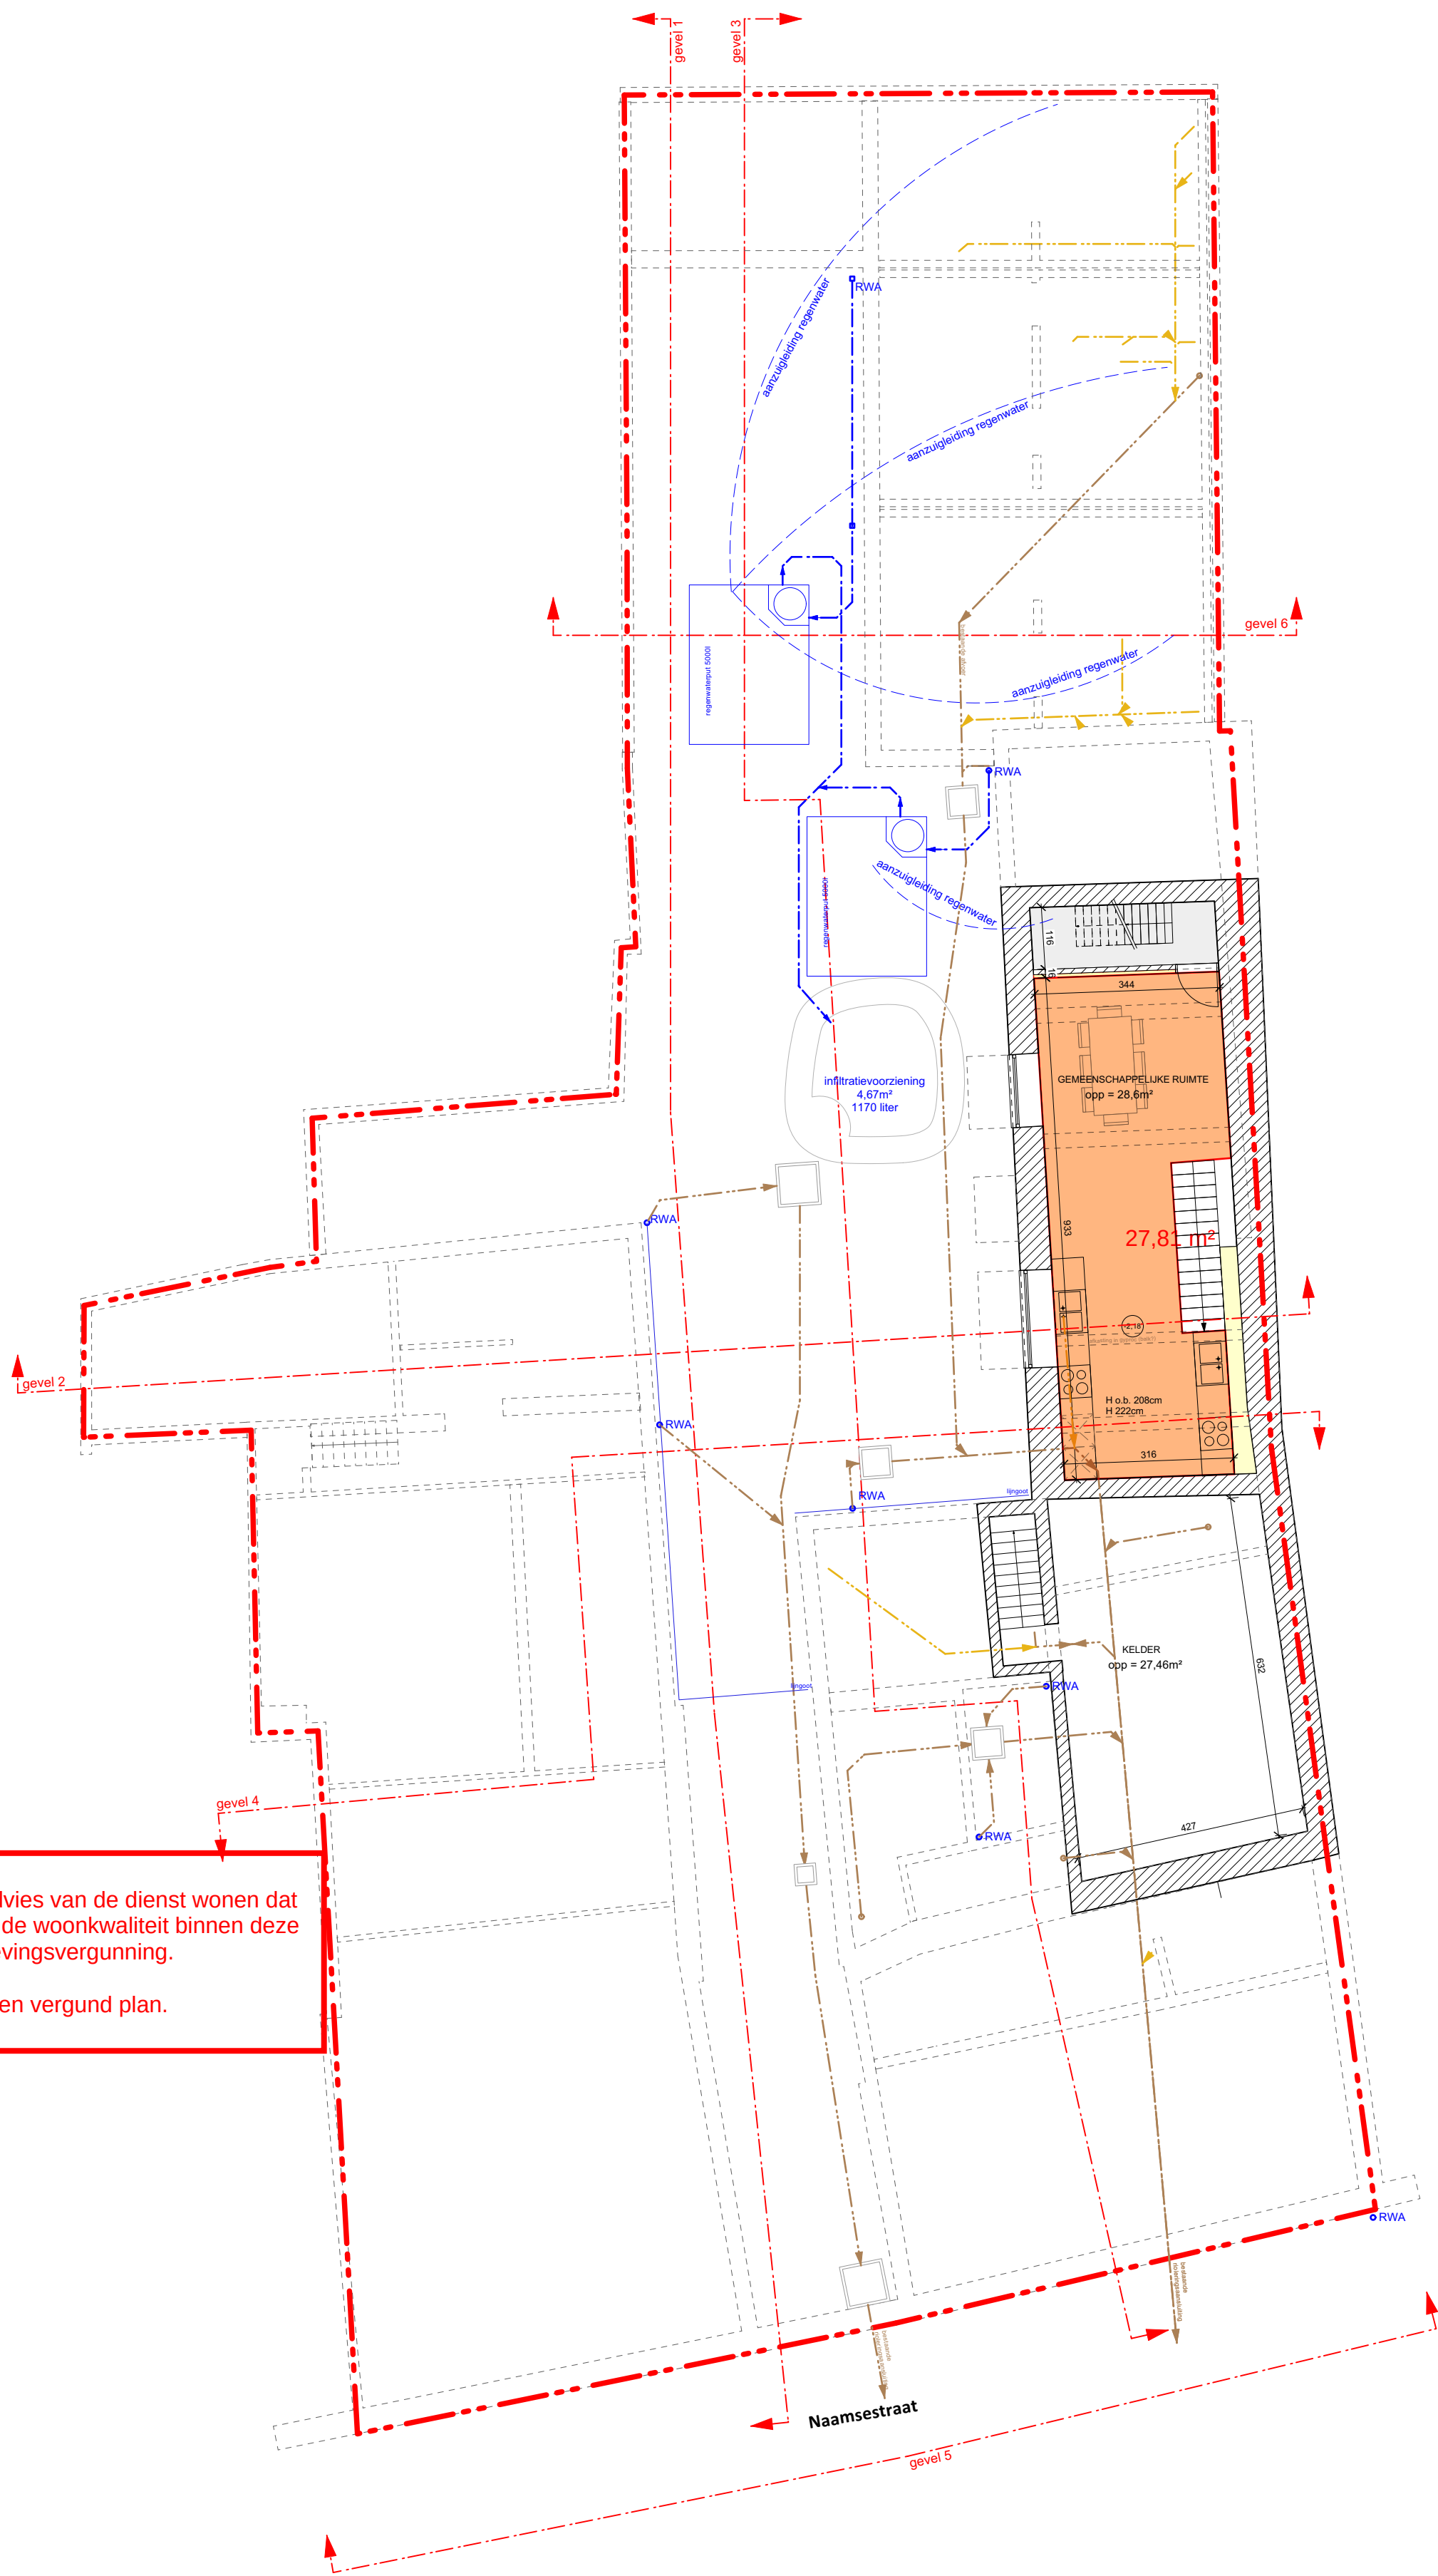


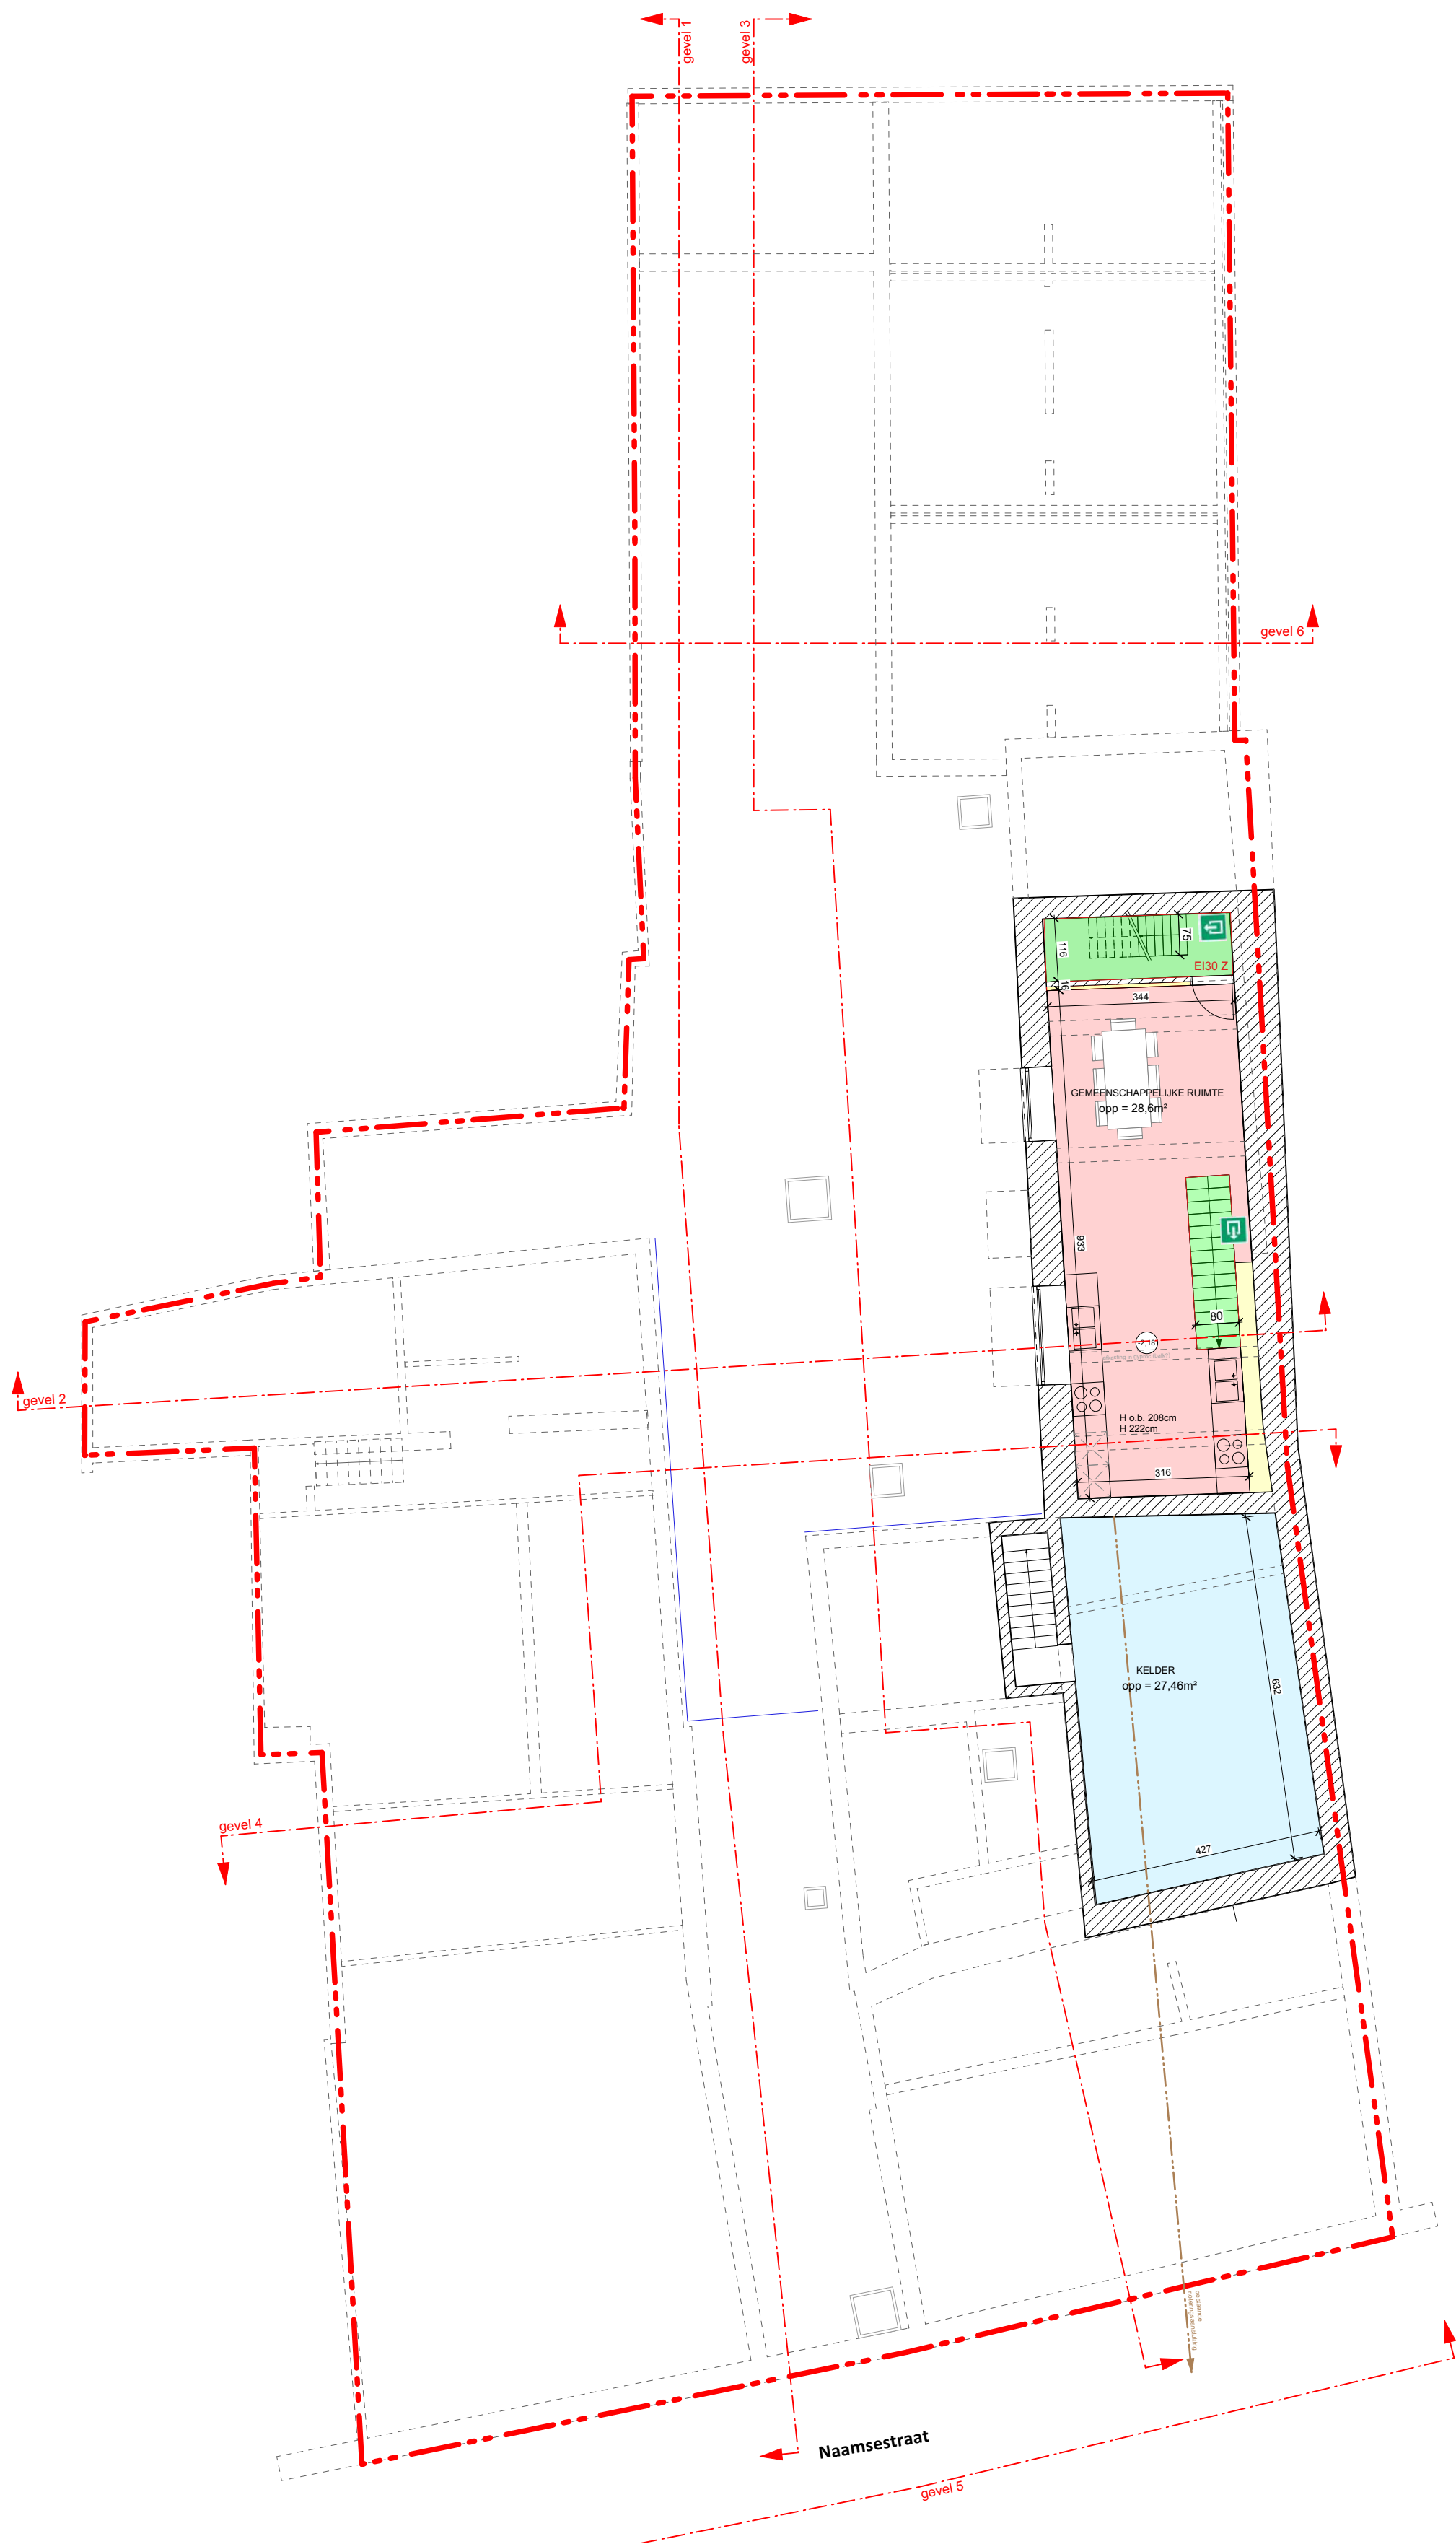


Elektronisch ondertekend document, blz. 3 van 54. Verifieerbaar via code.esignflow.be met code 3318-2678-4008-3316

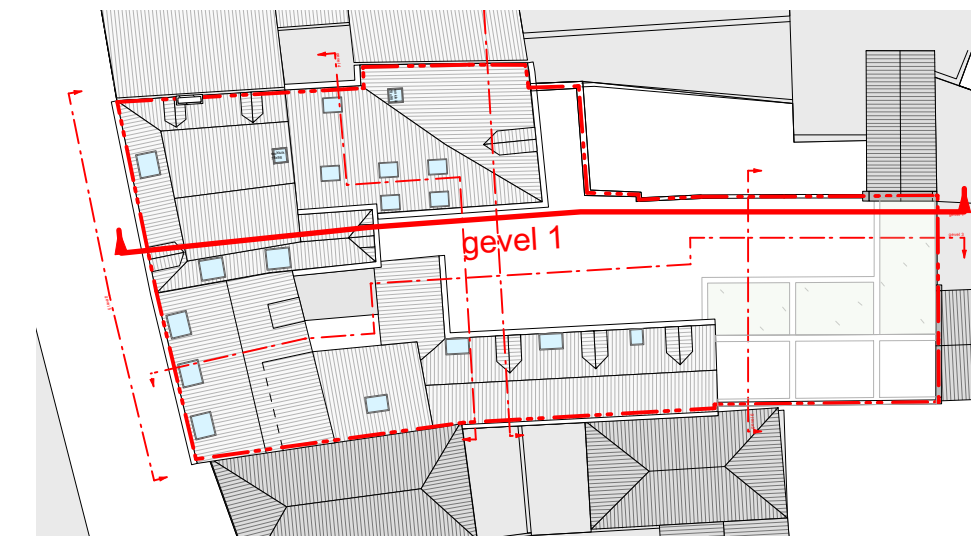

Het betreft dus geen vergund plan.

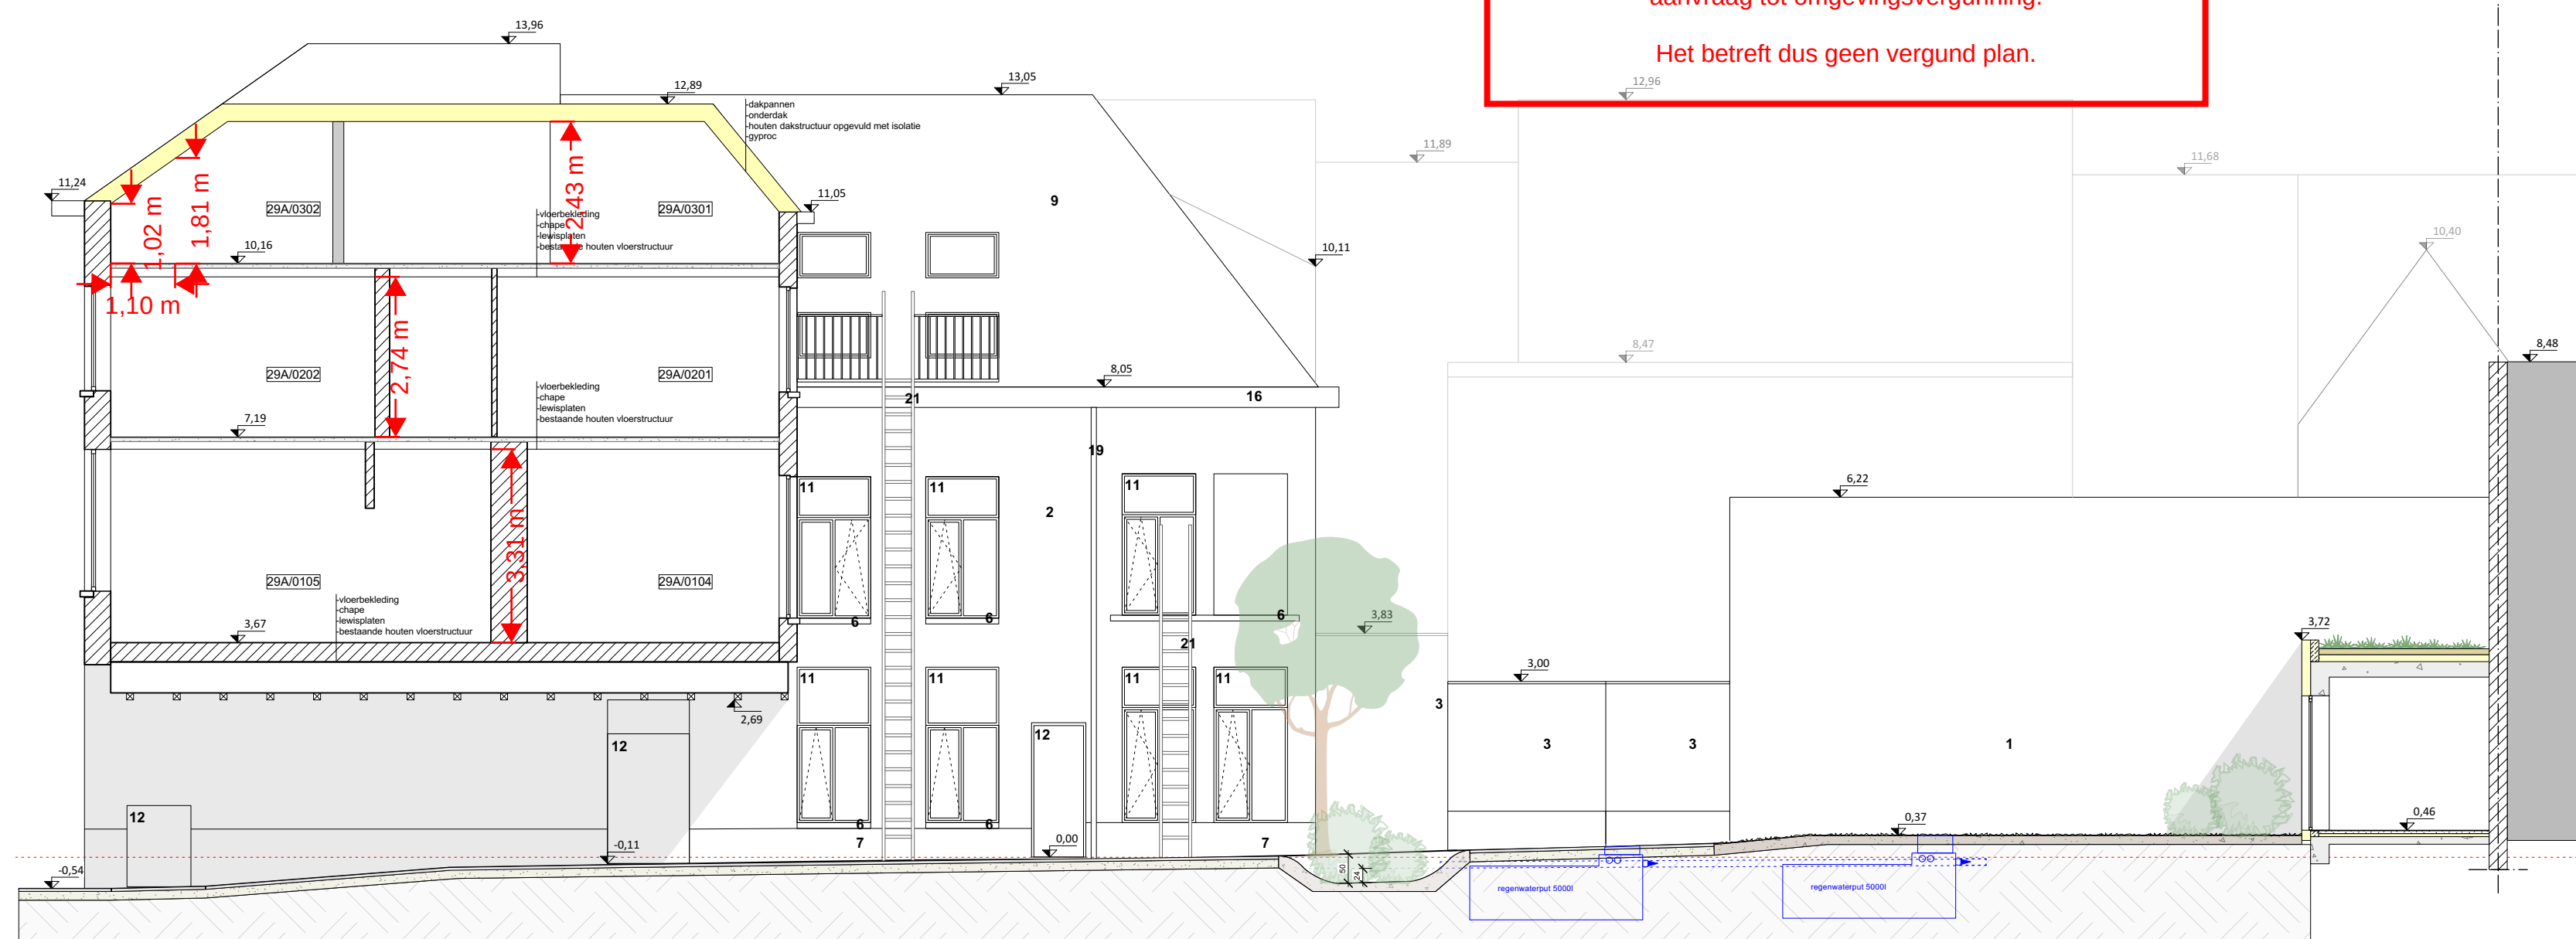

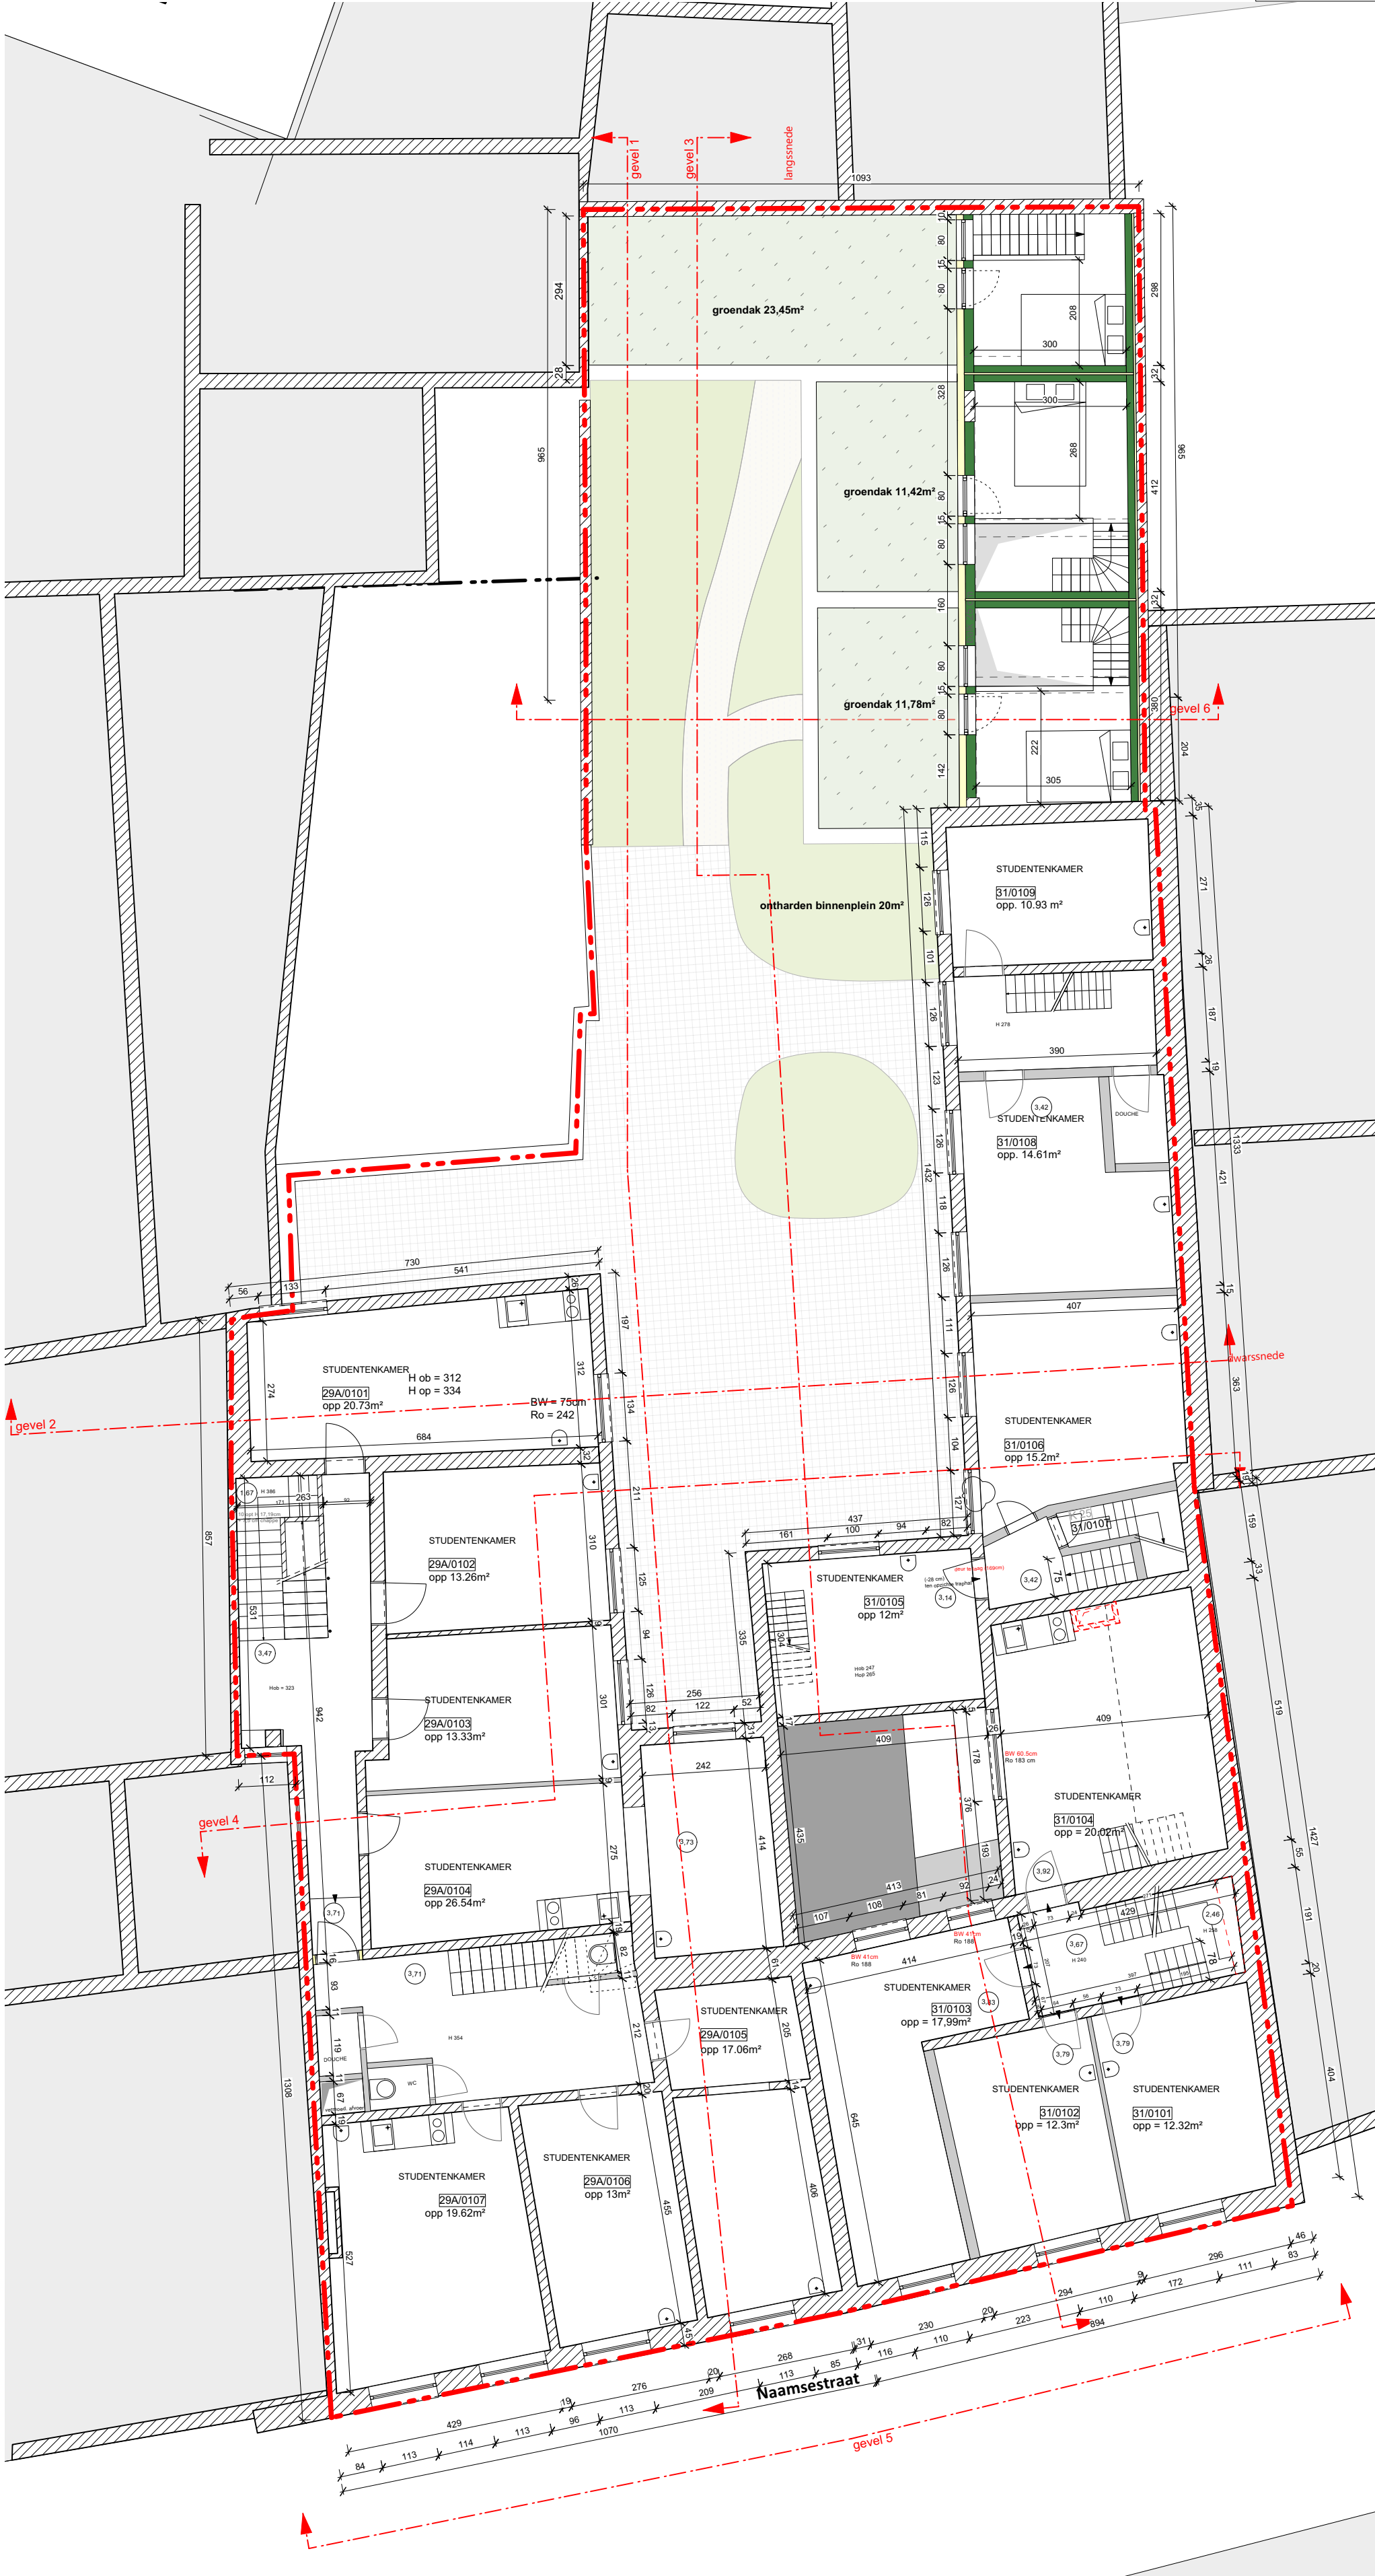





Dit plan is een bijlage bij het advies van de dienst wonen dat werd uitgebracht in functie van de woonkwaliteit binnen deze aanvraag tot omgevingsvergunning.

Het betreft dus geen vergund plan.

0 1 10x
1:200
26/01/2024
VO_NAAMSE 29-31_I_N_01 1/1

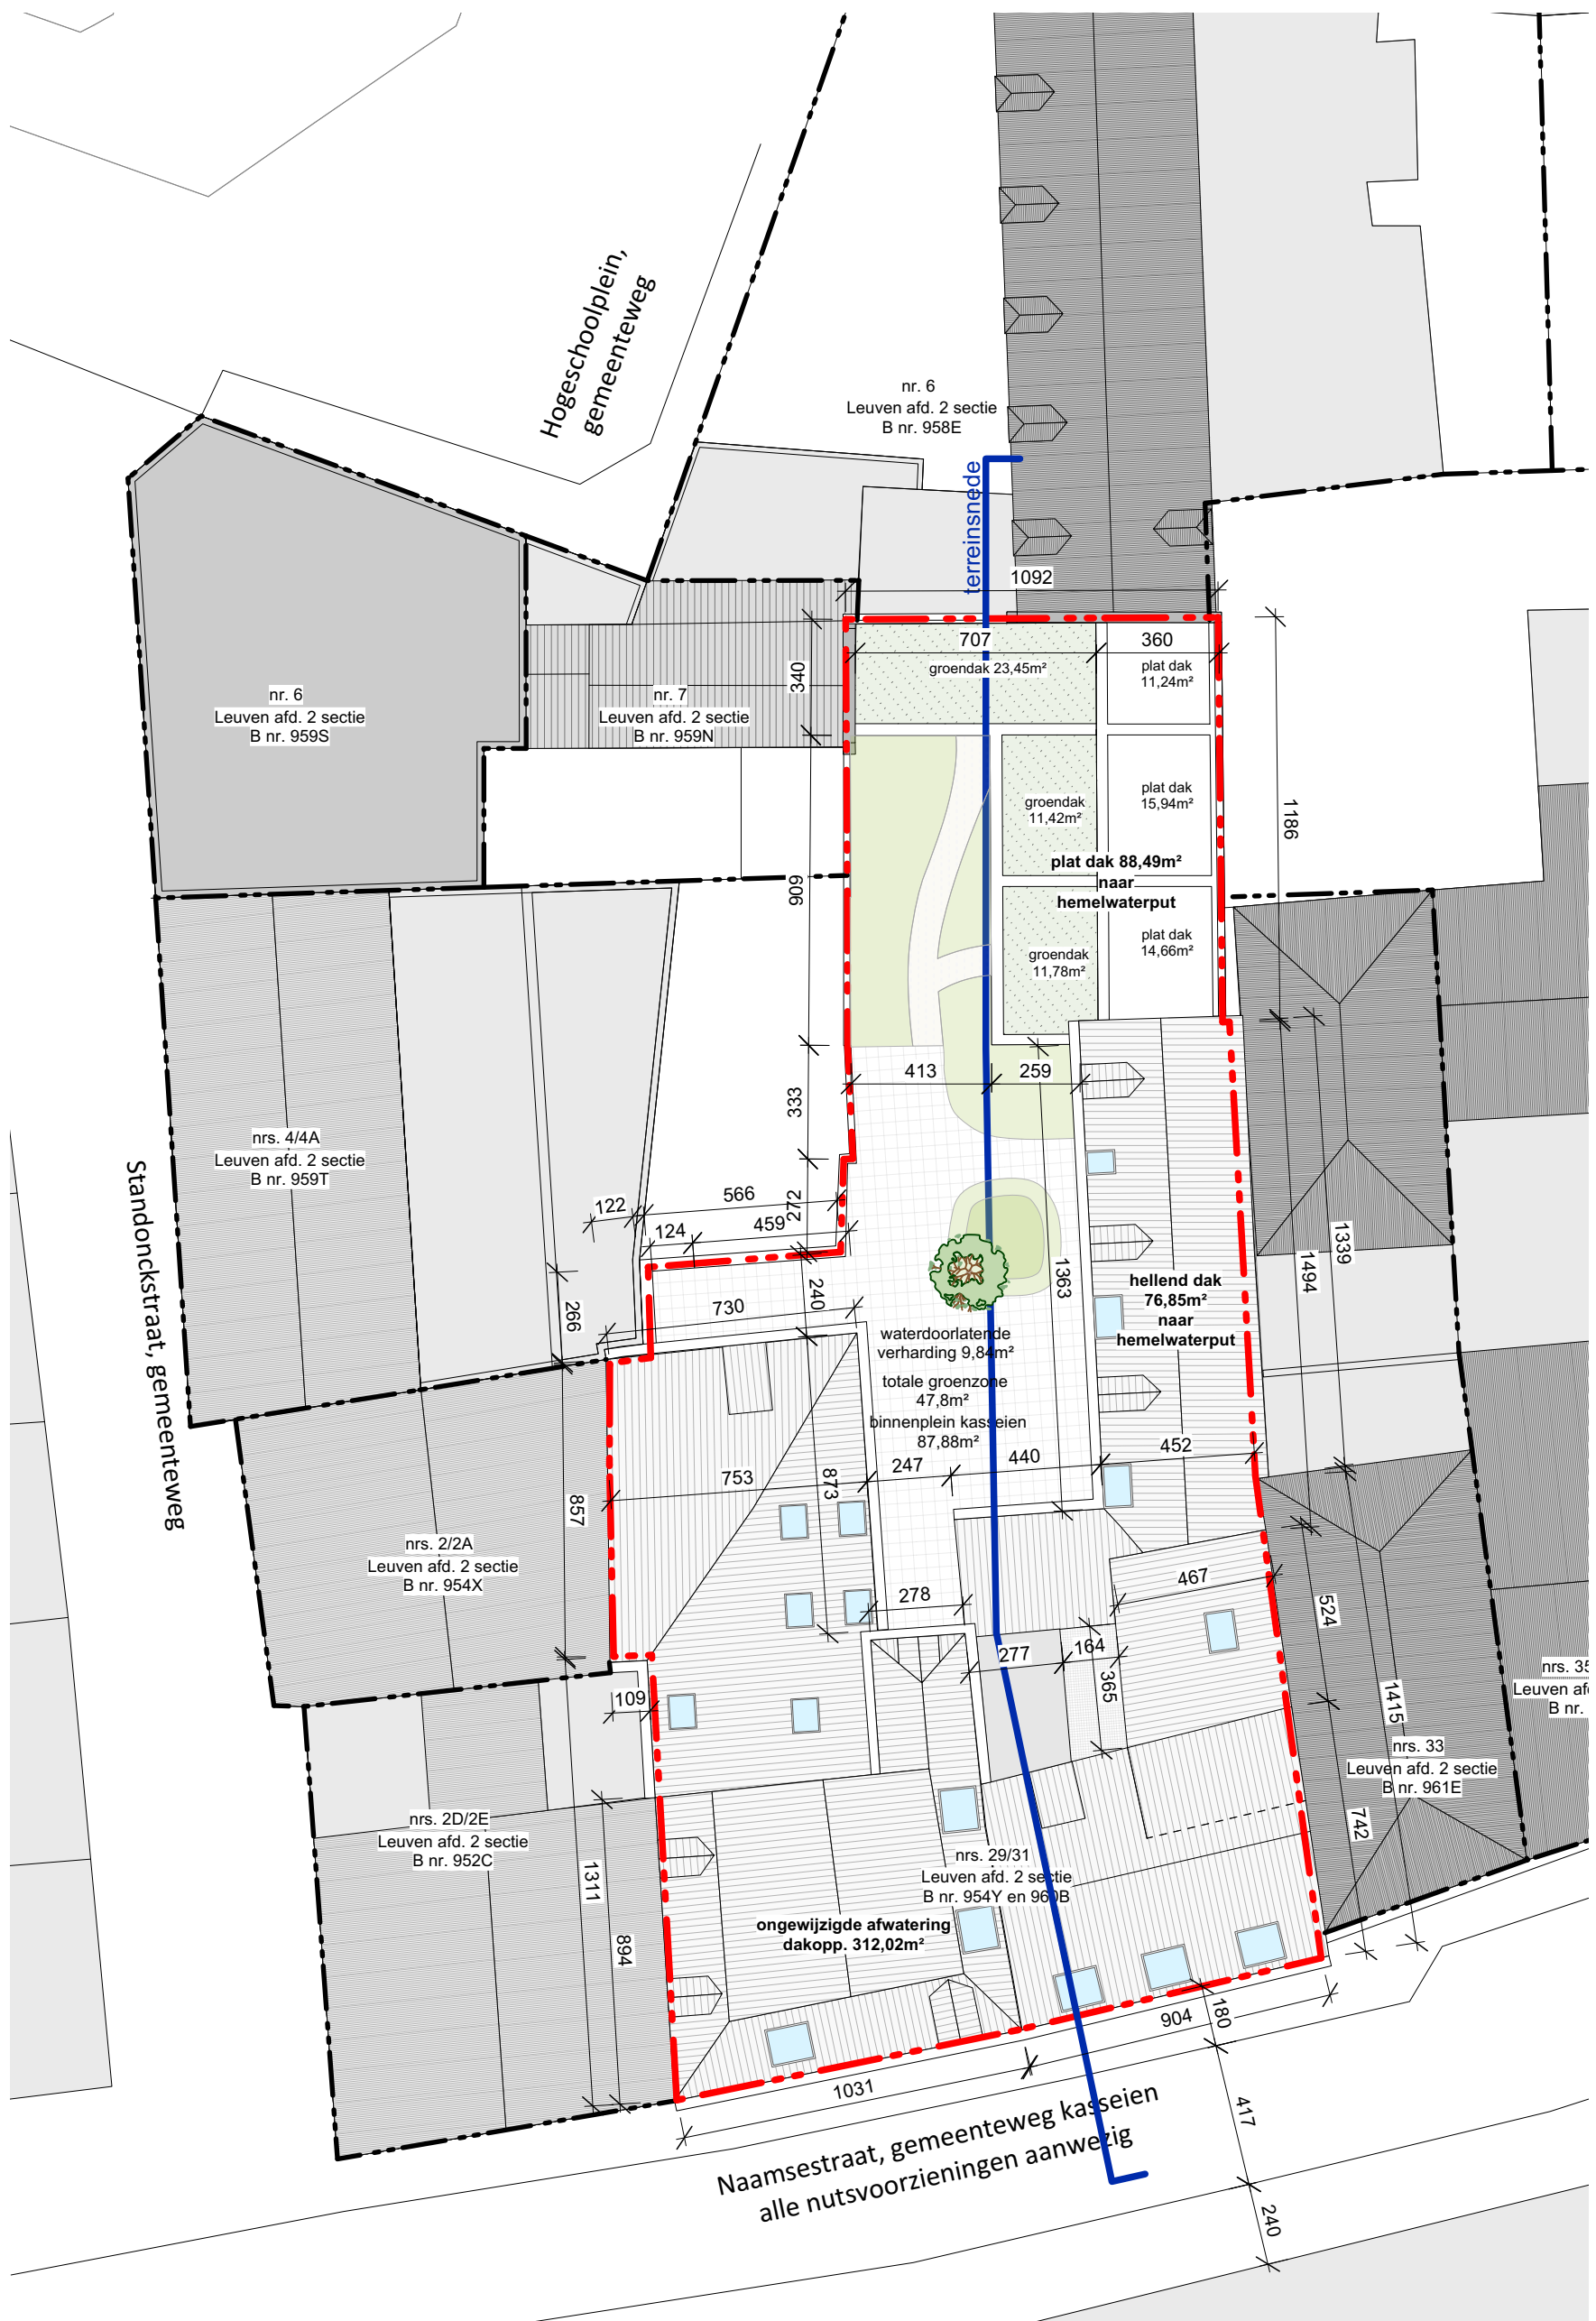

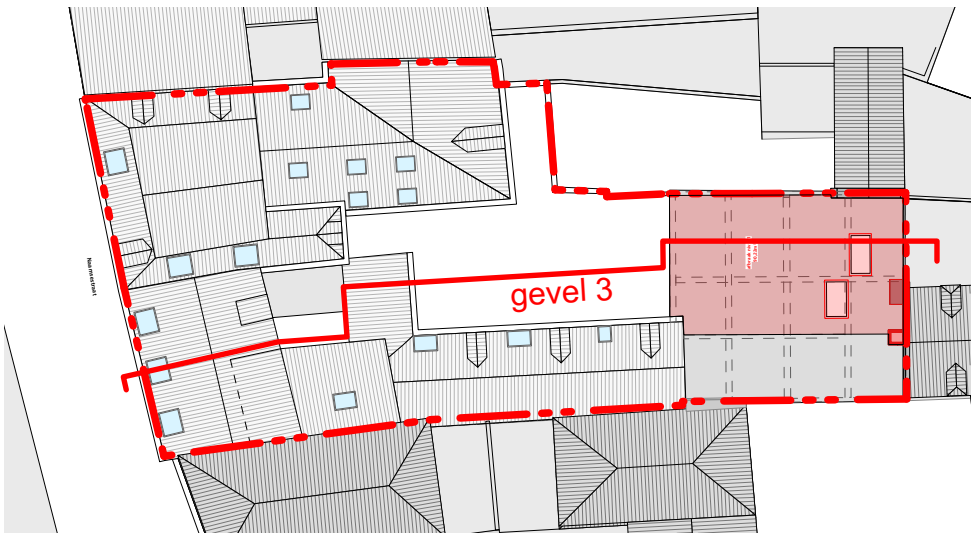

T'JONCK / NILIS

INGENIEUR-ARCHITECTEN

Erasmus Ruelensvest 83/002

3001 Heverlee

T: +32 16 23 45 48

NAAMSESTRAAT 29

ZIJGEVEL - GEVEL 3

bestaande toestand

01000

26/01/2024

BA_NAAMSE 29-31_G_8_02

01000


26/01/2024


BA_NAAMSE 29-31_G_8_02

01000

26/01/2024

BA_NAAMSE 29-31_G_8_02

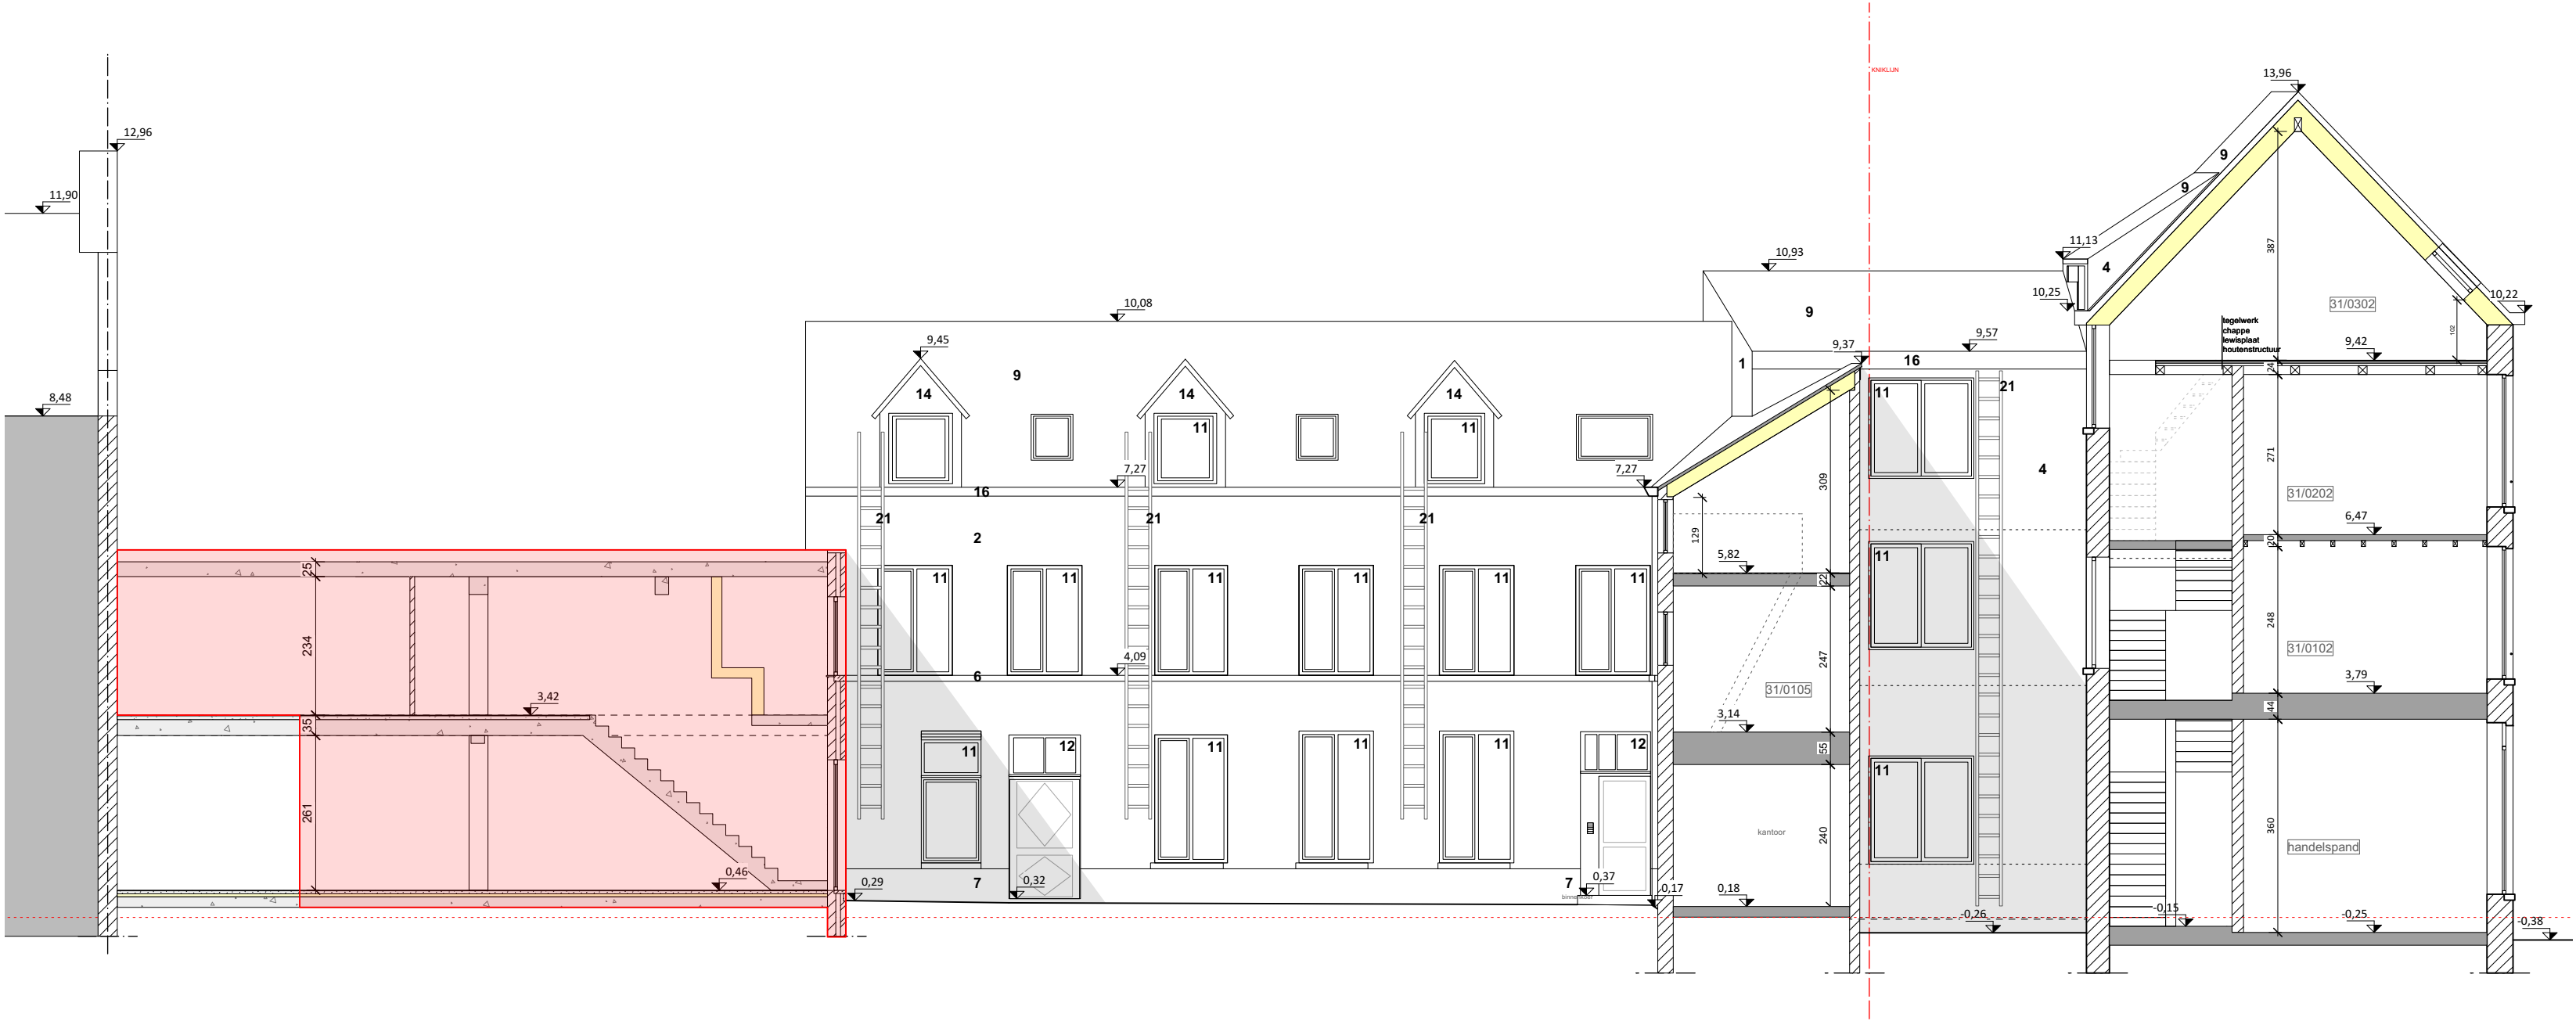

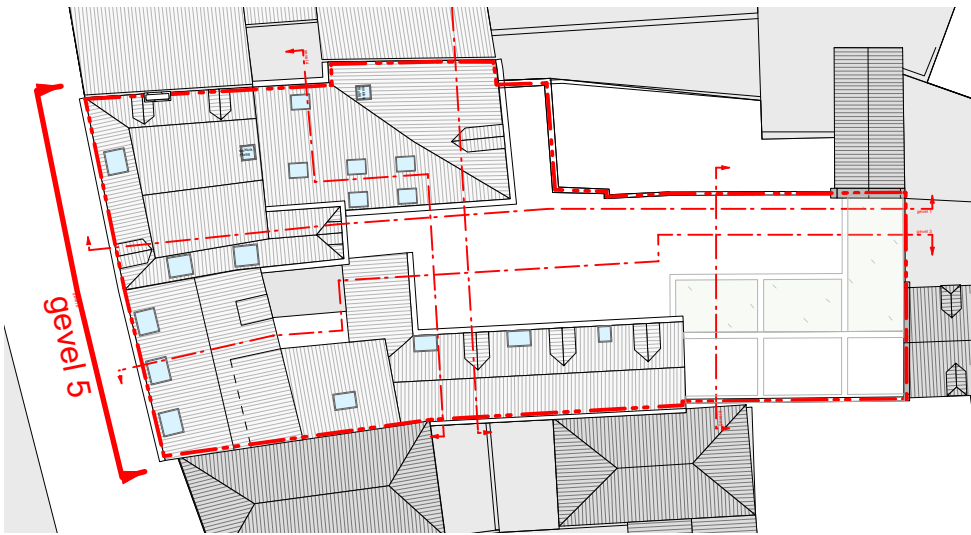

T'JONCK / NILIS

INGENIEUR-ARCHITECTEN

Erasmus Ruelensvest 83/002

3001 Heverlee

T: +32 16 23 45 48

NAAMSESTRAAT 29

VOORGEVEL - GEVEL 5

nieuwe toestand - ongewijzigd

015

1:100

26/01/2024


BA_NAAMSE 29-31_G_N_04



NAAMSESTRAAT 29
GRONDPLAN GELIJKVLOERS
bestaande toestand

0 2 5
1:100
26/01/2024
BA_NAAMSE 29-31_P_8_02



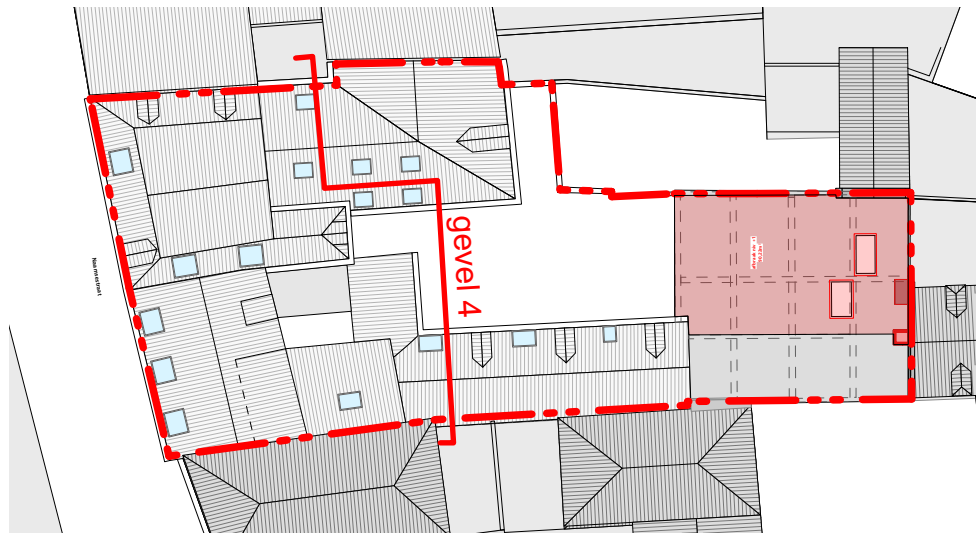


NAAMSESTRAAT 29
ACHTERGEVEL - GEVEL 4
bestaande toestand

0 1 5

1:100

26/01/2024


BA_NAAMSE 29-31_G_8_03

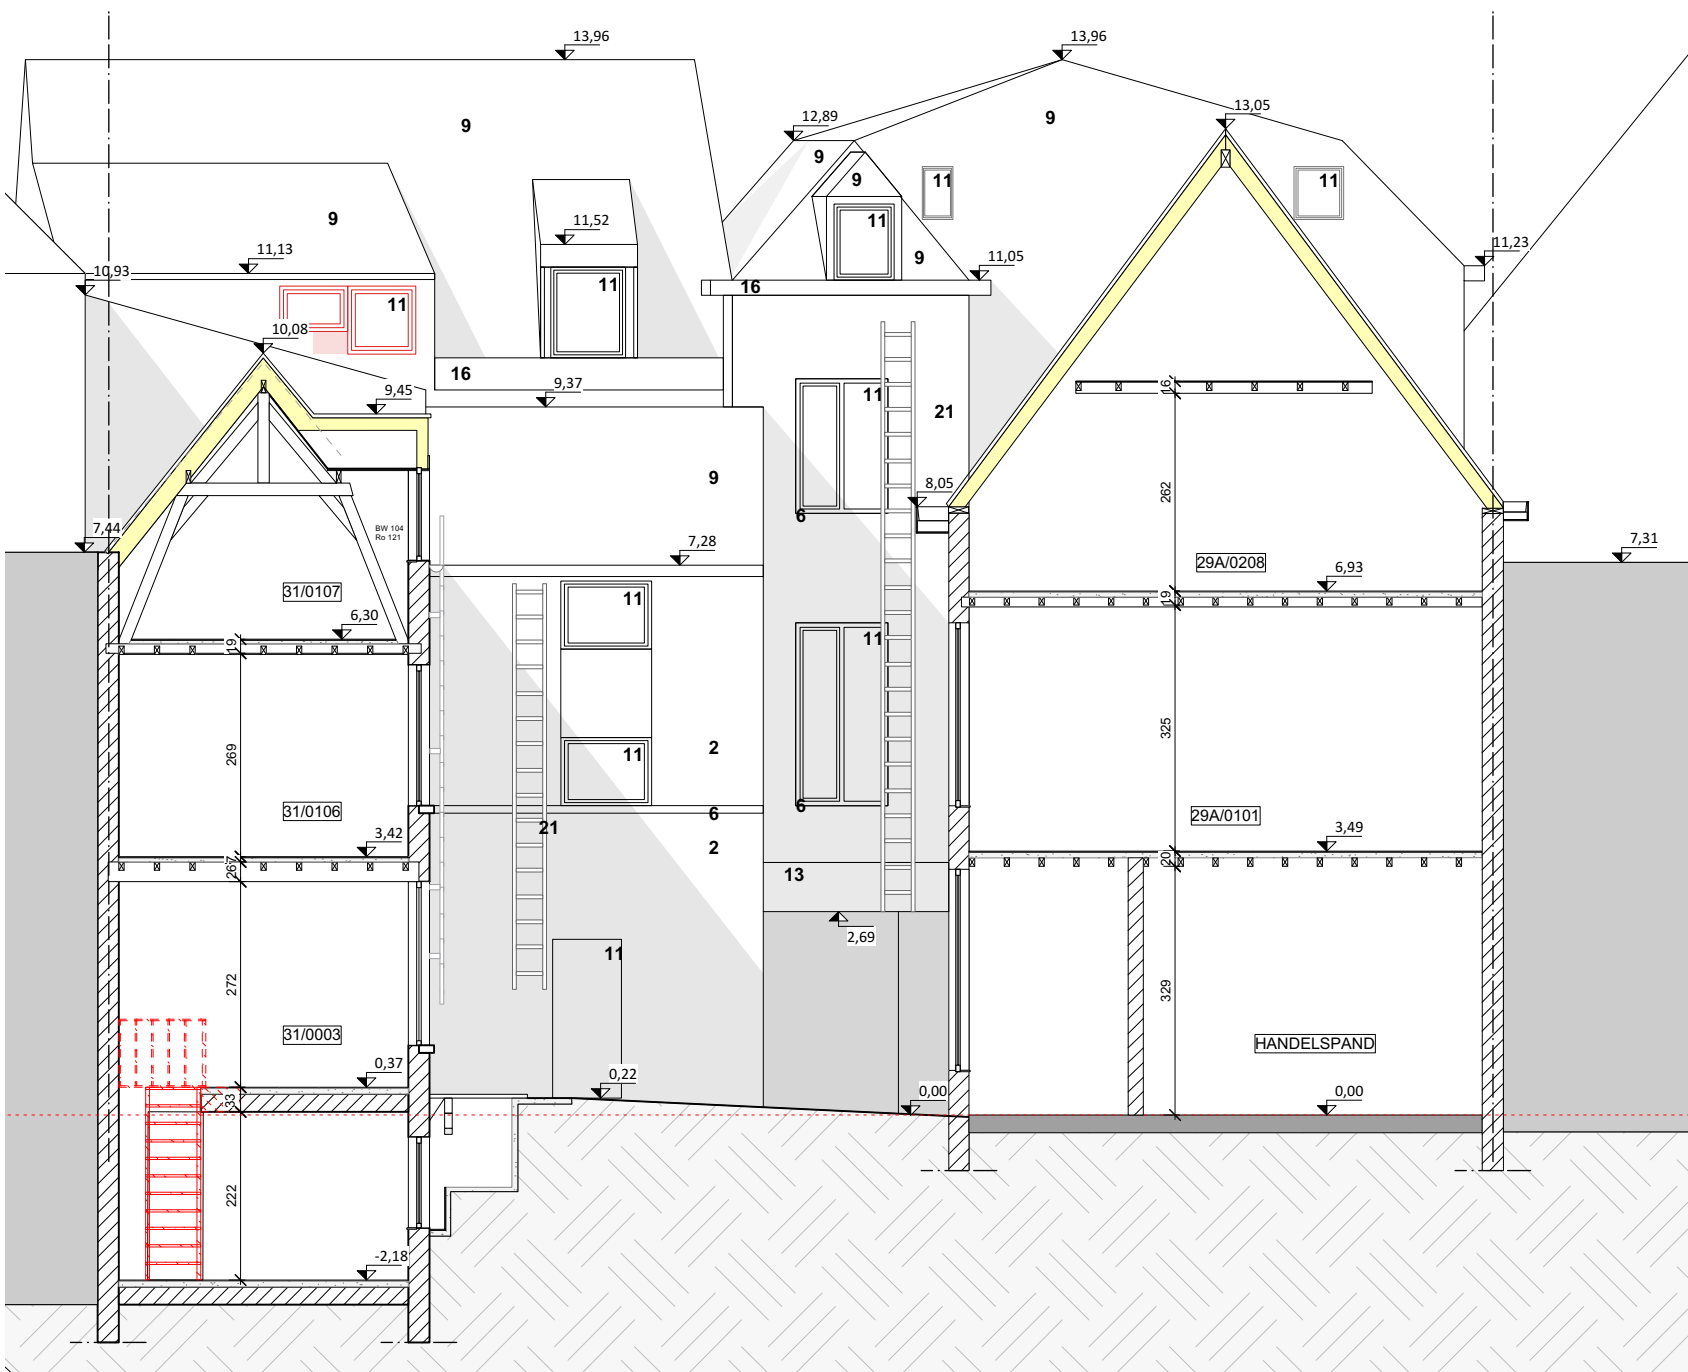



NAAMSESTRAAT 29
GRONDPLAN NIVO +1 - brandweer
nieuwe toestand

0 1 5
1:100

26/01/2024
BA_NAAMSE 29-31_P_N_03

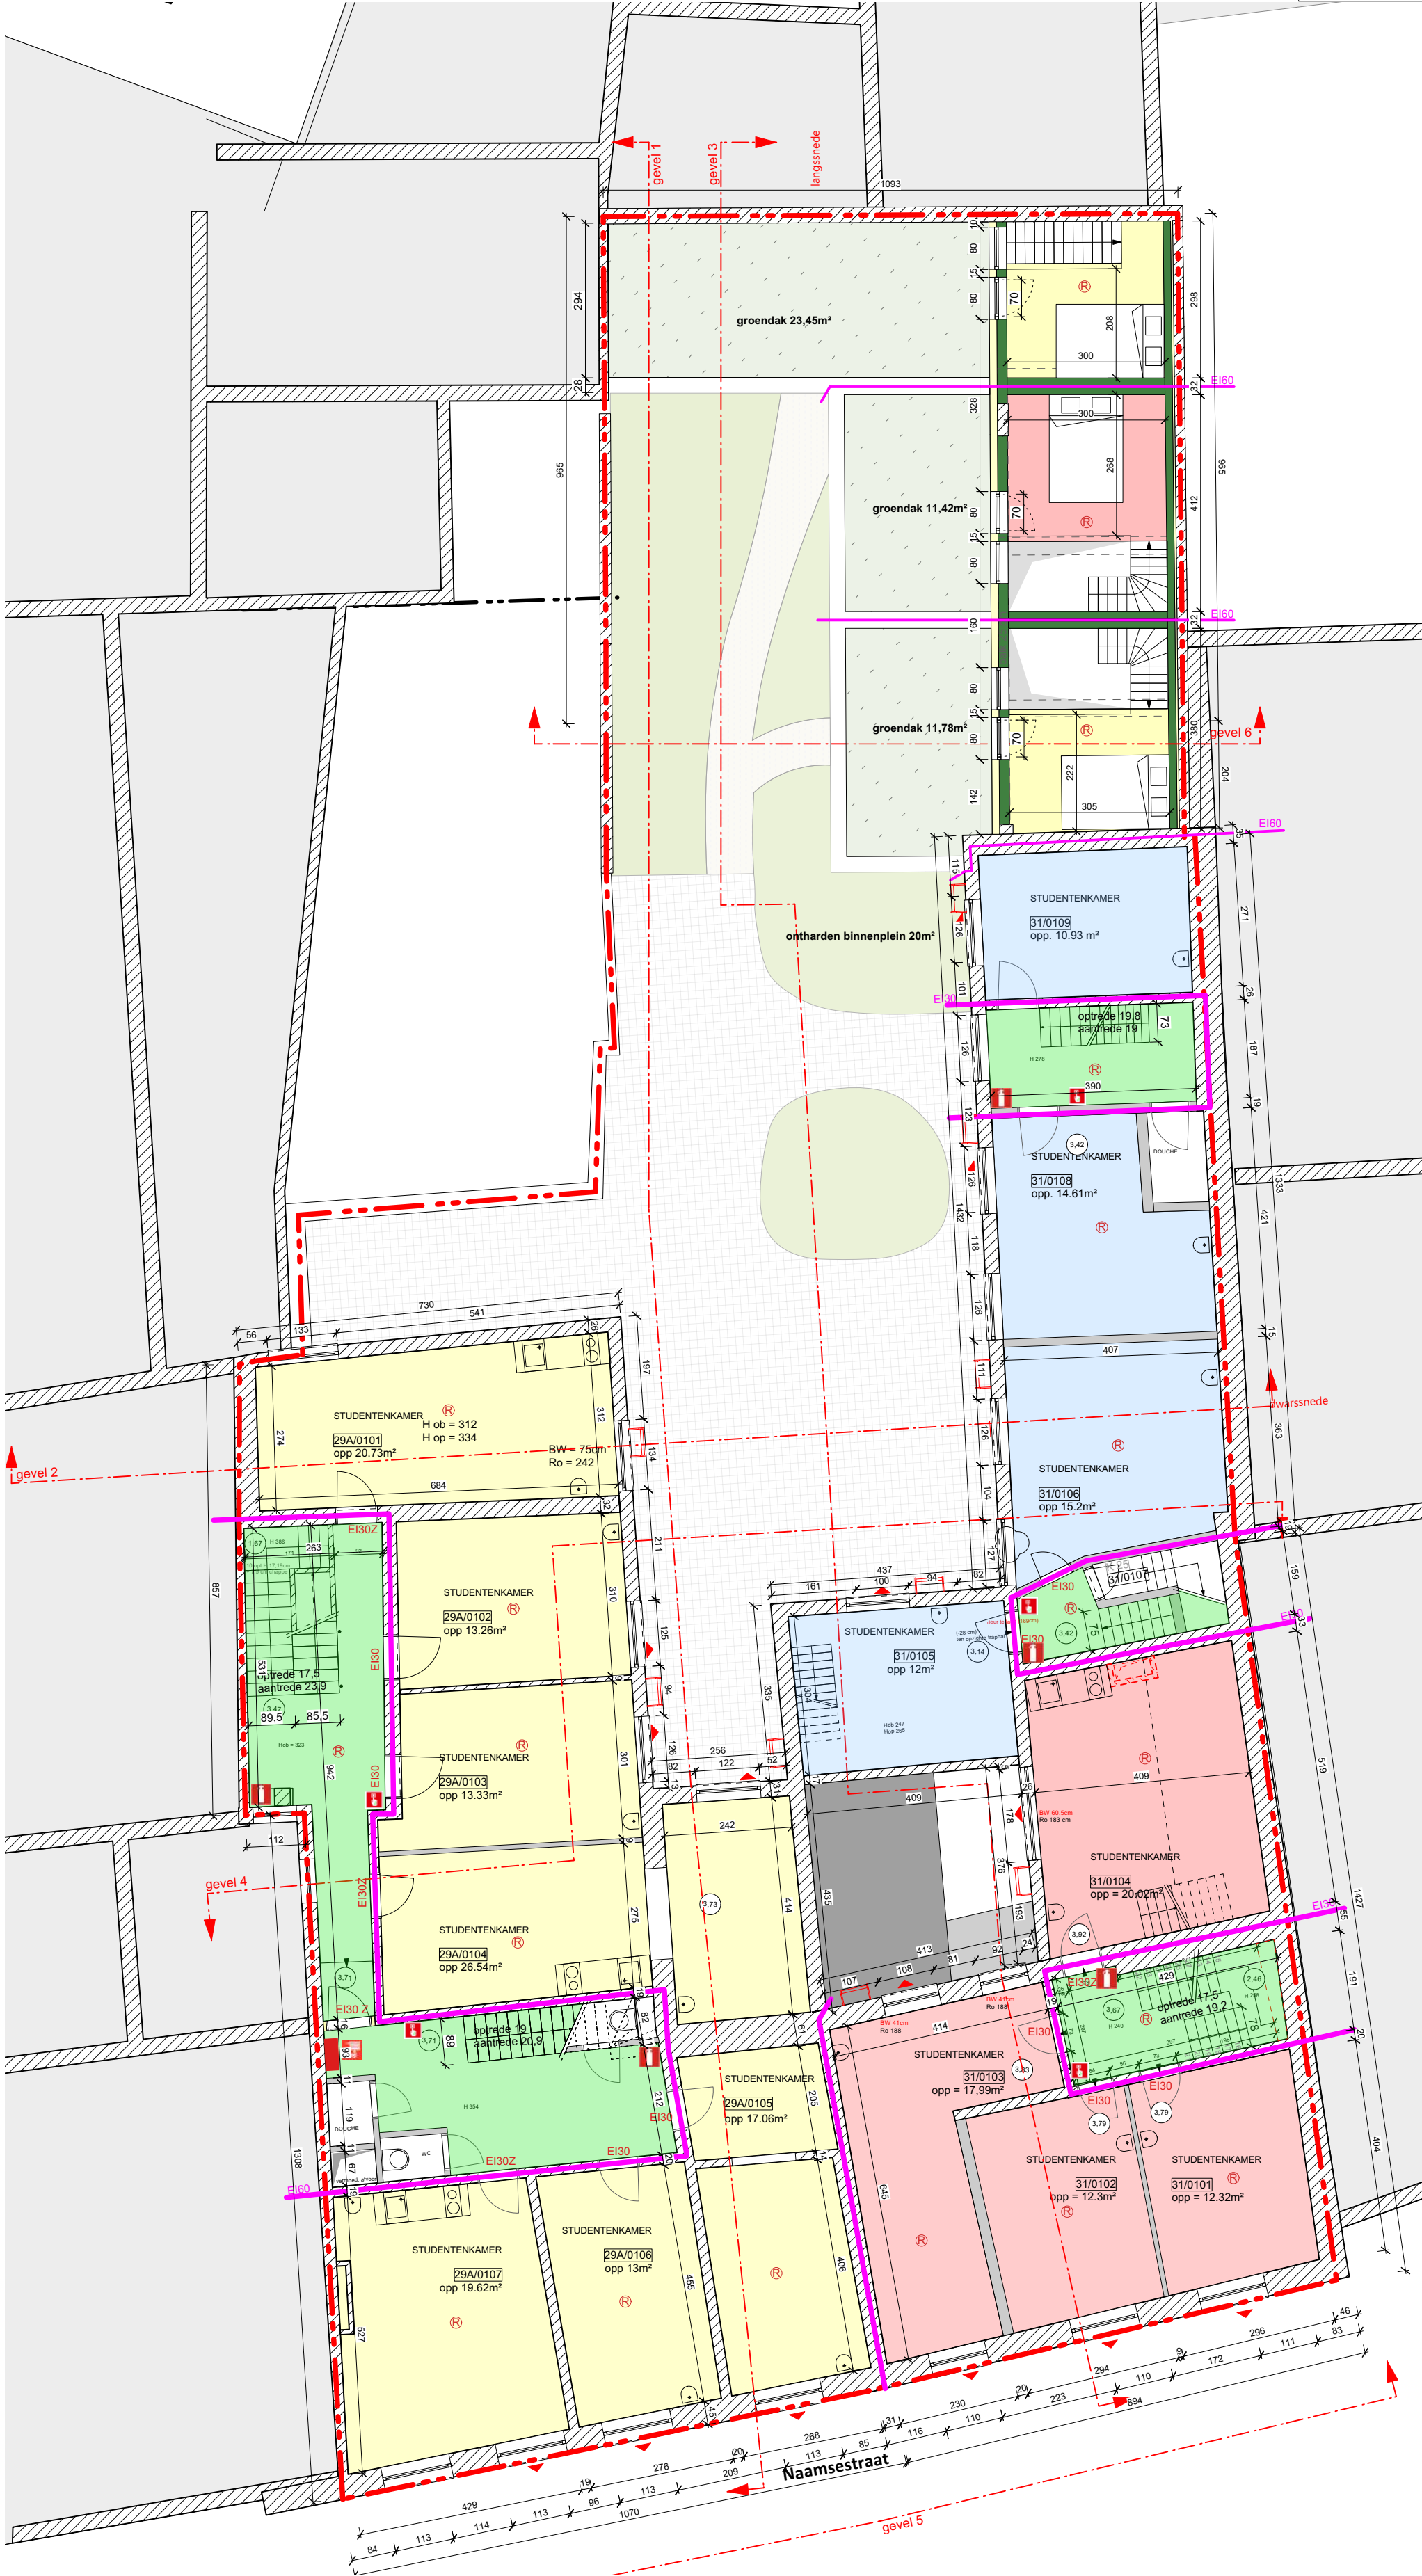



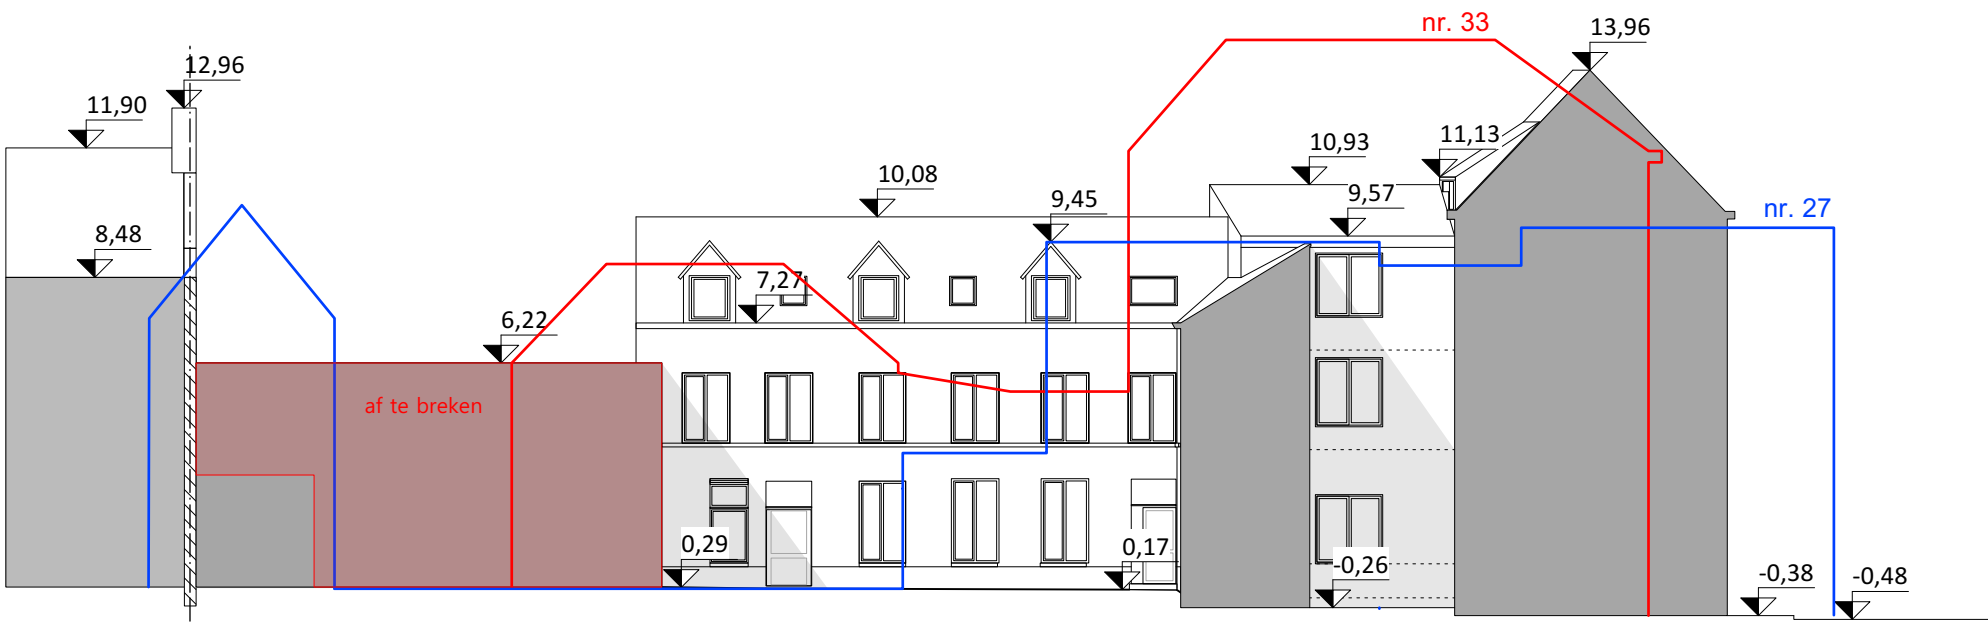


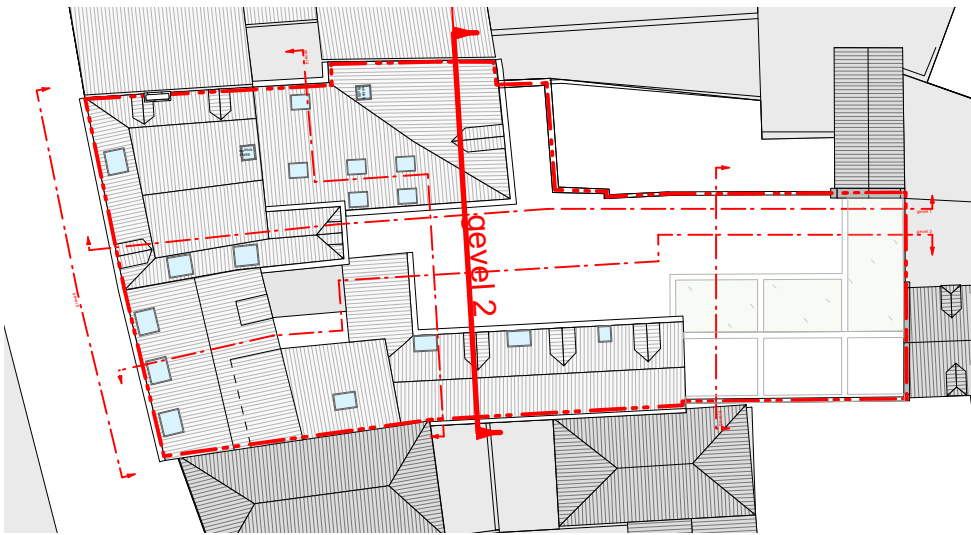


Dit plan is een bijlage bij het advies van de dienst wonen dat werd uitgebracht in functie van de woonkwaliteit binnen deze aanvraag tot omgevingsvergunning.

Het betreft dus geen vergund plan.

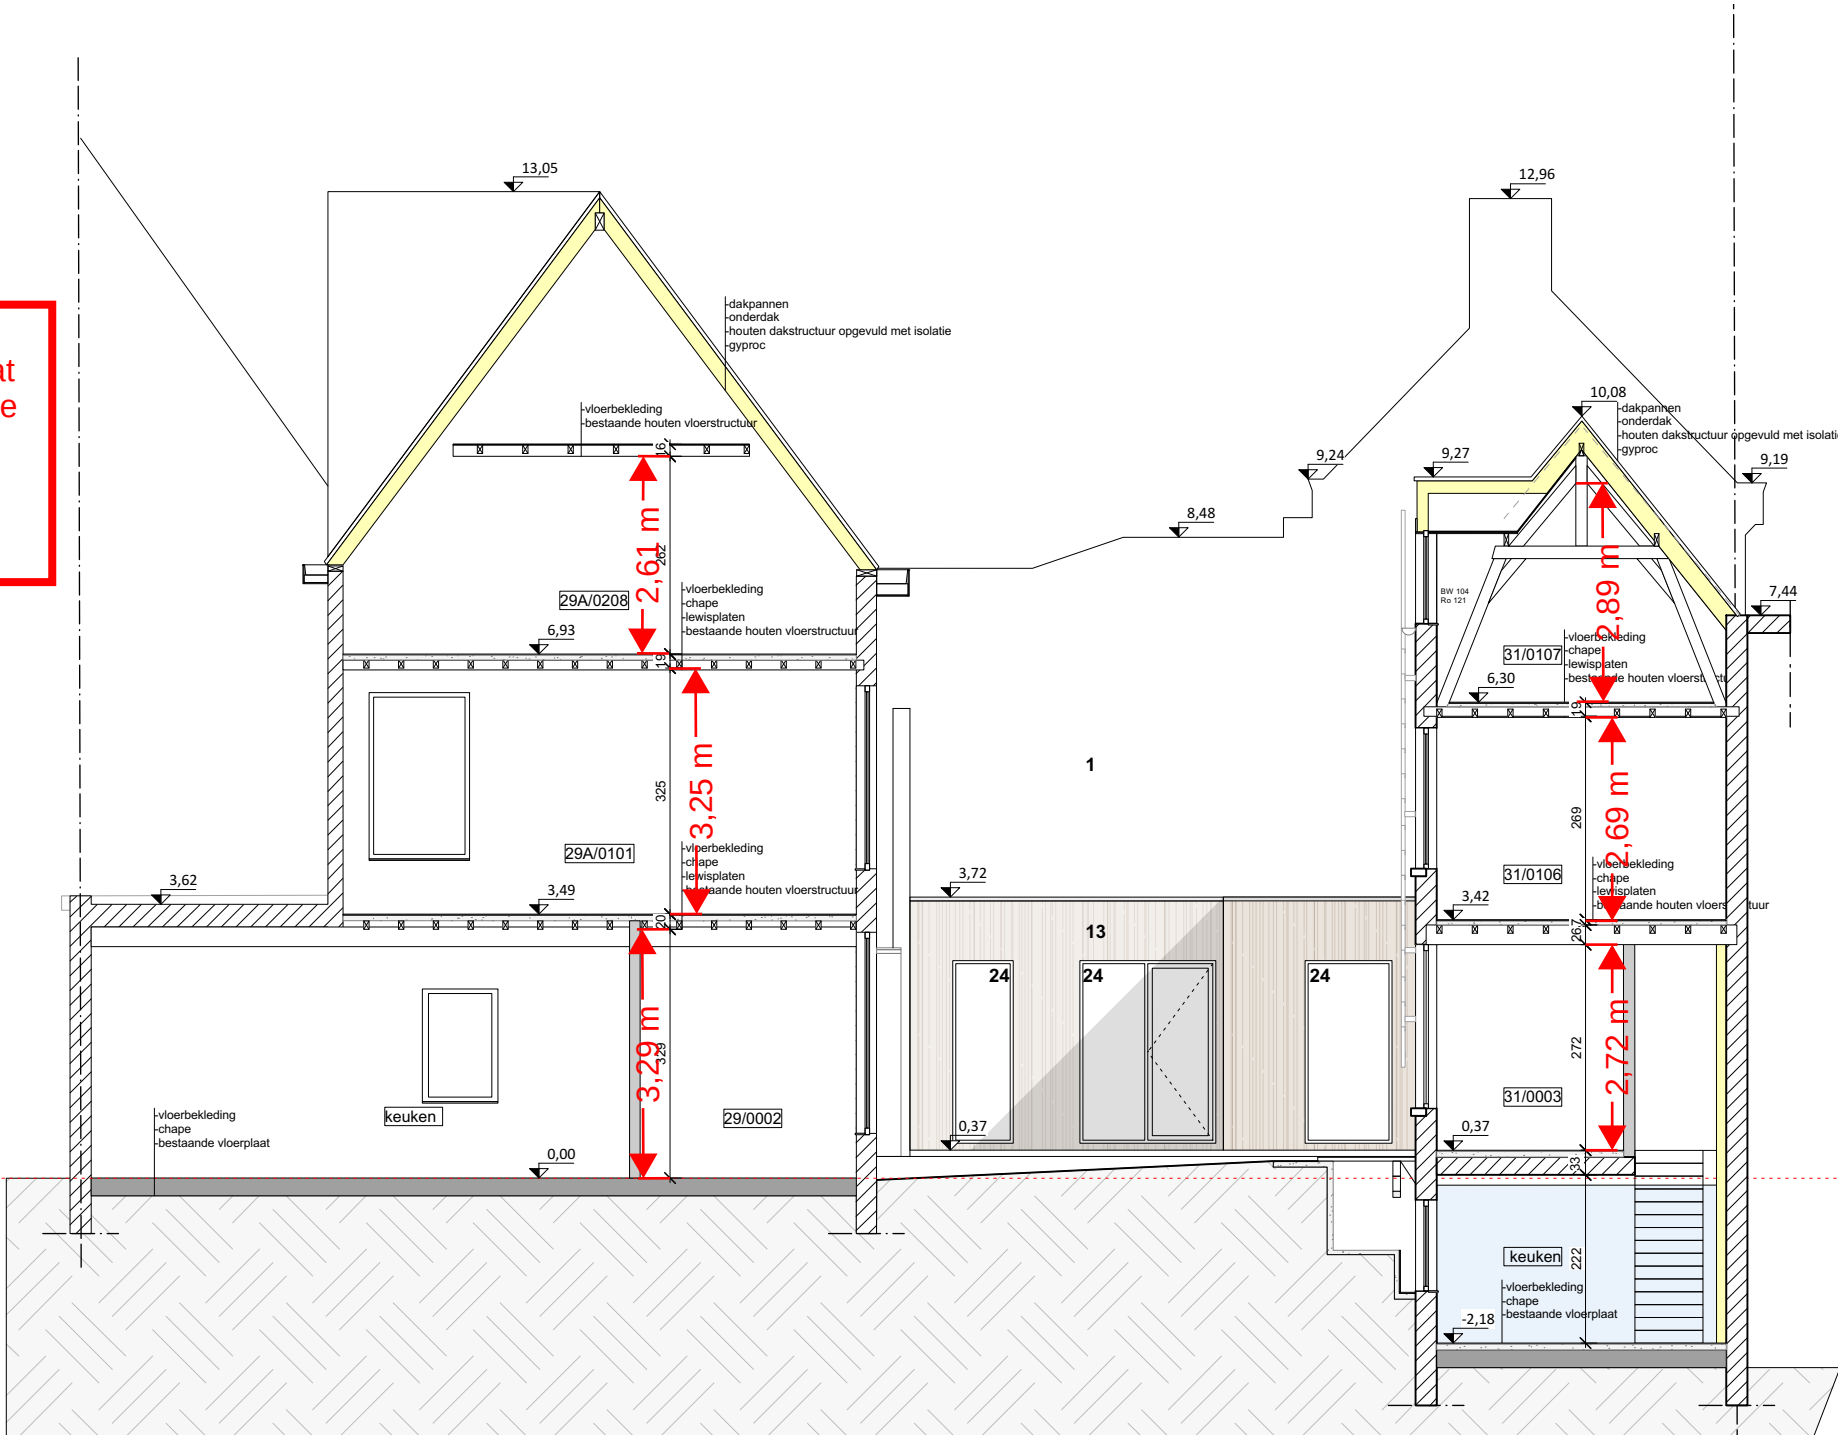

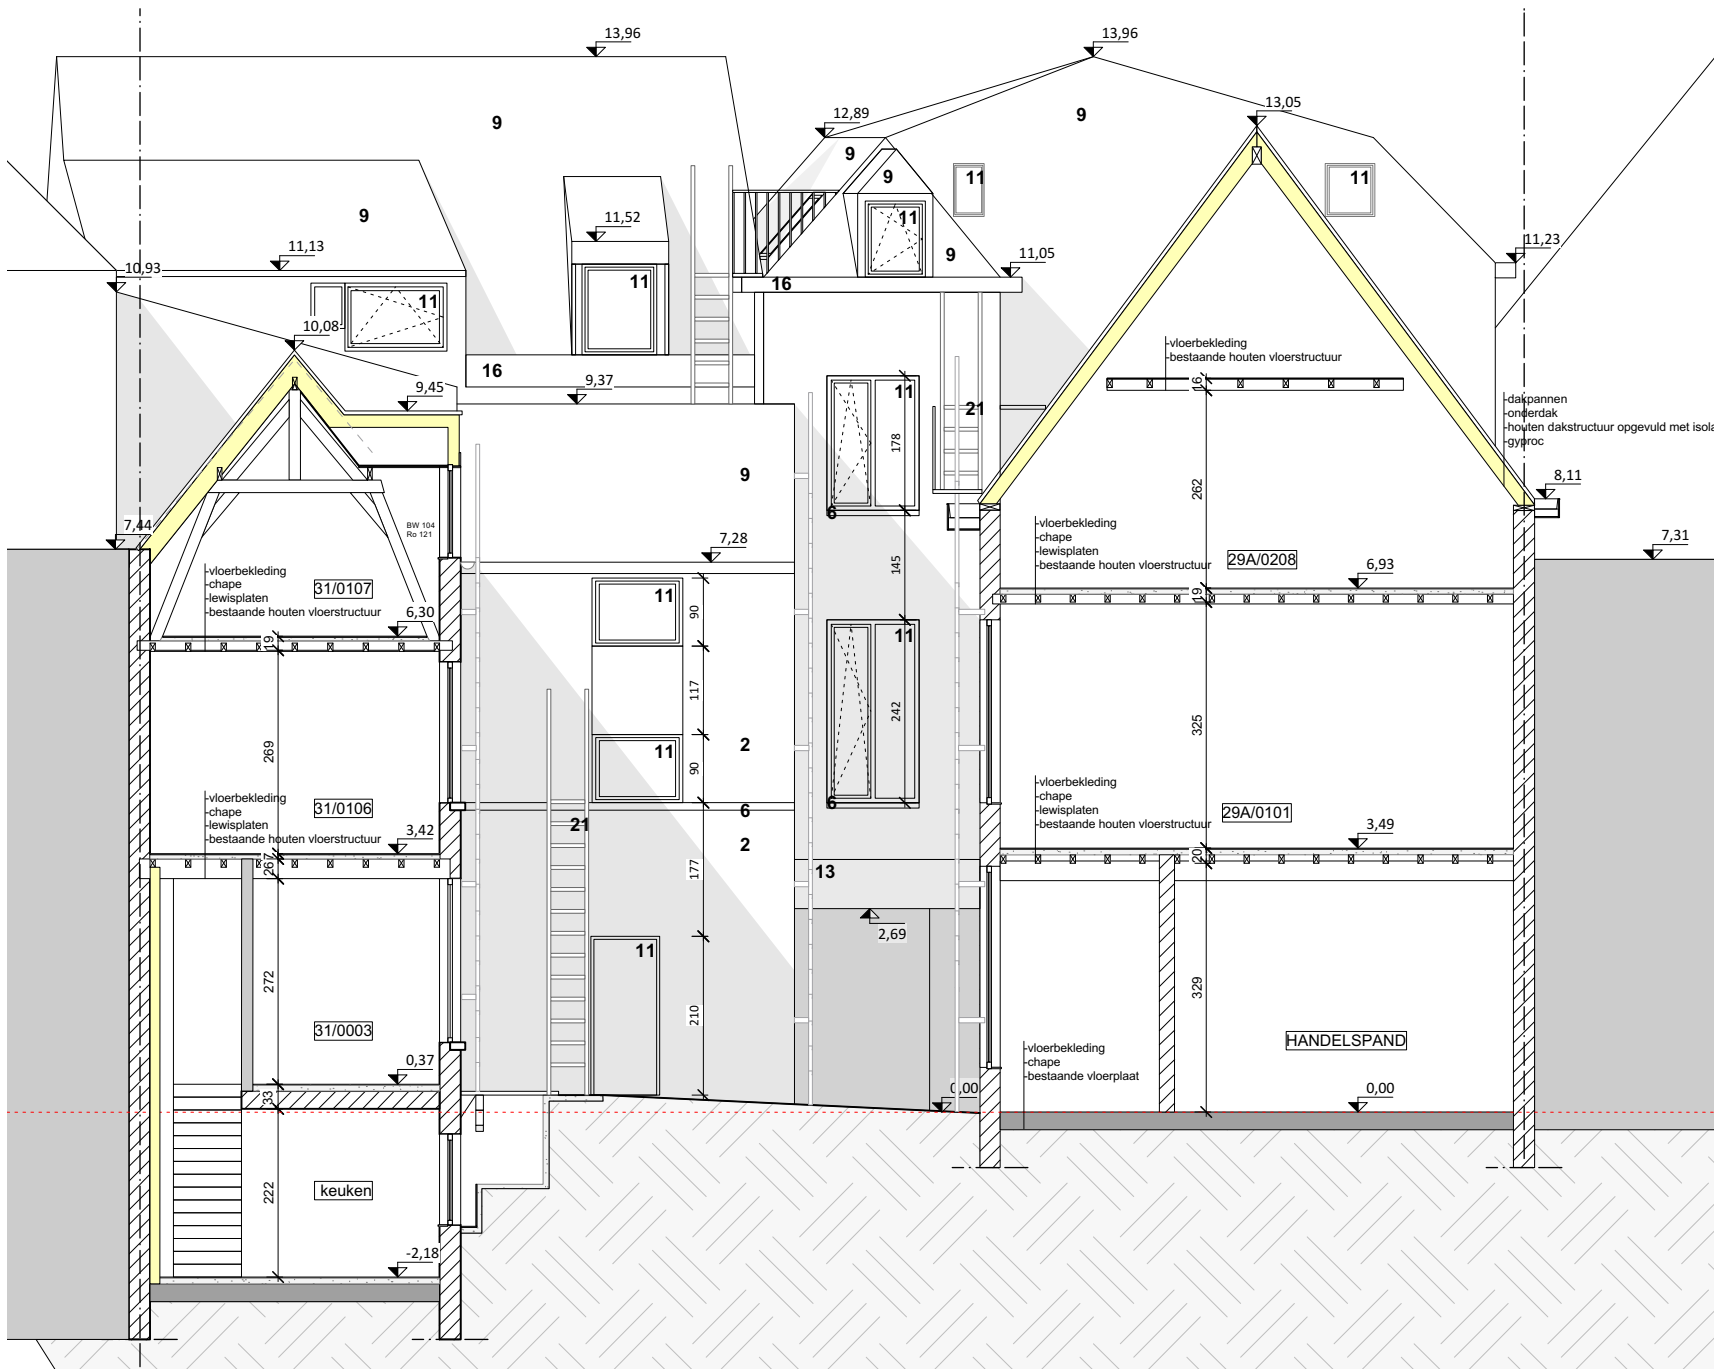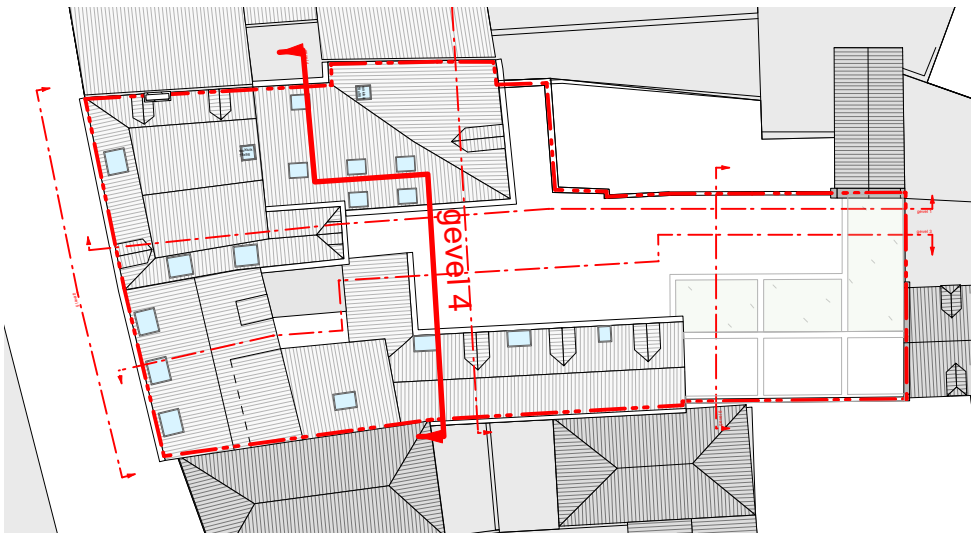

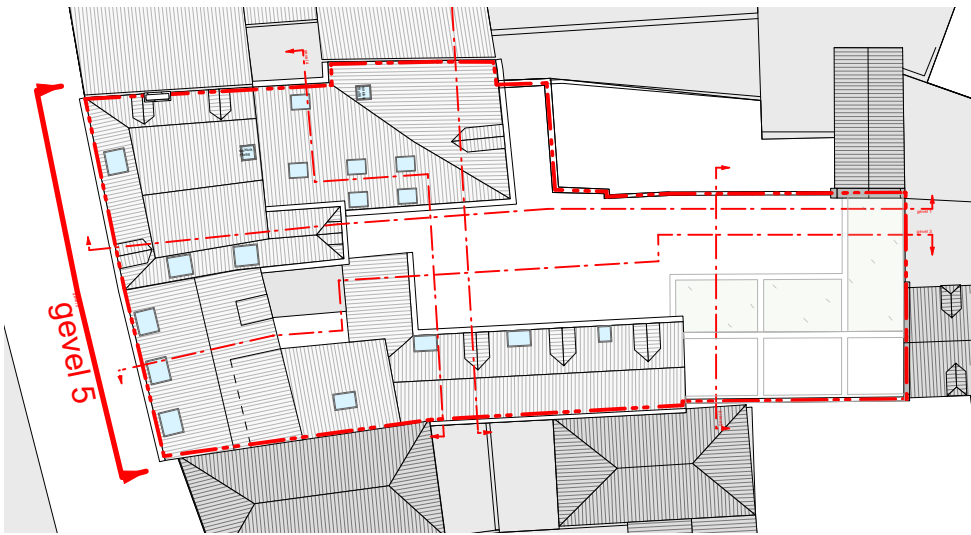

T'JONCK / NILIS
INGENIEUR-ARCHITECTEN

Erasmestraat 83/002
3001 Heverlee
T: +32 16 23 45 48

NAAMSESTRAAT 29
VOORGEVEL - GEVEL 5 - brandweer

nieuwe toestand - ongewijzigd


015

1:100

26/01/2024

BA_NAAMSE 29-31_G_N_04




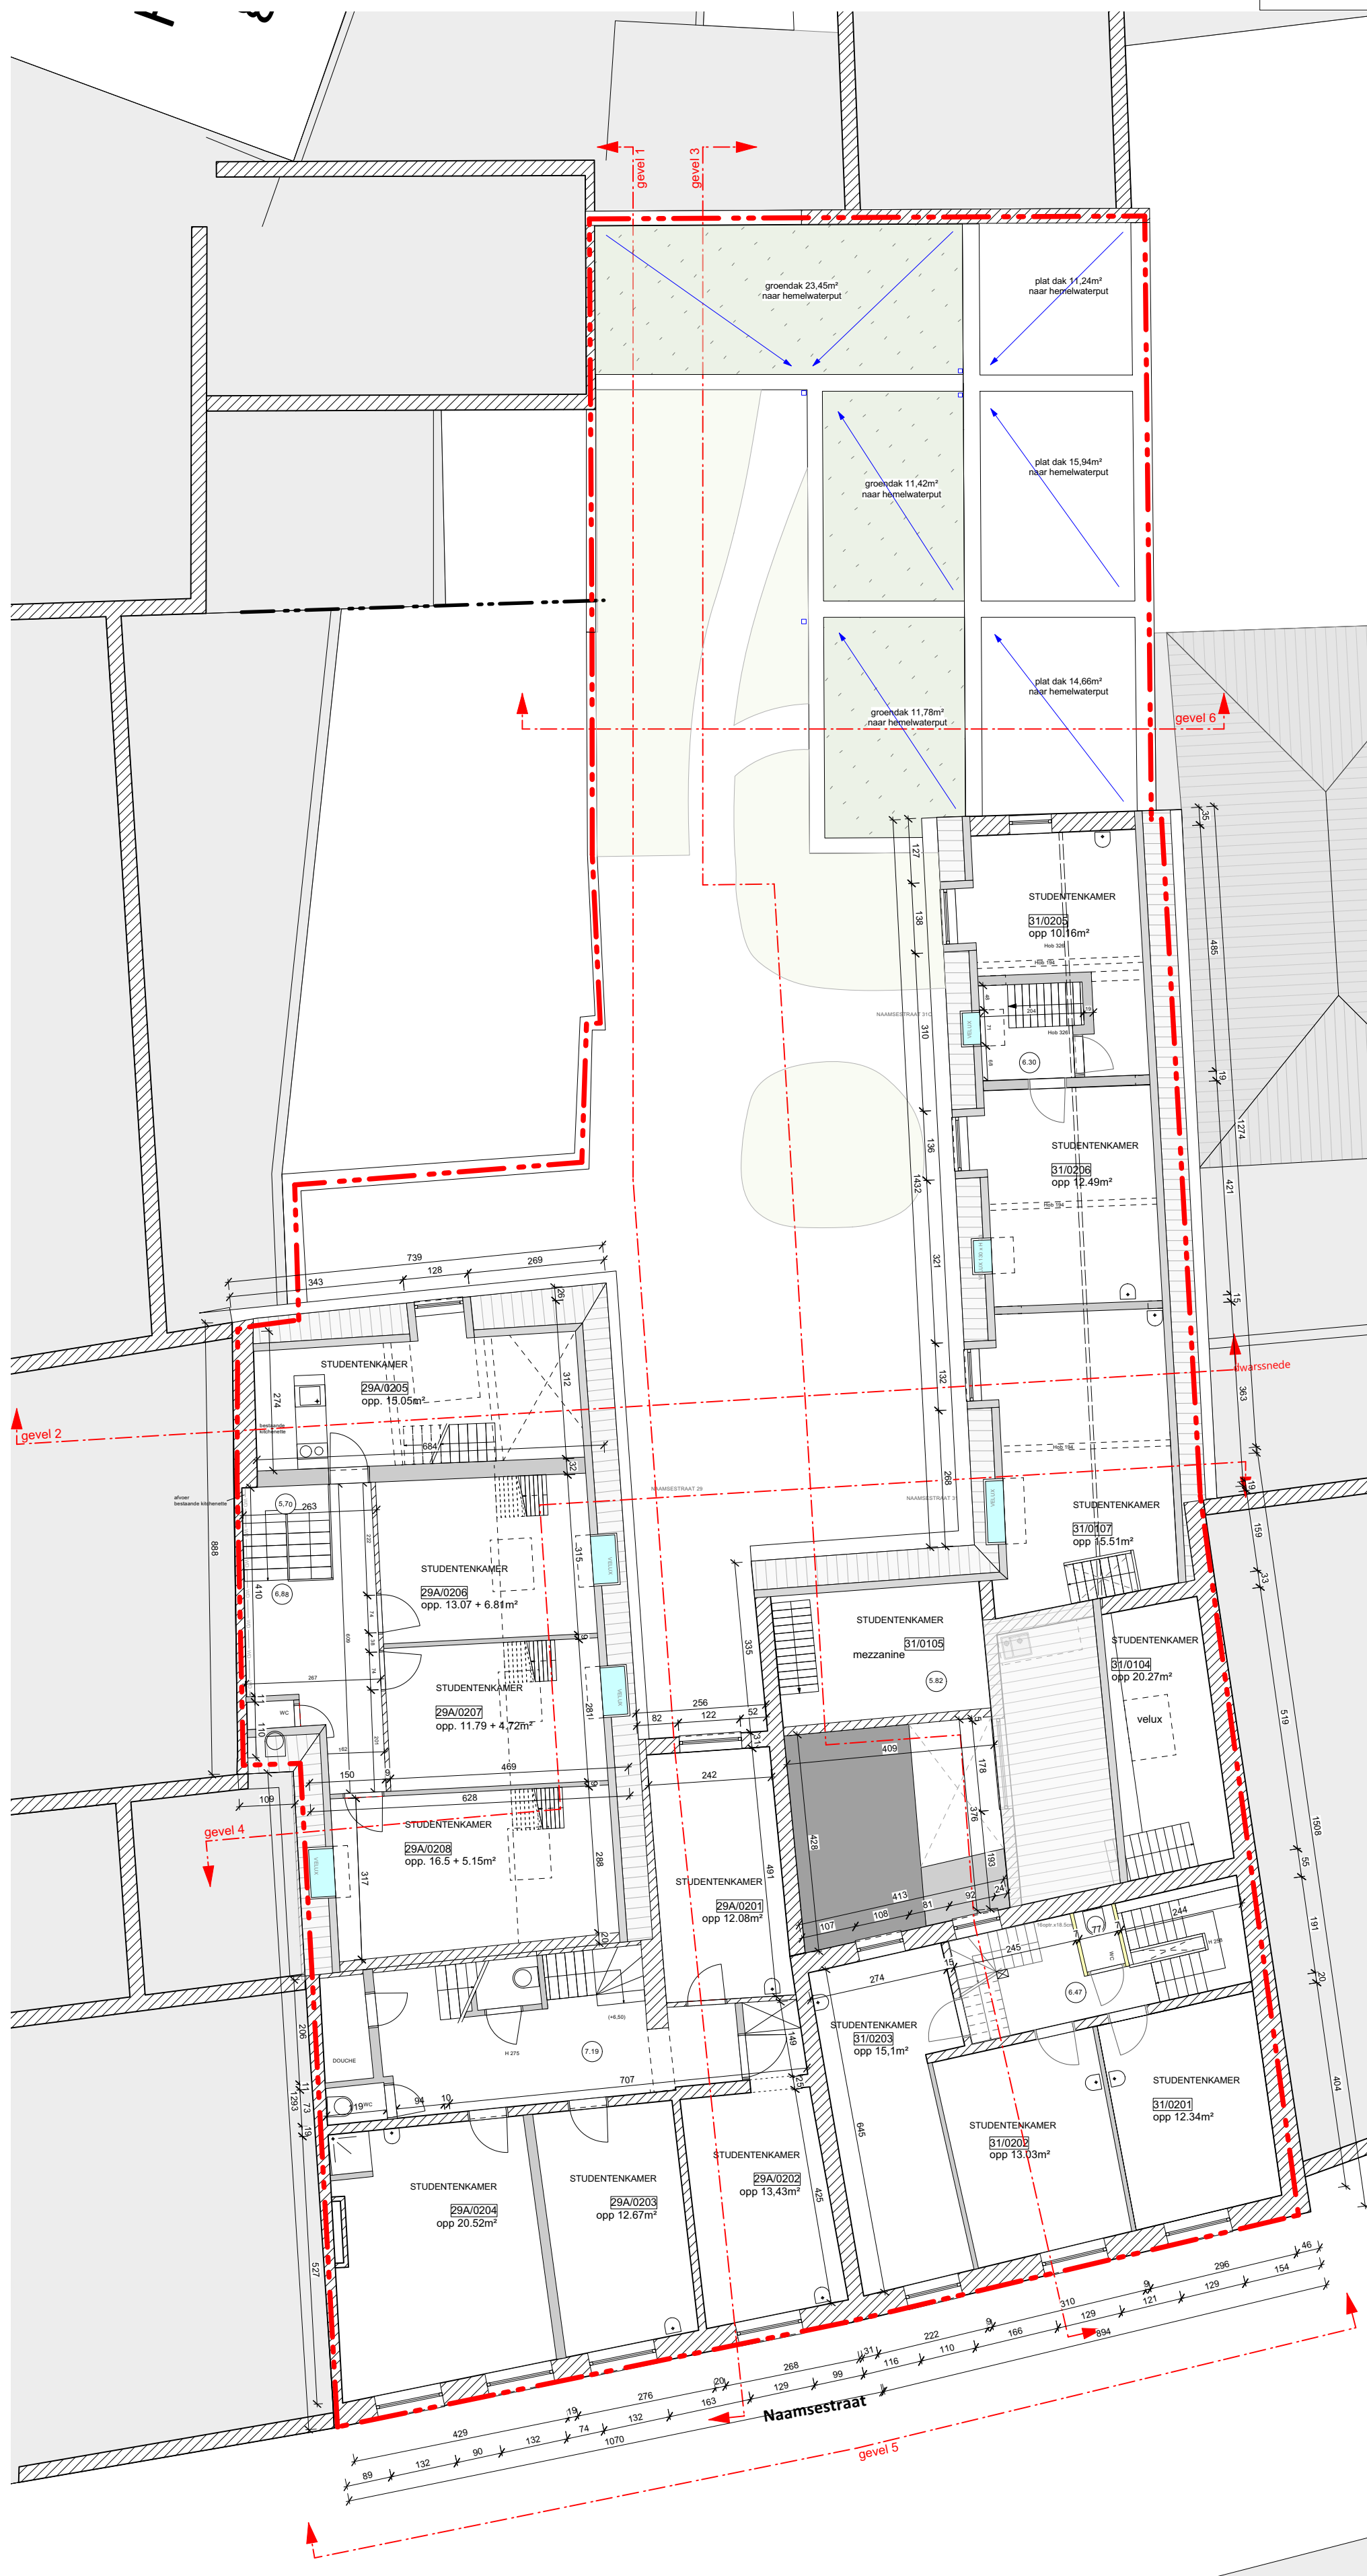








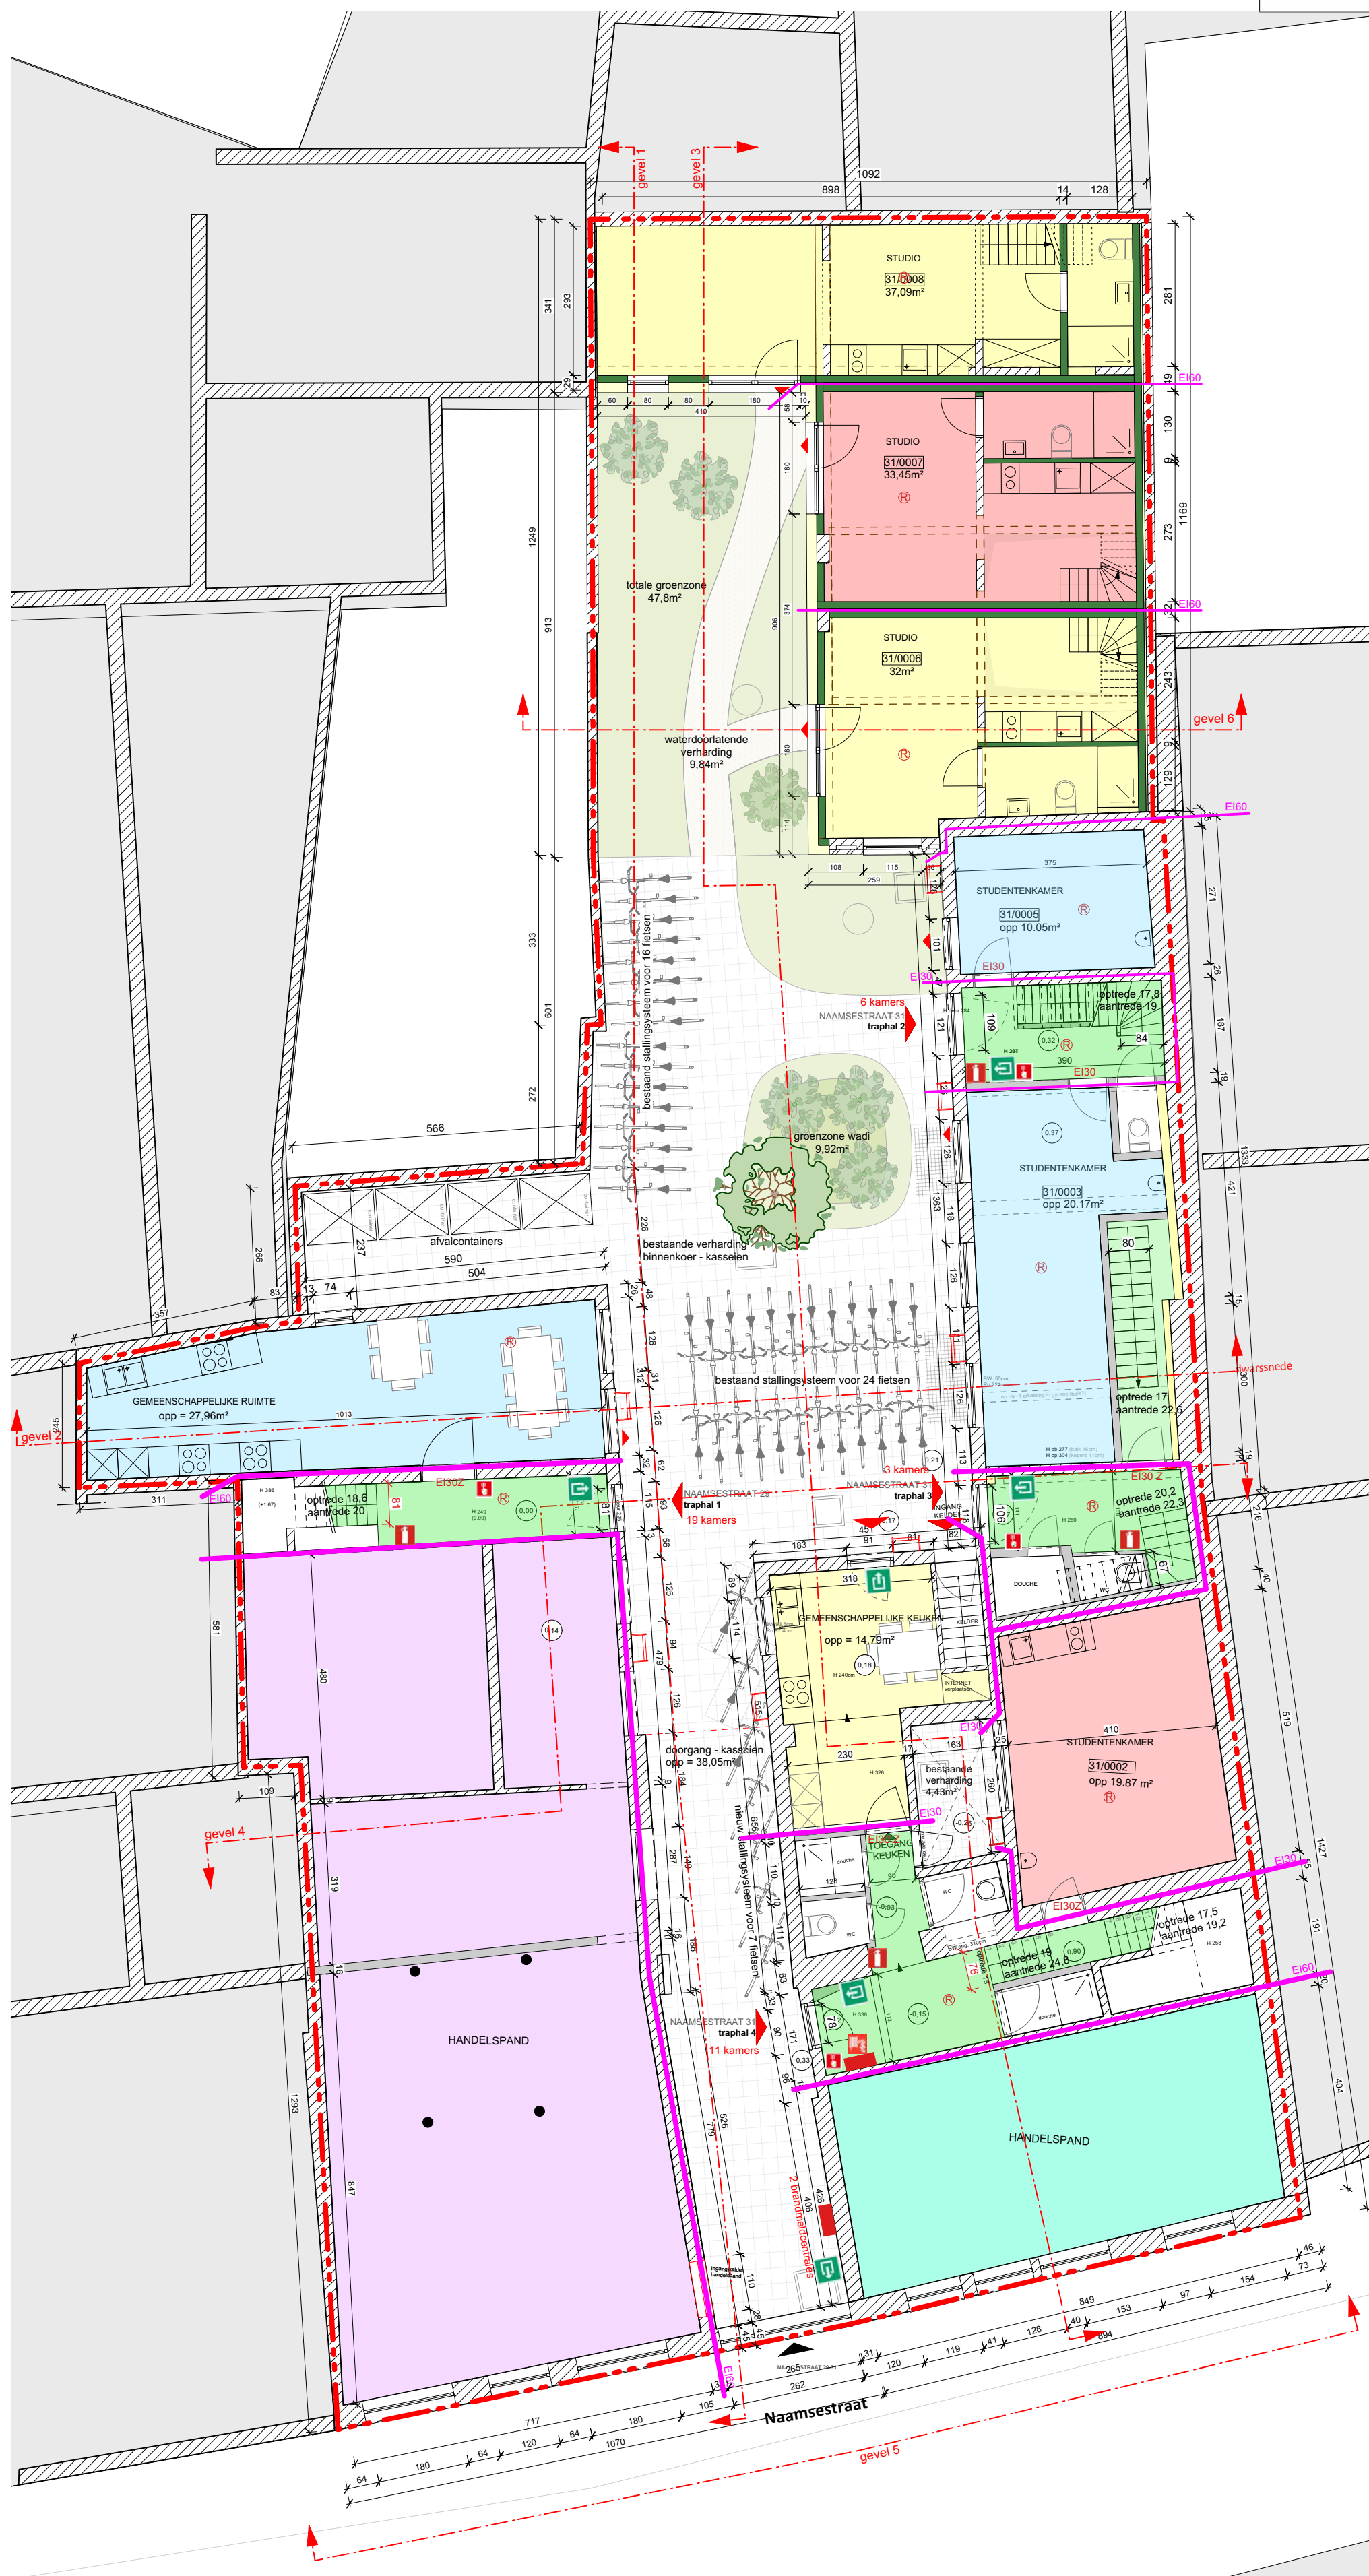


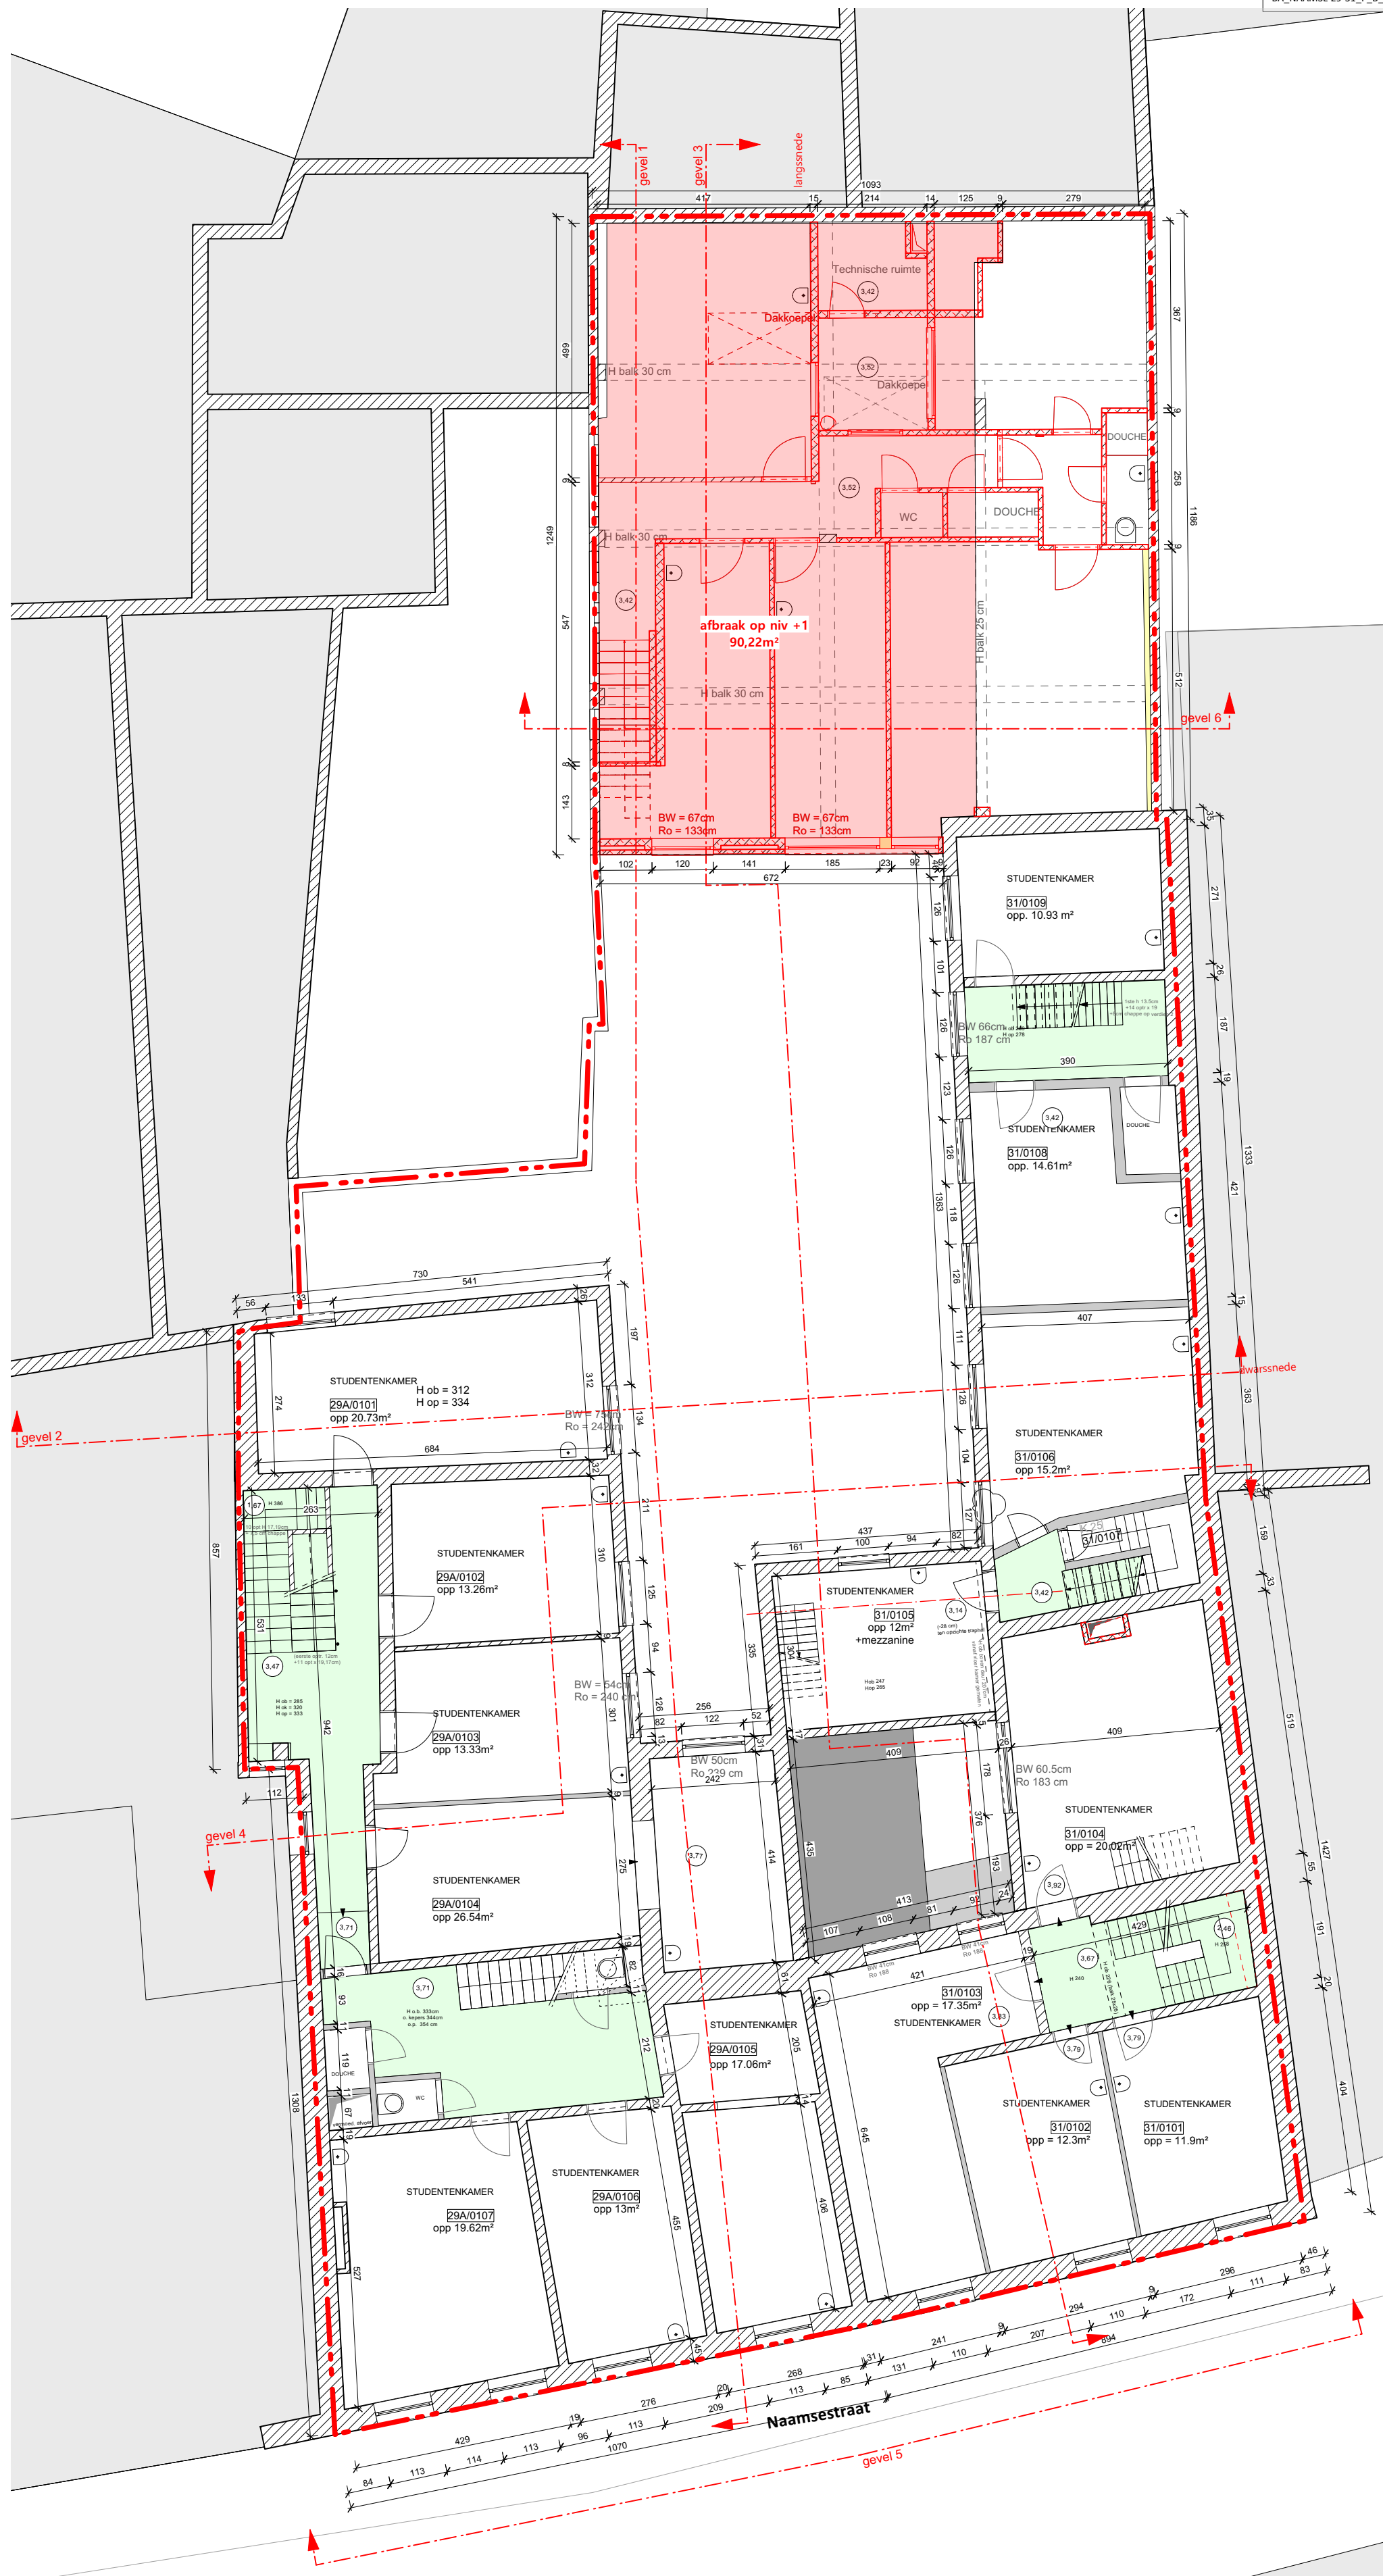


NAAMSESTRAAT 29
GRONDPLAN NIVO +1
nieuwe toestand

0 1 5
1:100

26/01/2024
BA_NAAMSE 29-31_P_N_03

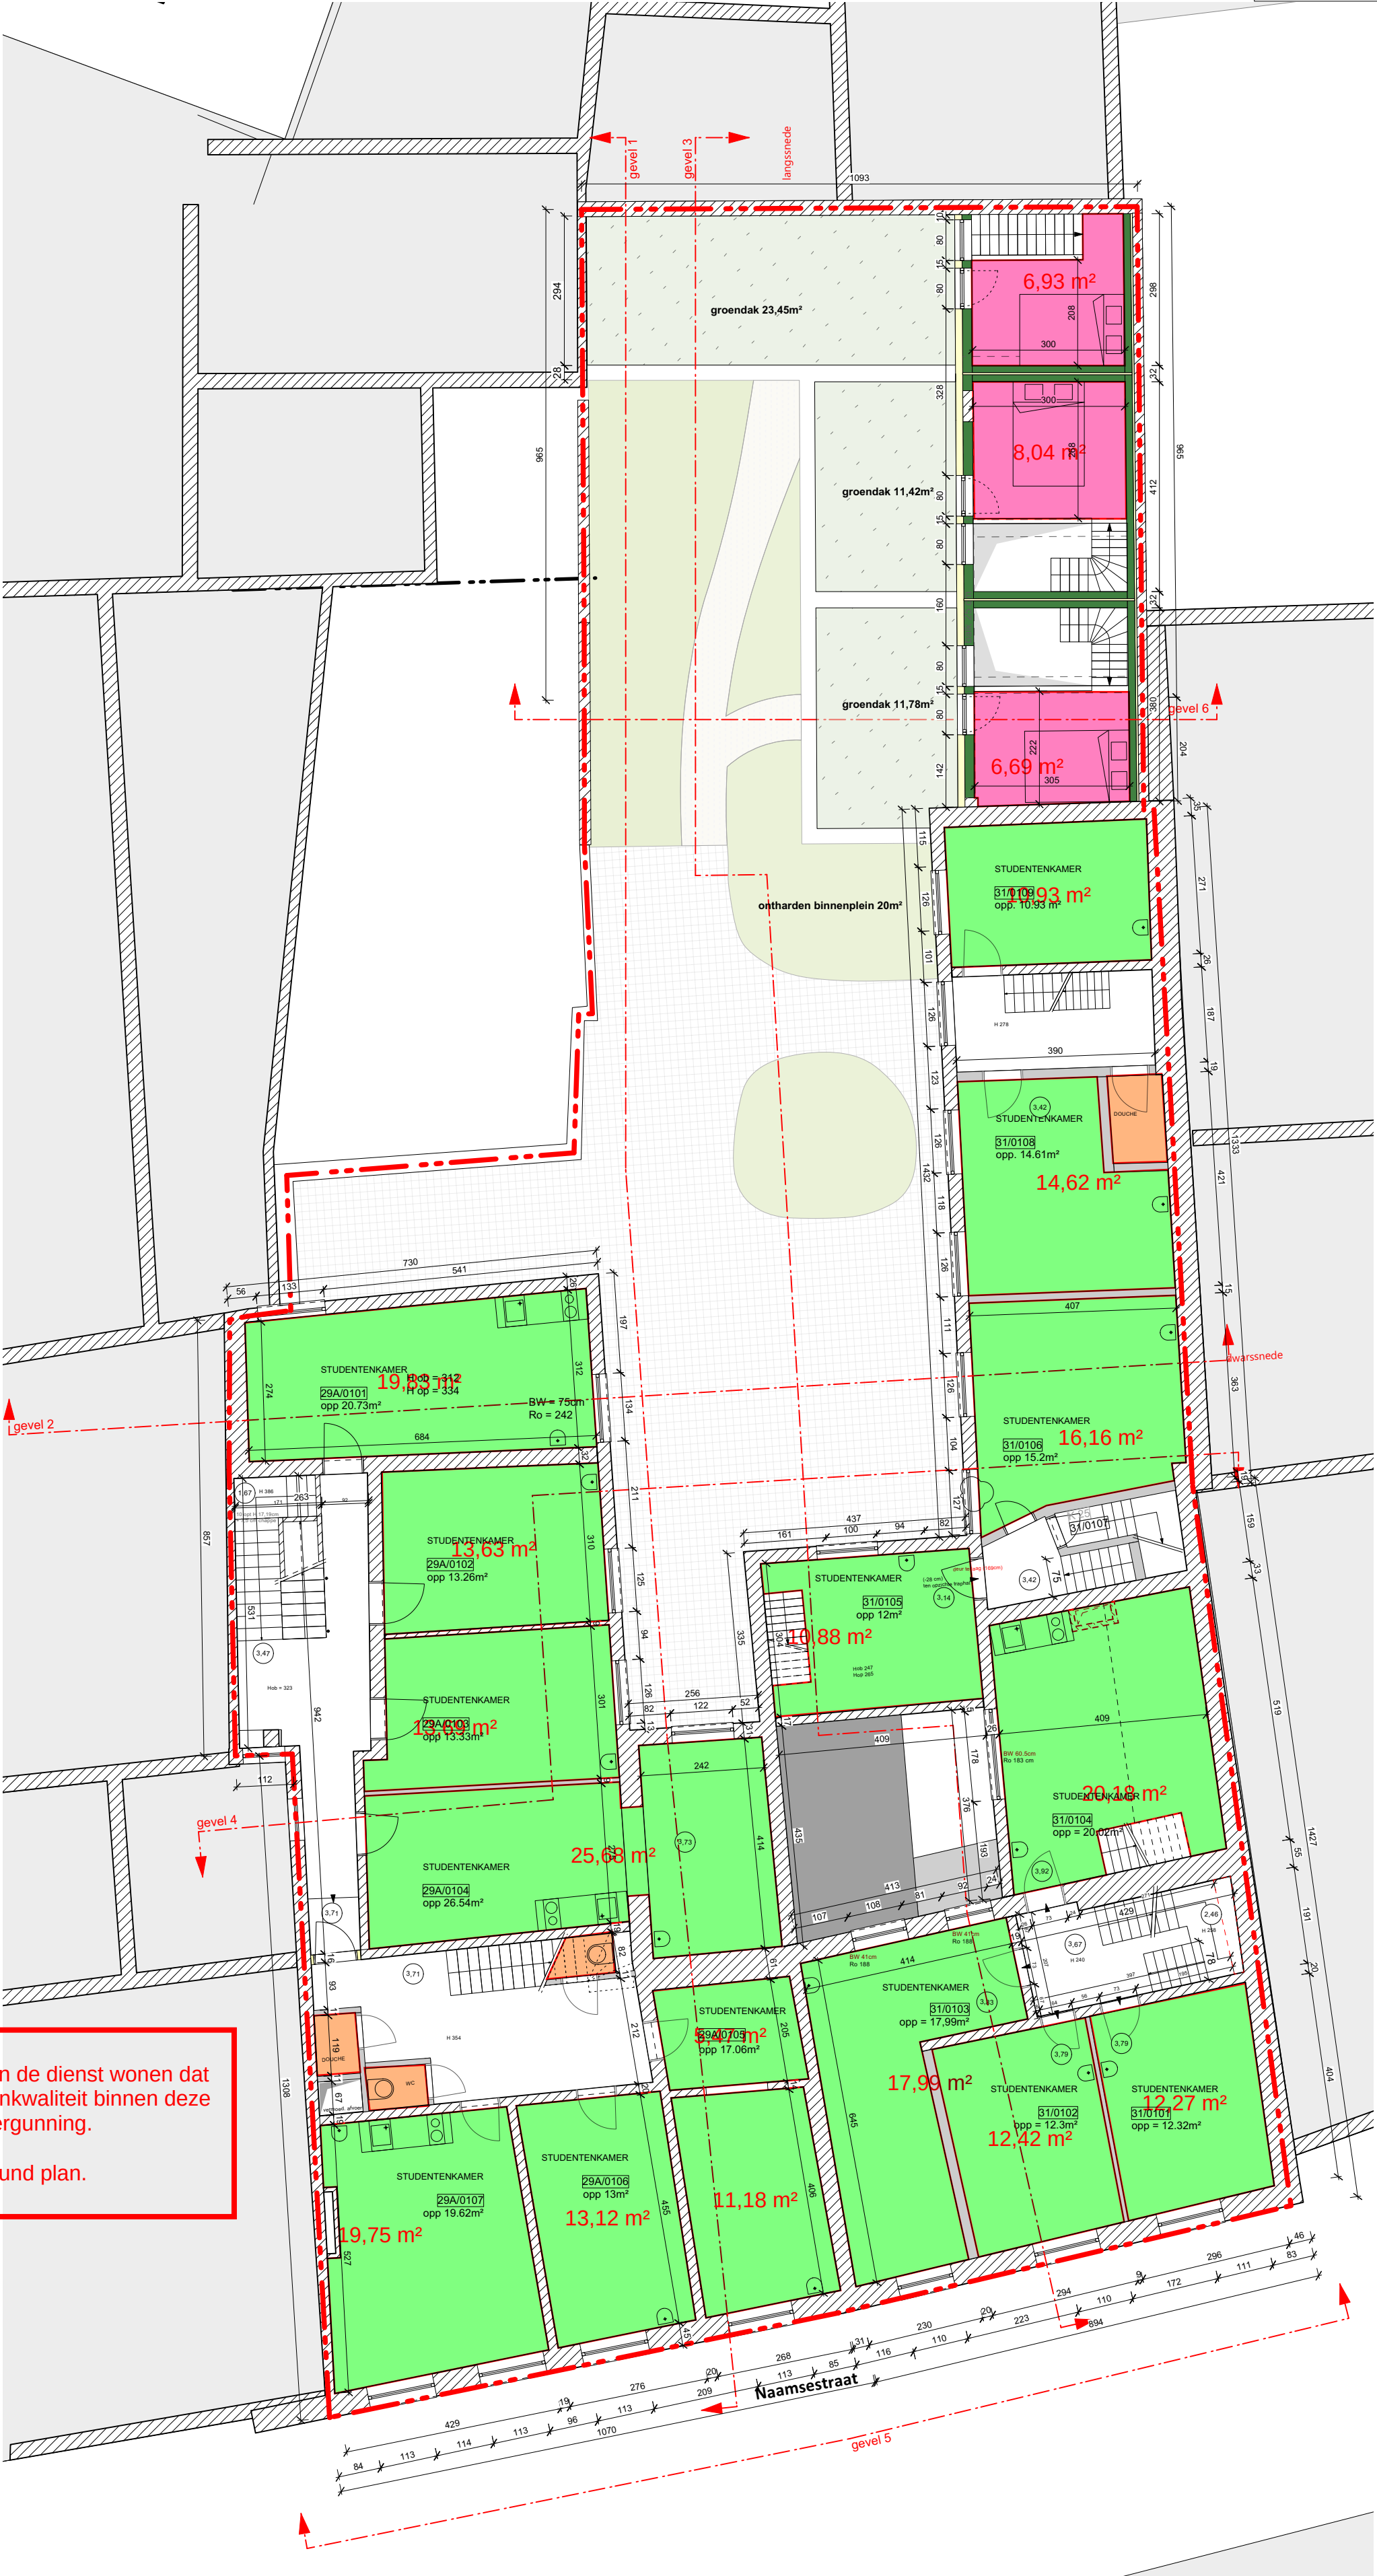

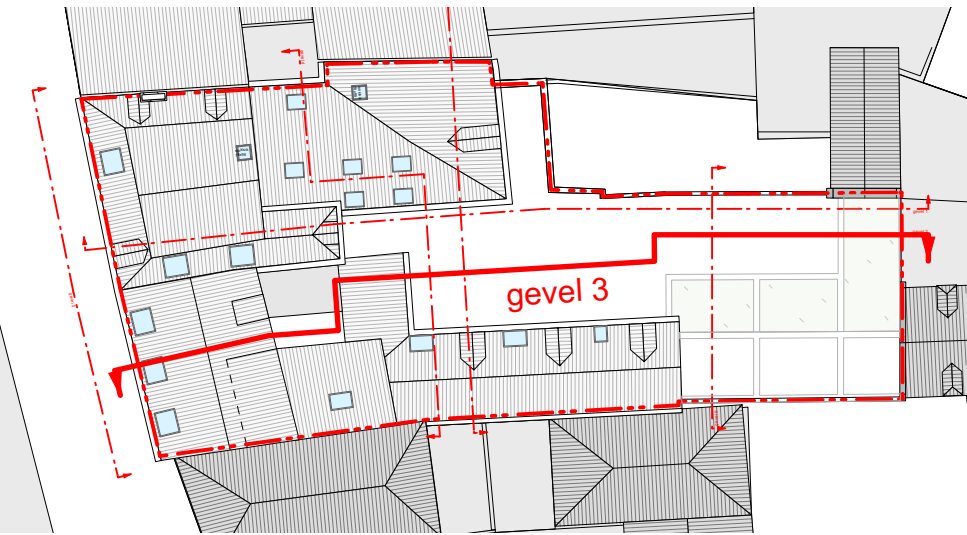

T'JONCK / NILIS

INGENIEUR-ARCHITECTEN

Erasmus Ruelensvest 83/002

3001 Heverlee

T: +32 16 23 45 48

NAAMSESTRAAT 29

ZIJGEVEL - GEVEL 3 - brandweer

nieuwe toestand


012345


1:100

26/03/2024

BA_NAAMSE 29-31_G_N_02



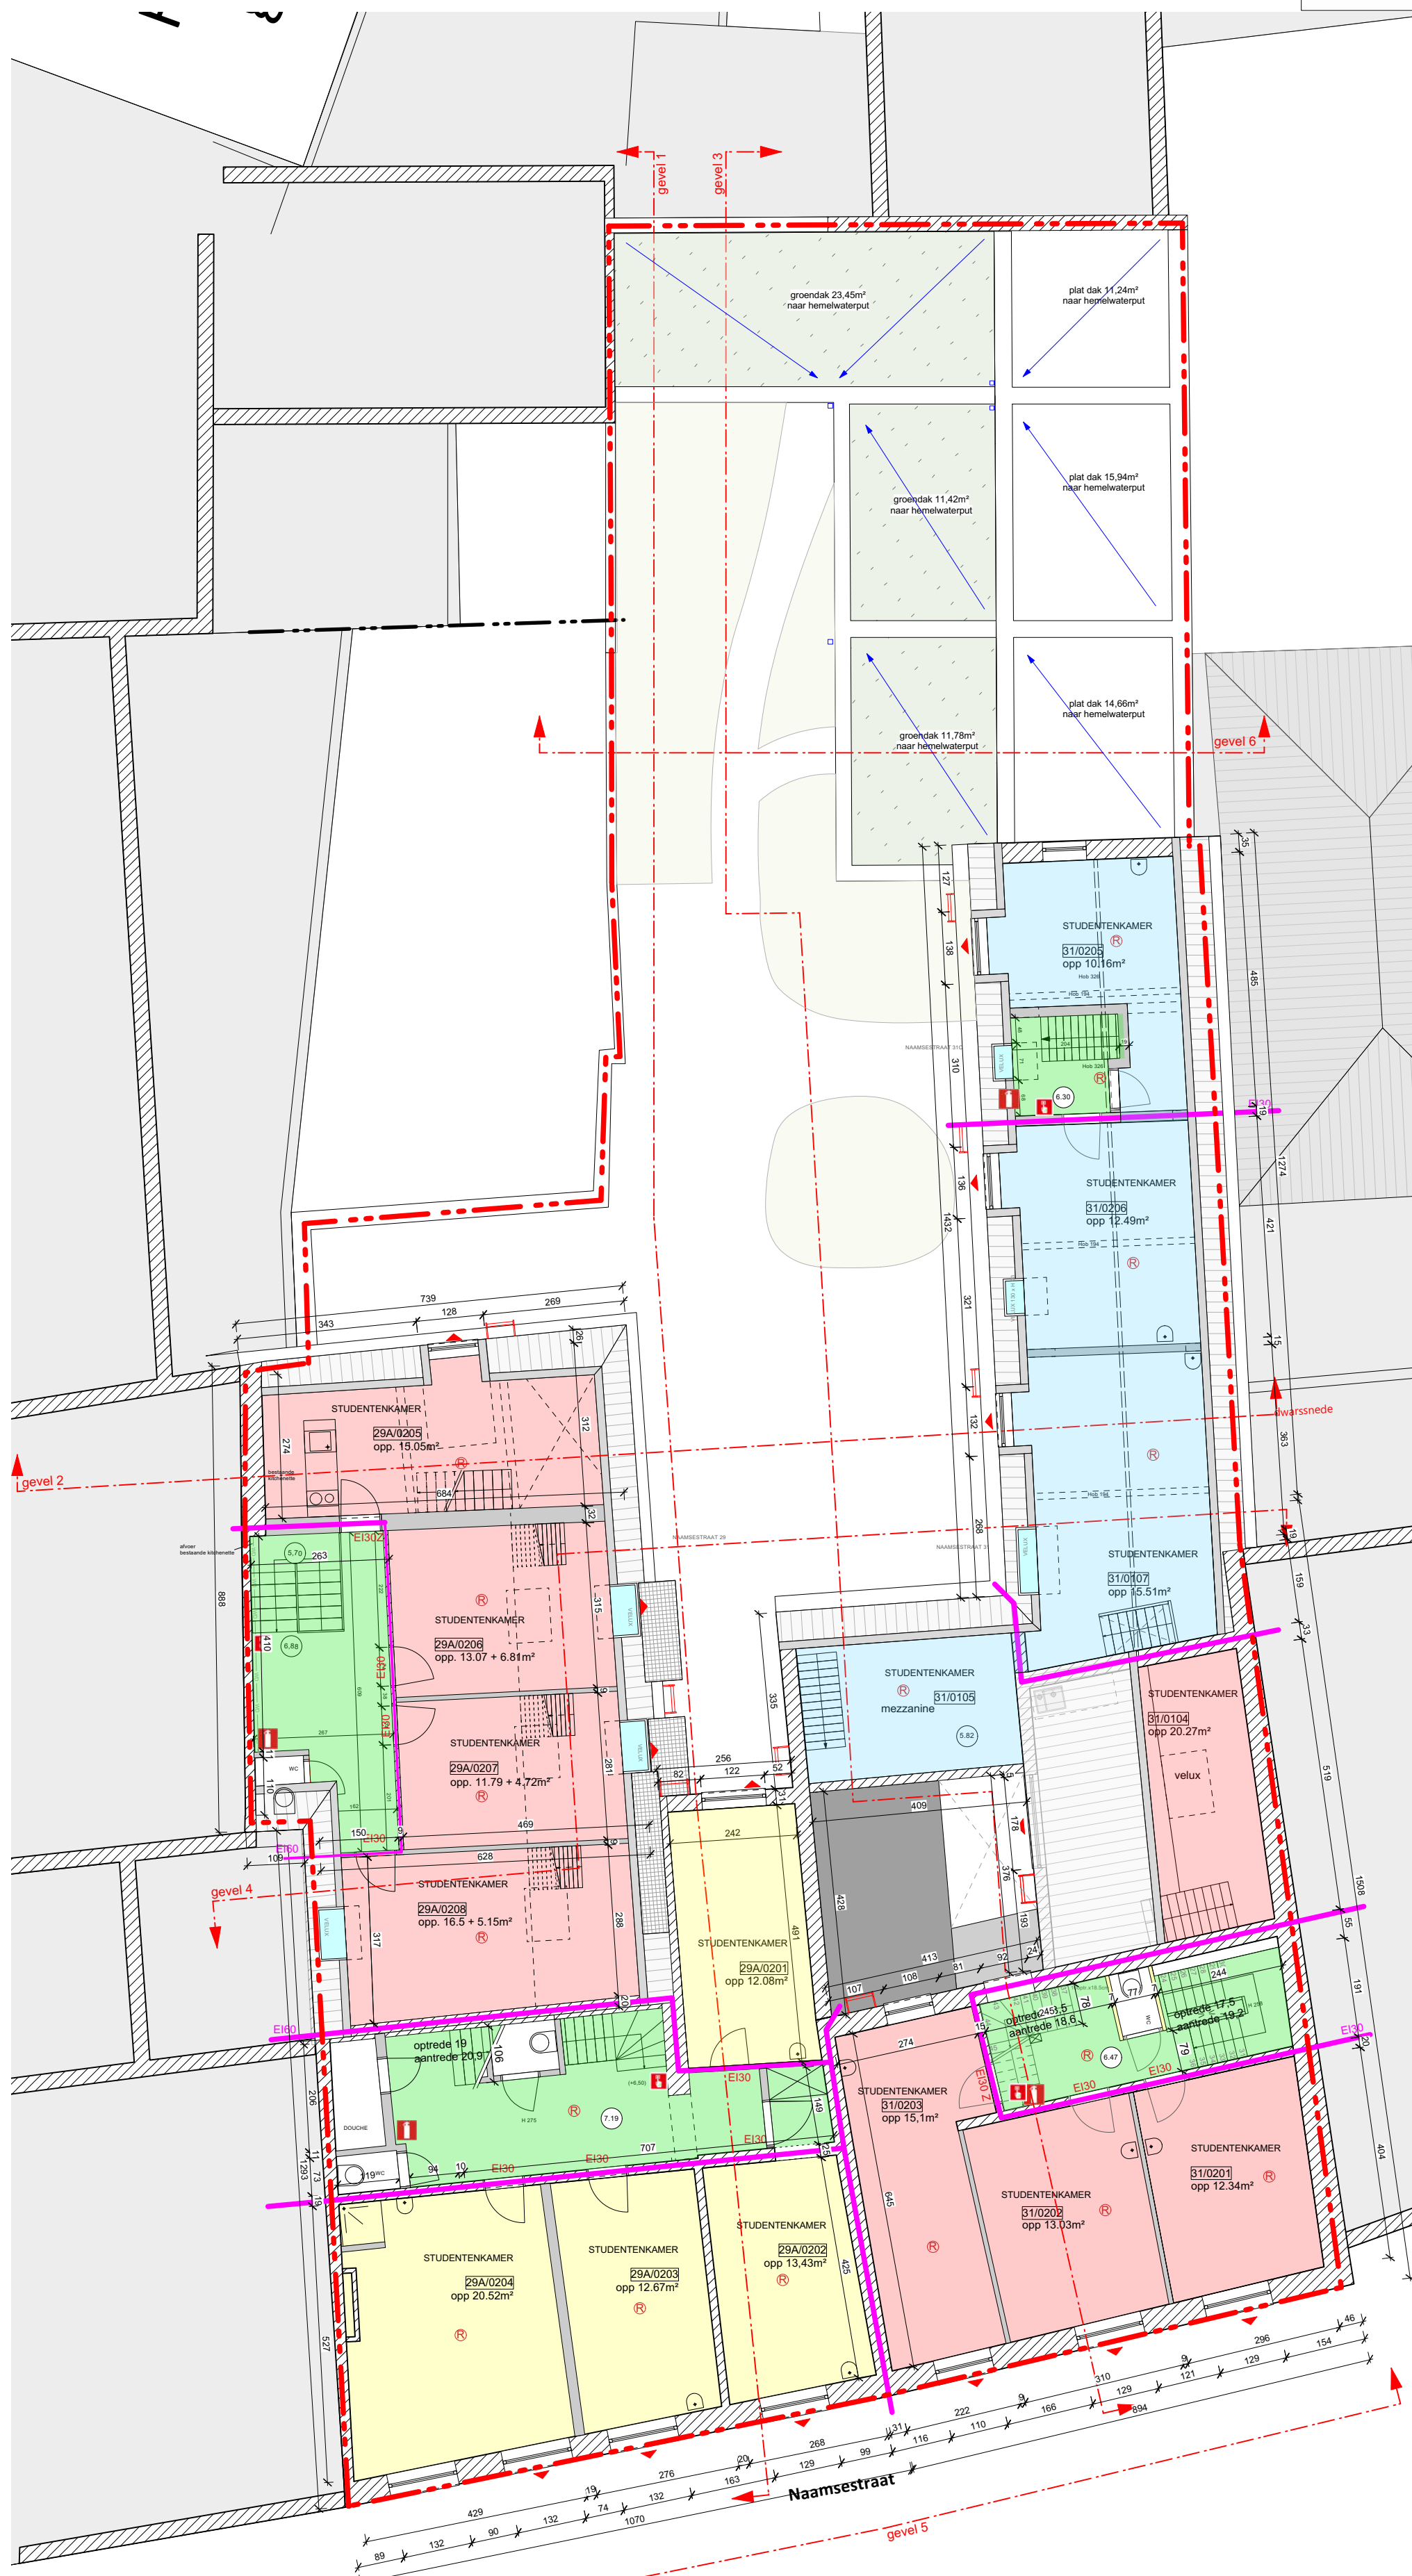

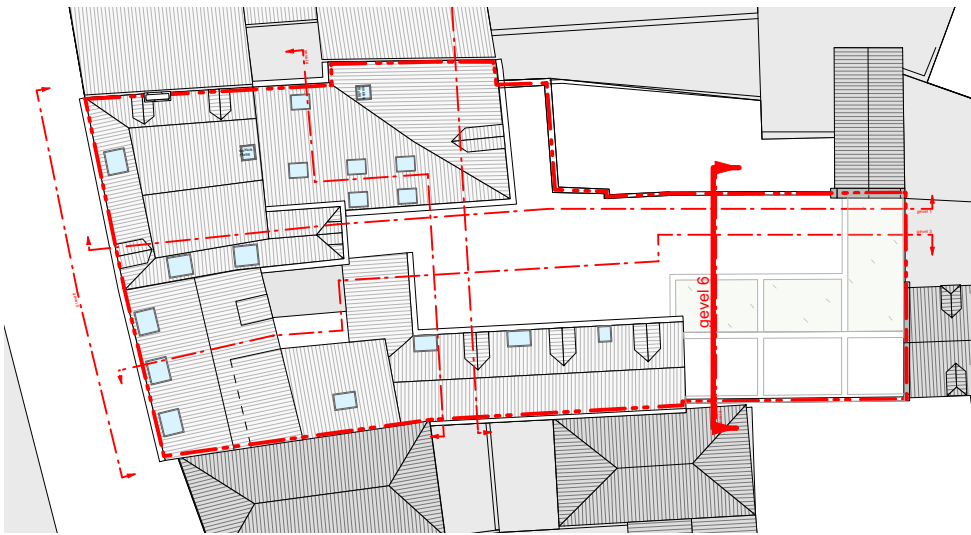

T'JONCK / NILIS

INGENIEUR-ARCHITECTEN

Erasme Ruelensvest 83/002
3001 Heverlee
T: +32 16 23 45 48

NAAMSESTRAAT 29

GEVEL 6

nieuwe toestand

012.5


01


2.5


1:50


26/01/2024

BA_NAAMSE 29-31_G_8_05

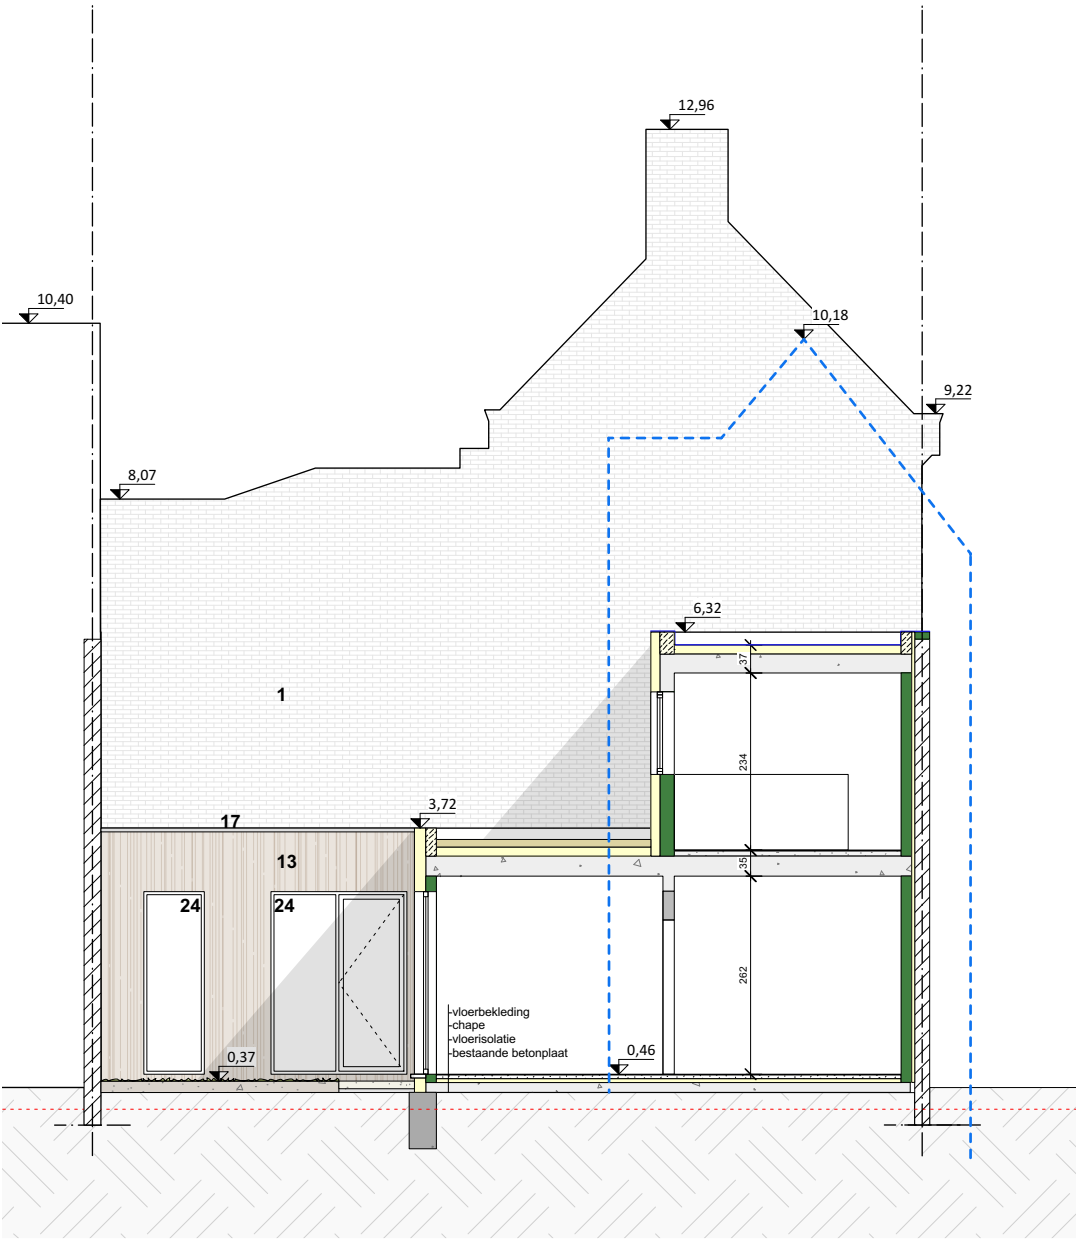

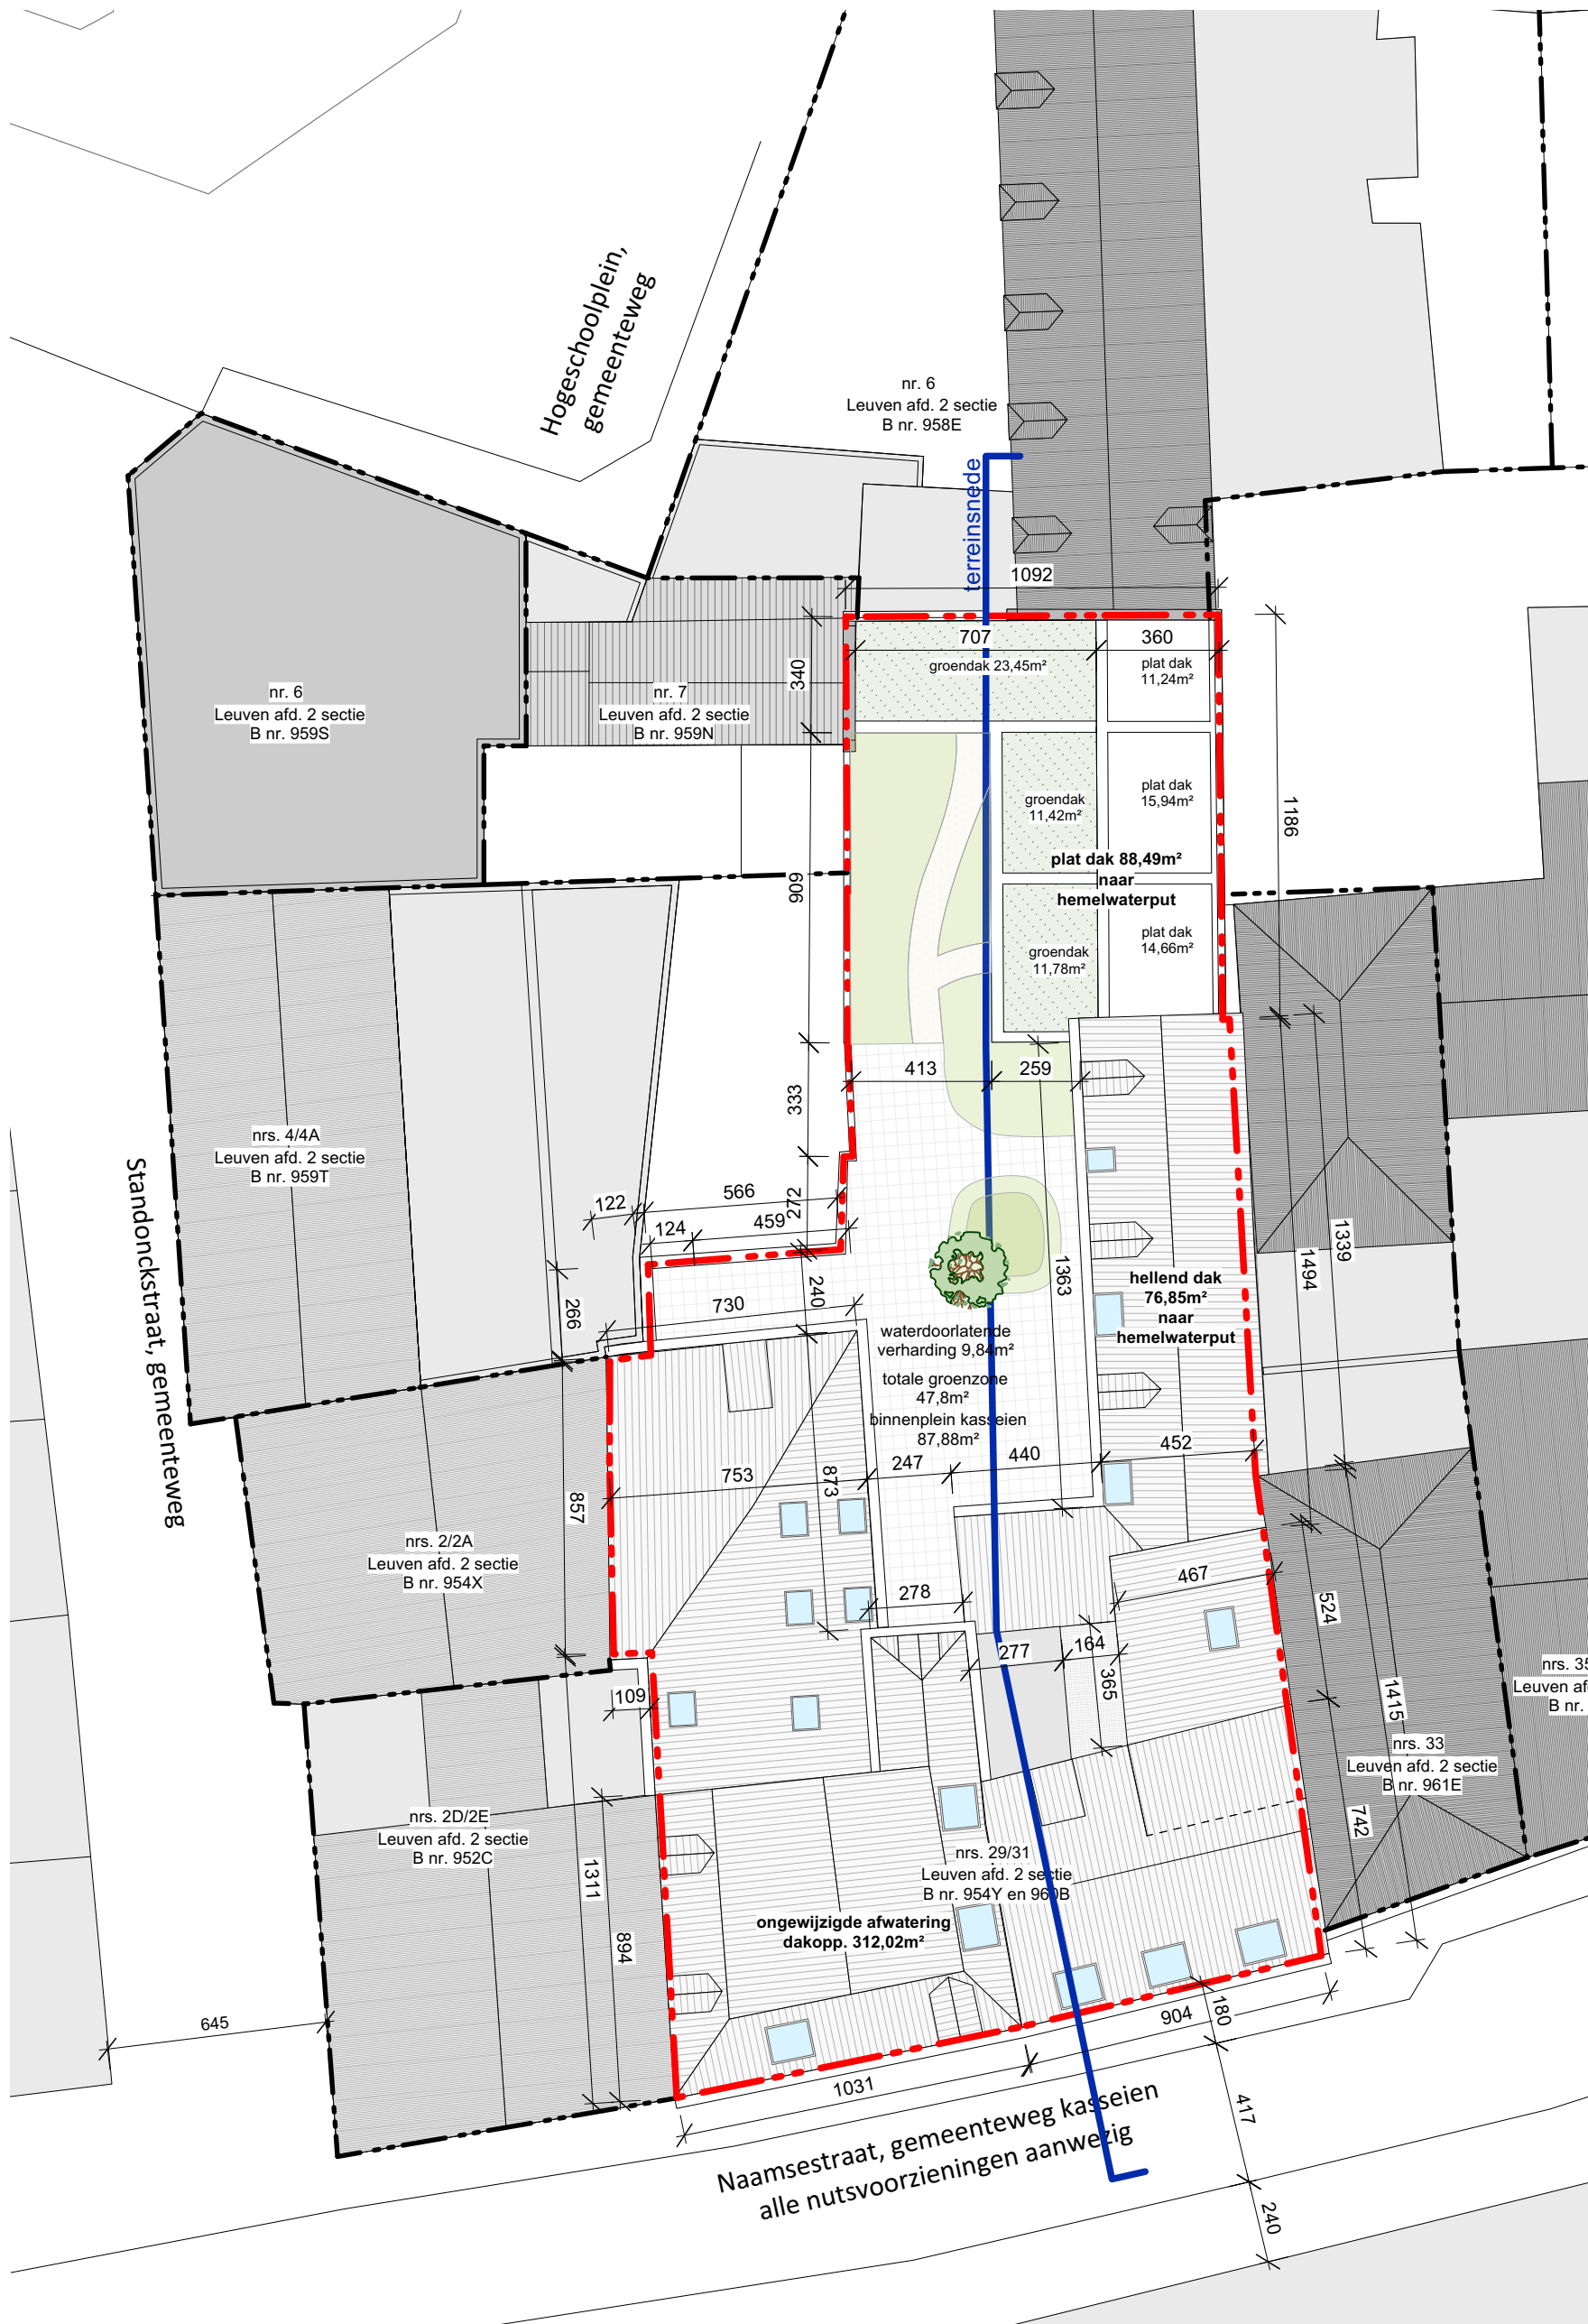

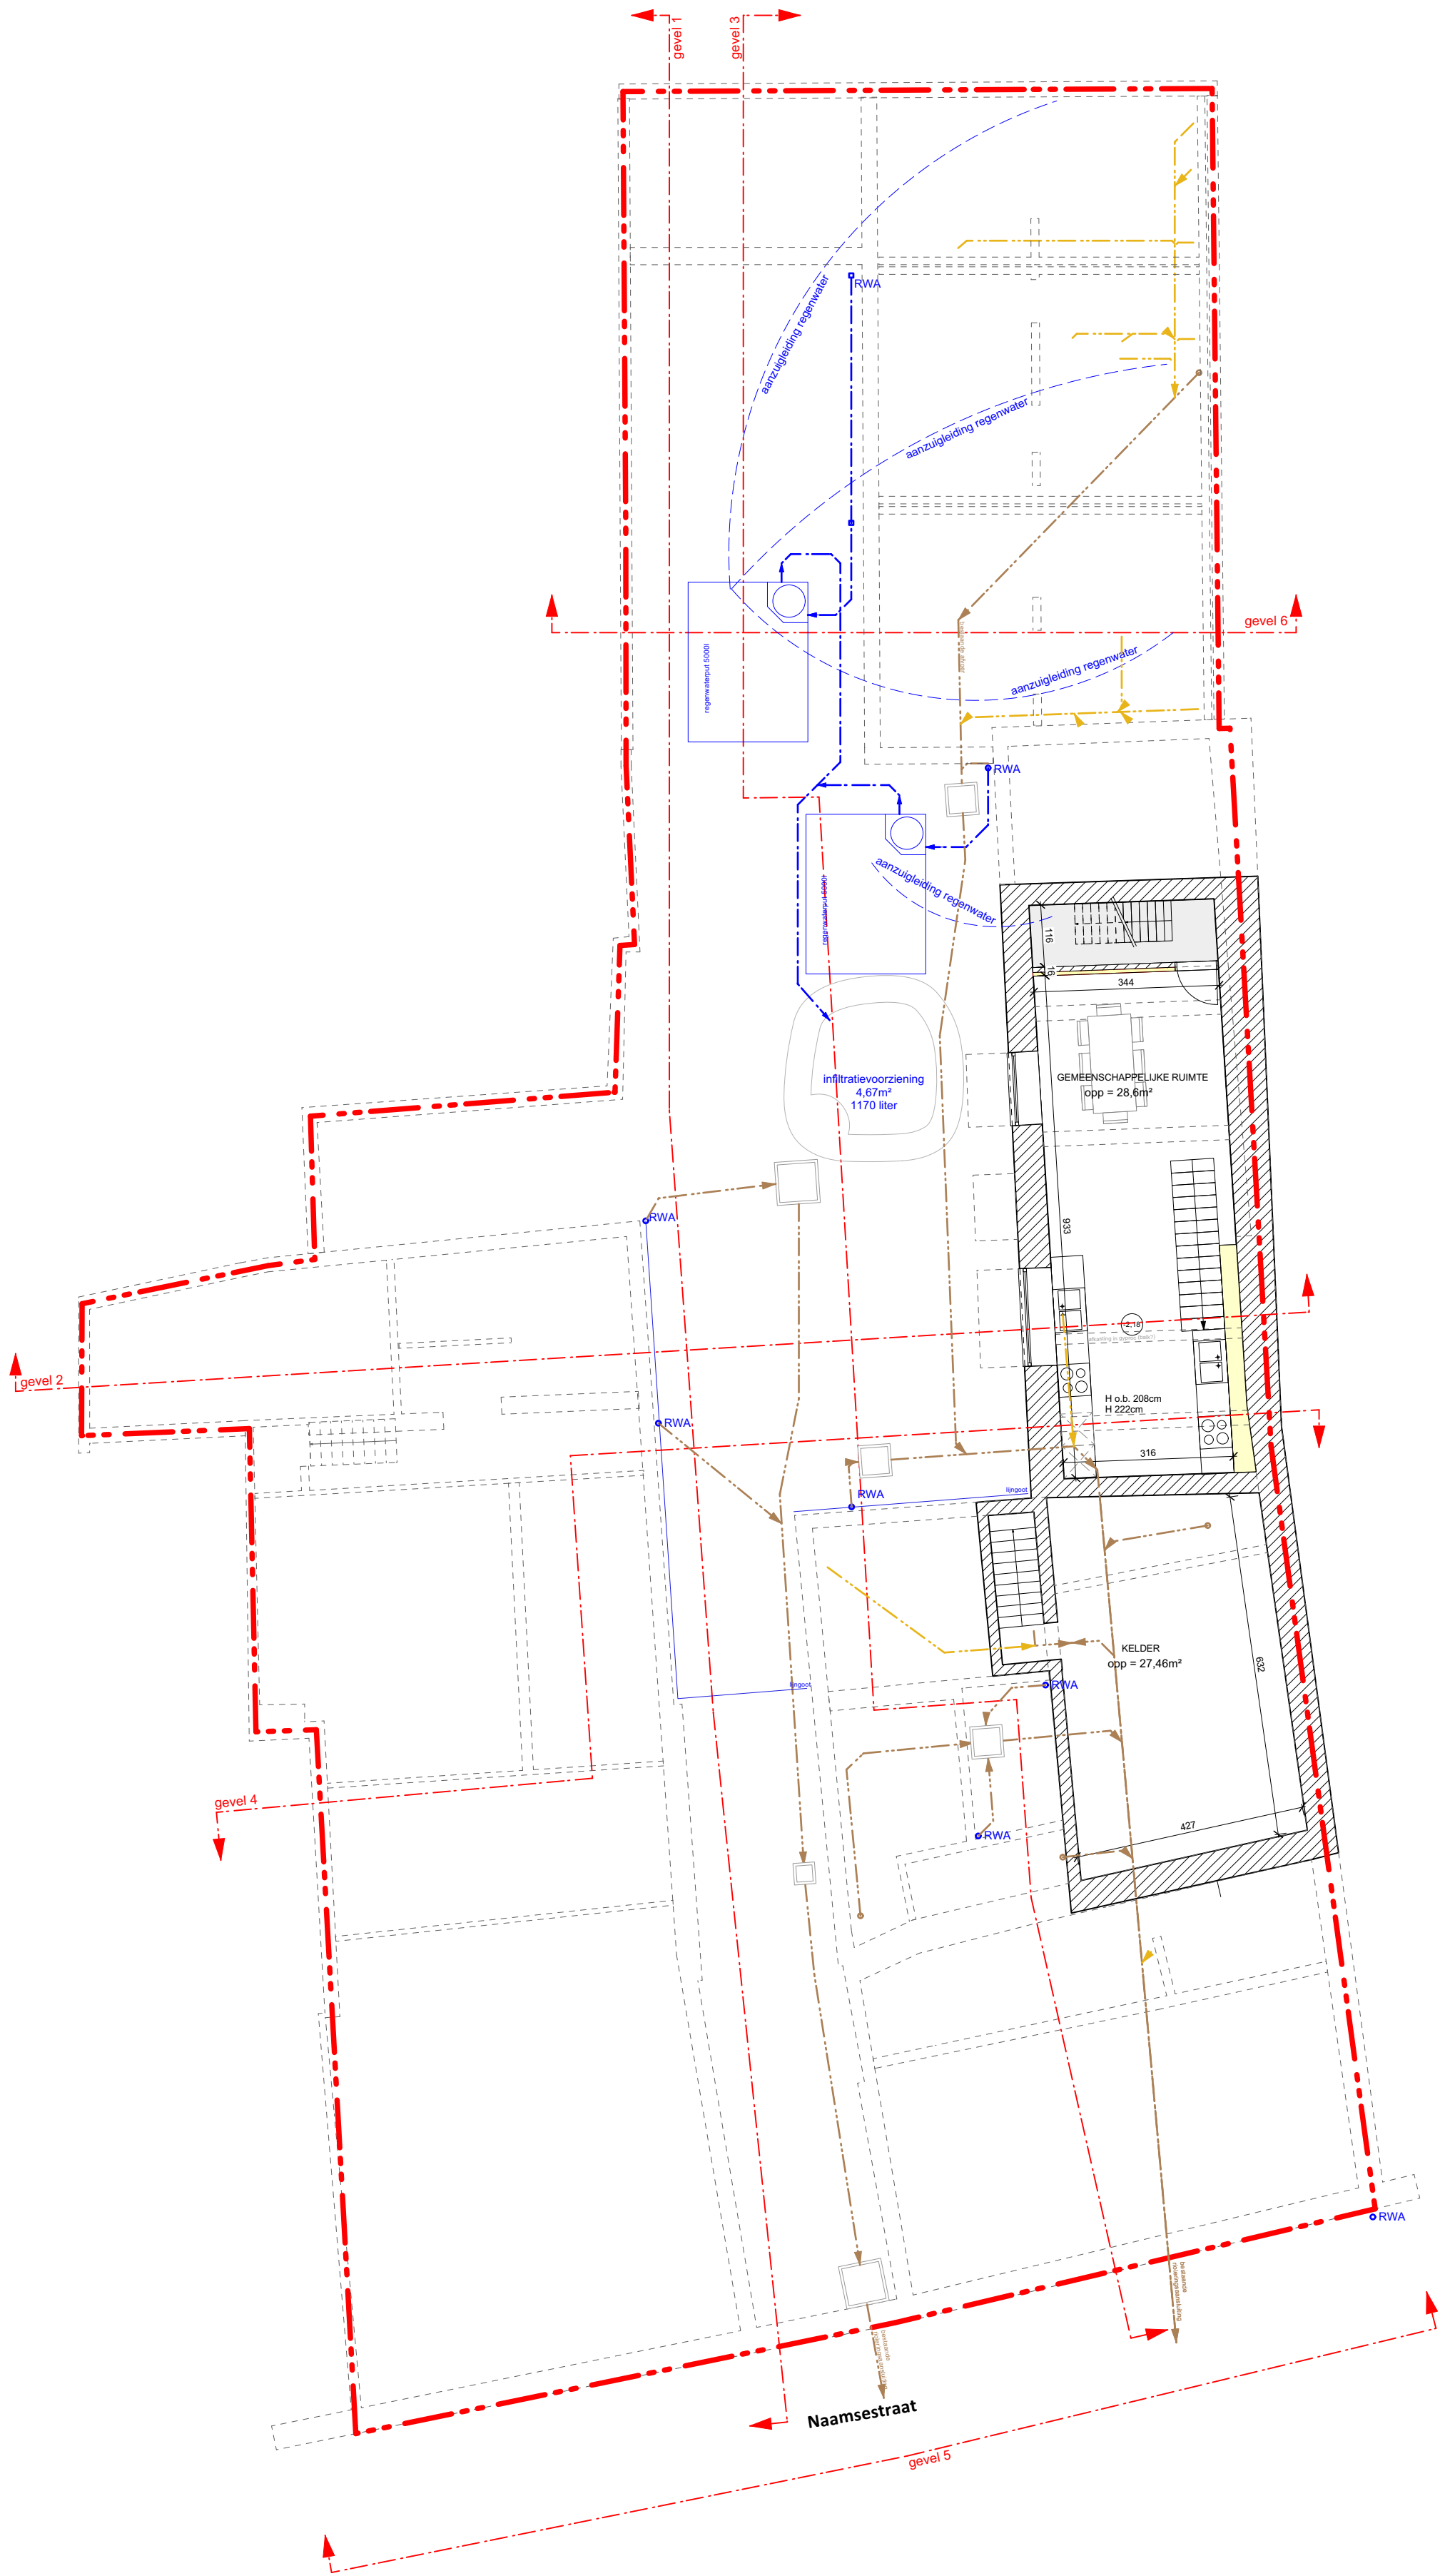

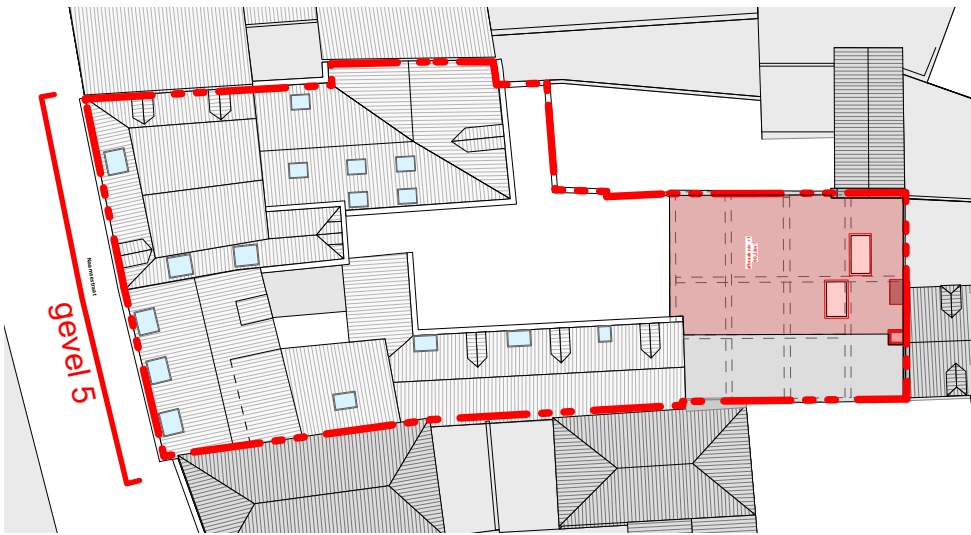



NAAMSESTRAAT 29
VOORGEVEL - GEVEL 5
bestaande toestand


0 1 5


1:100

26/01/2024
BA_NAAMSE 29-31_G_8_04



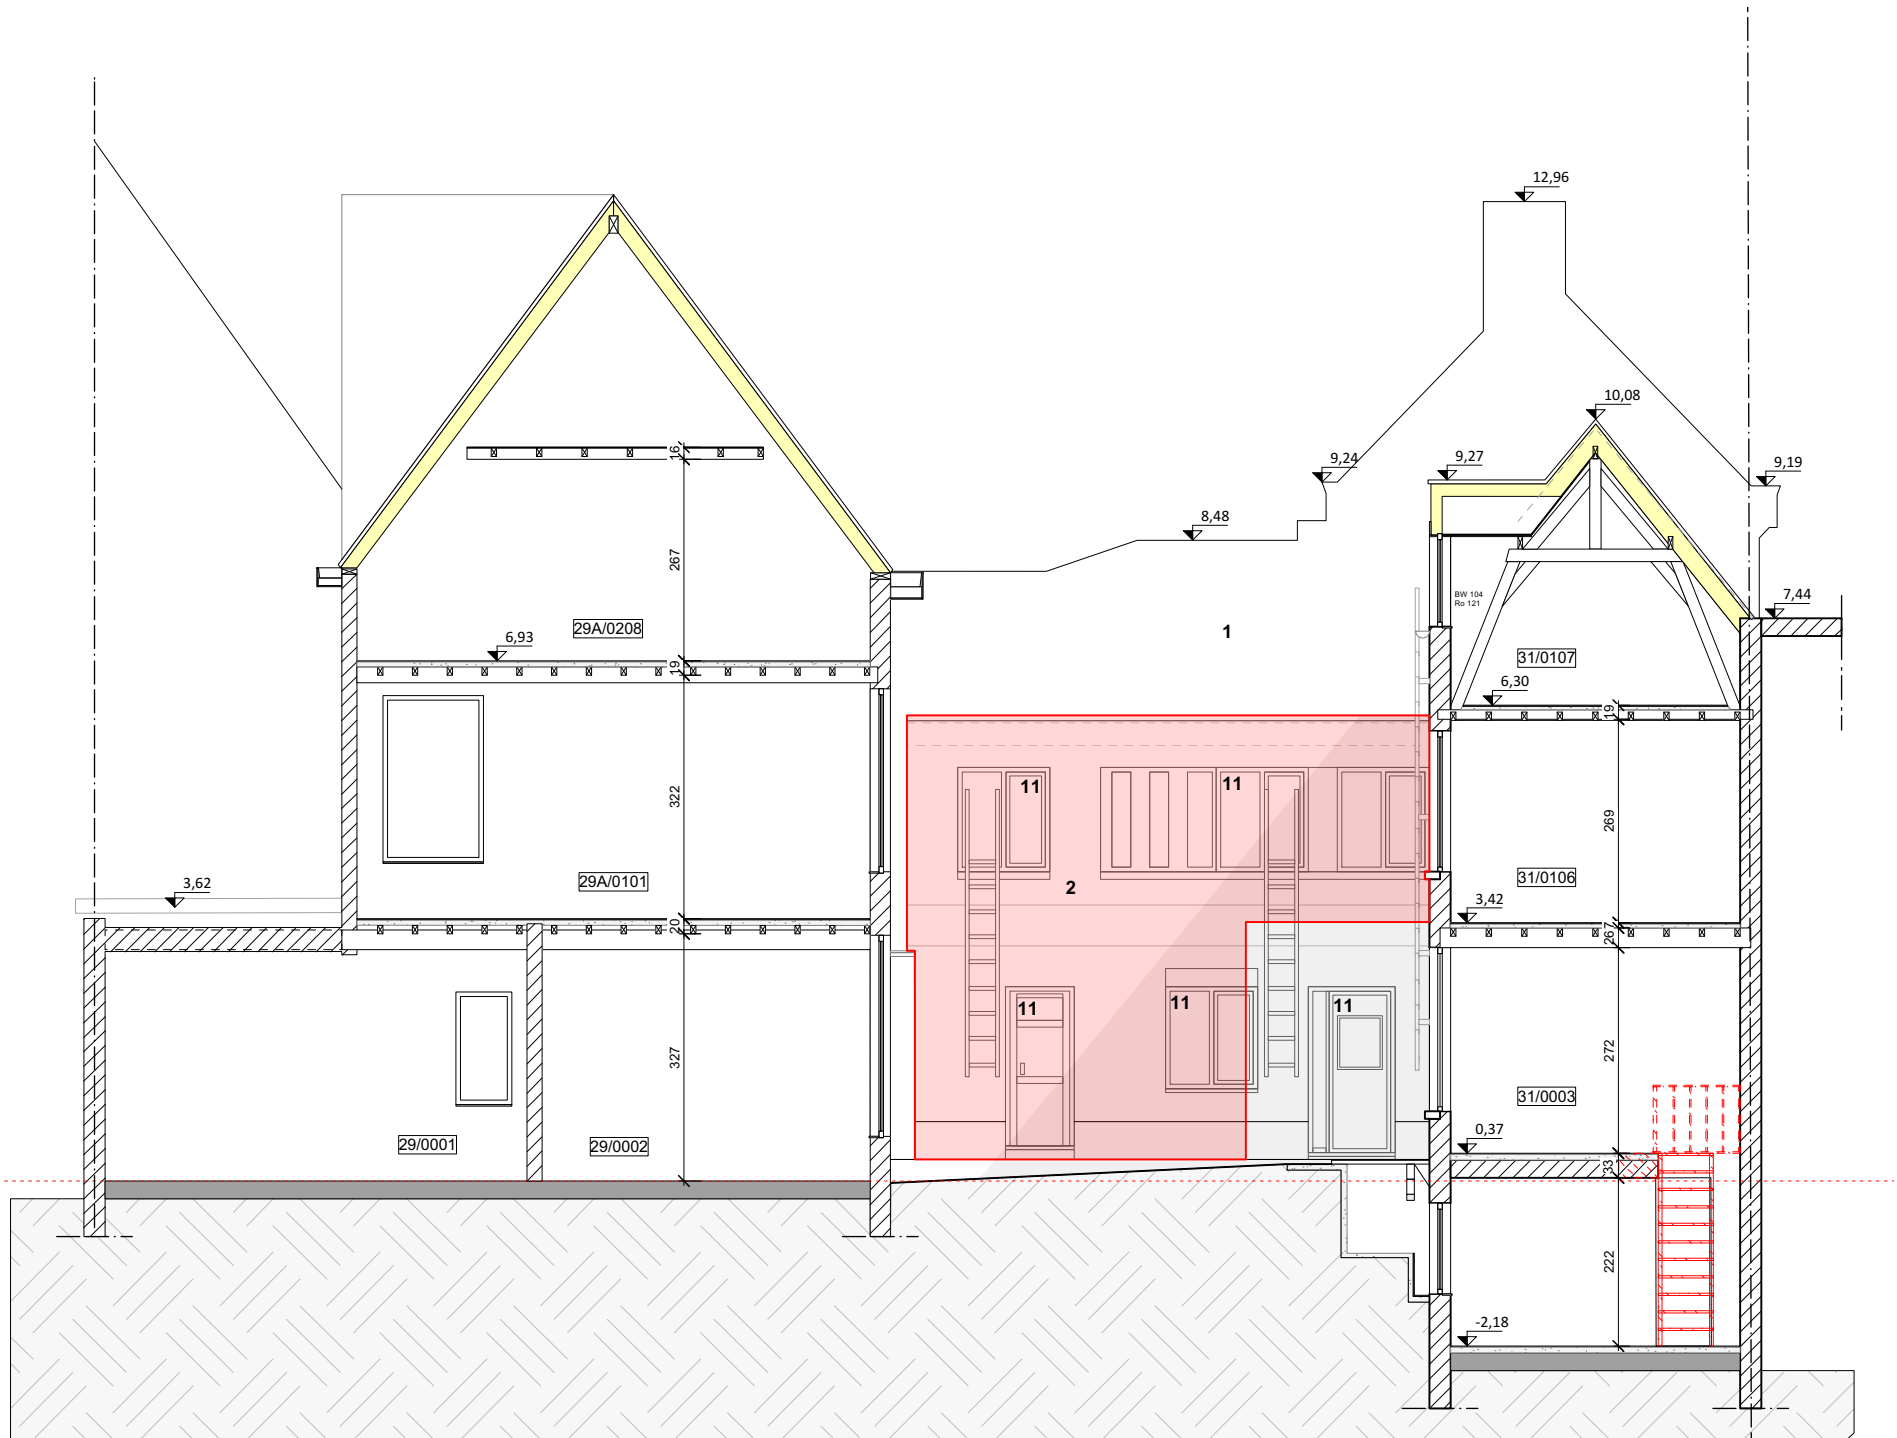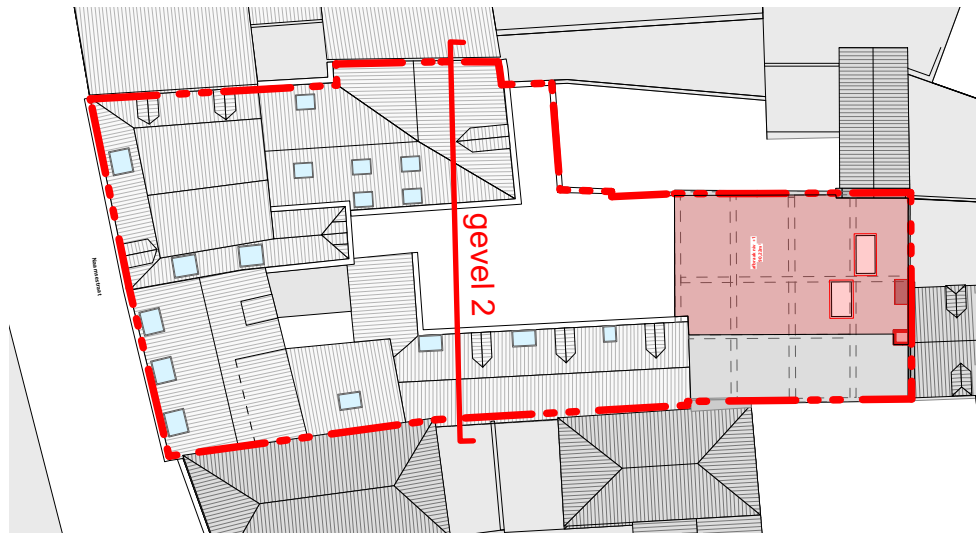

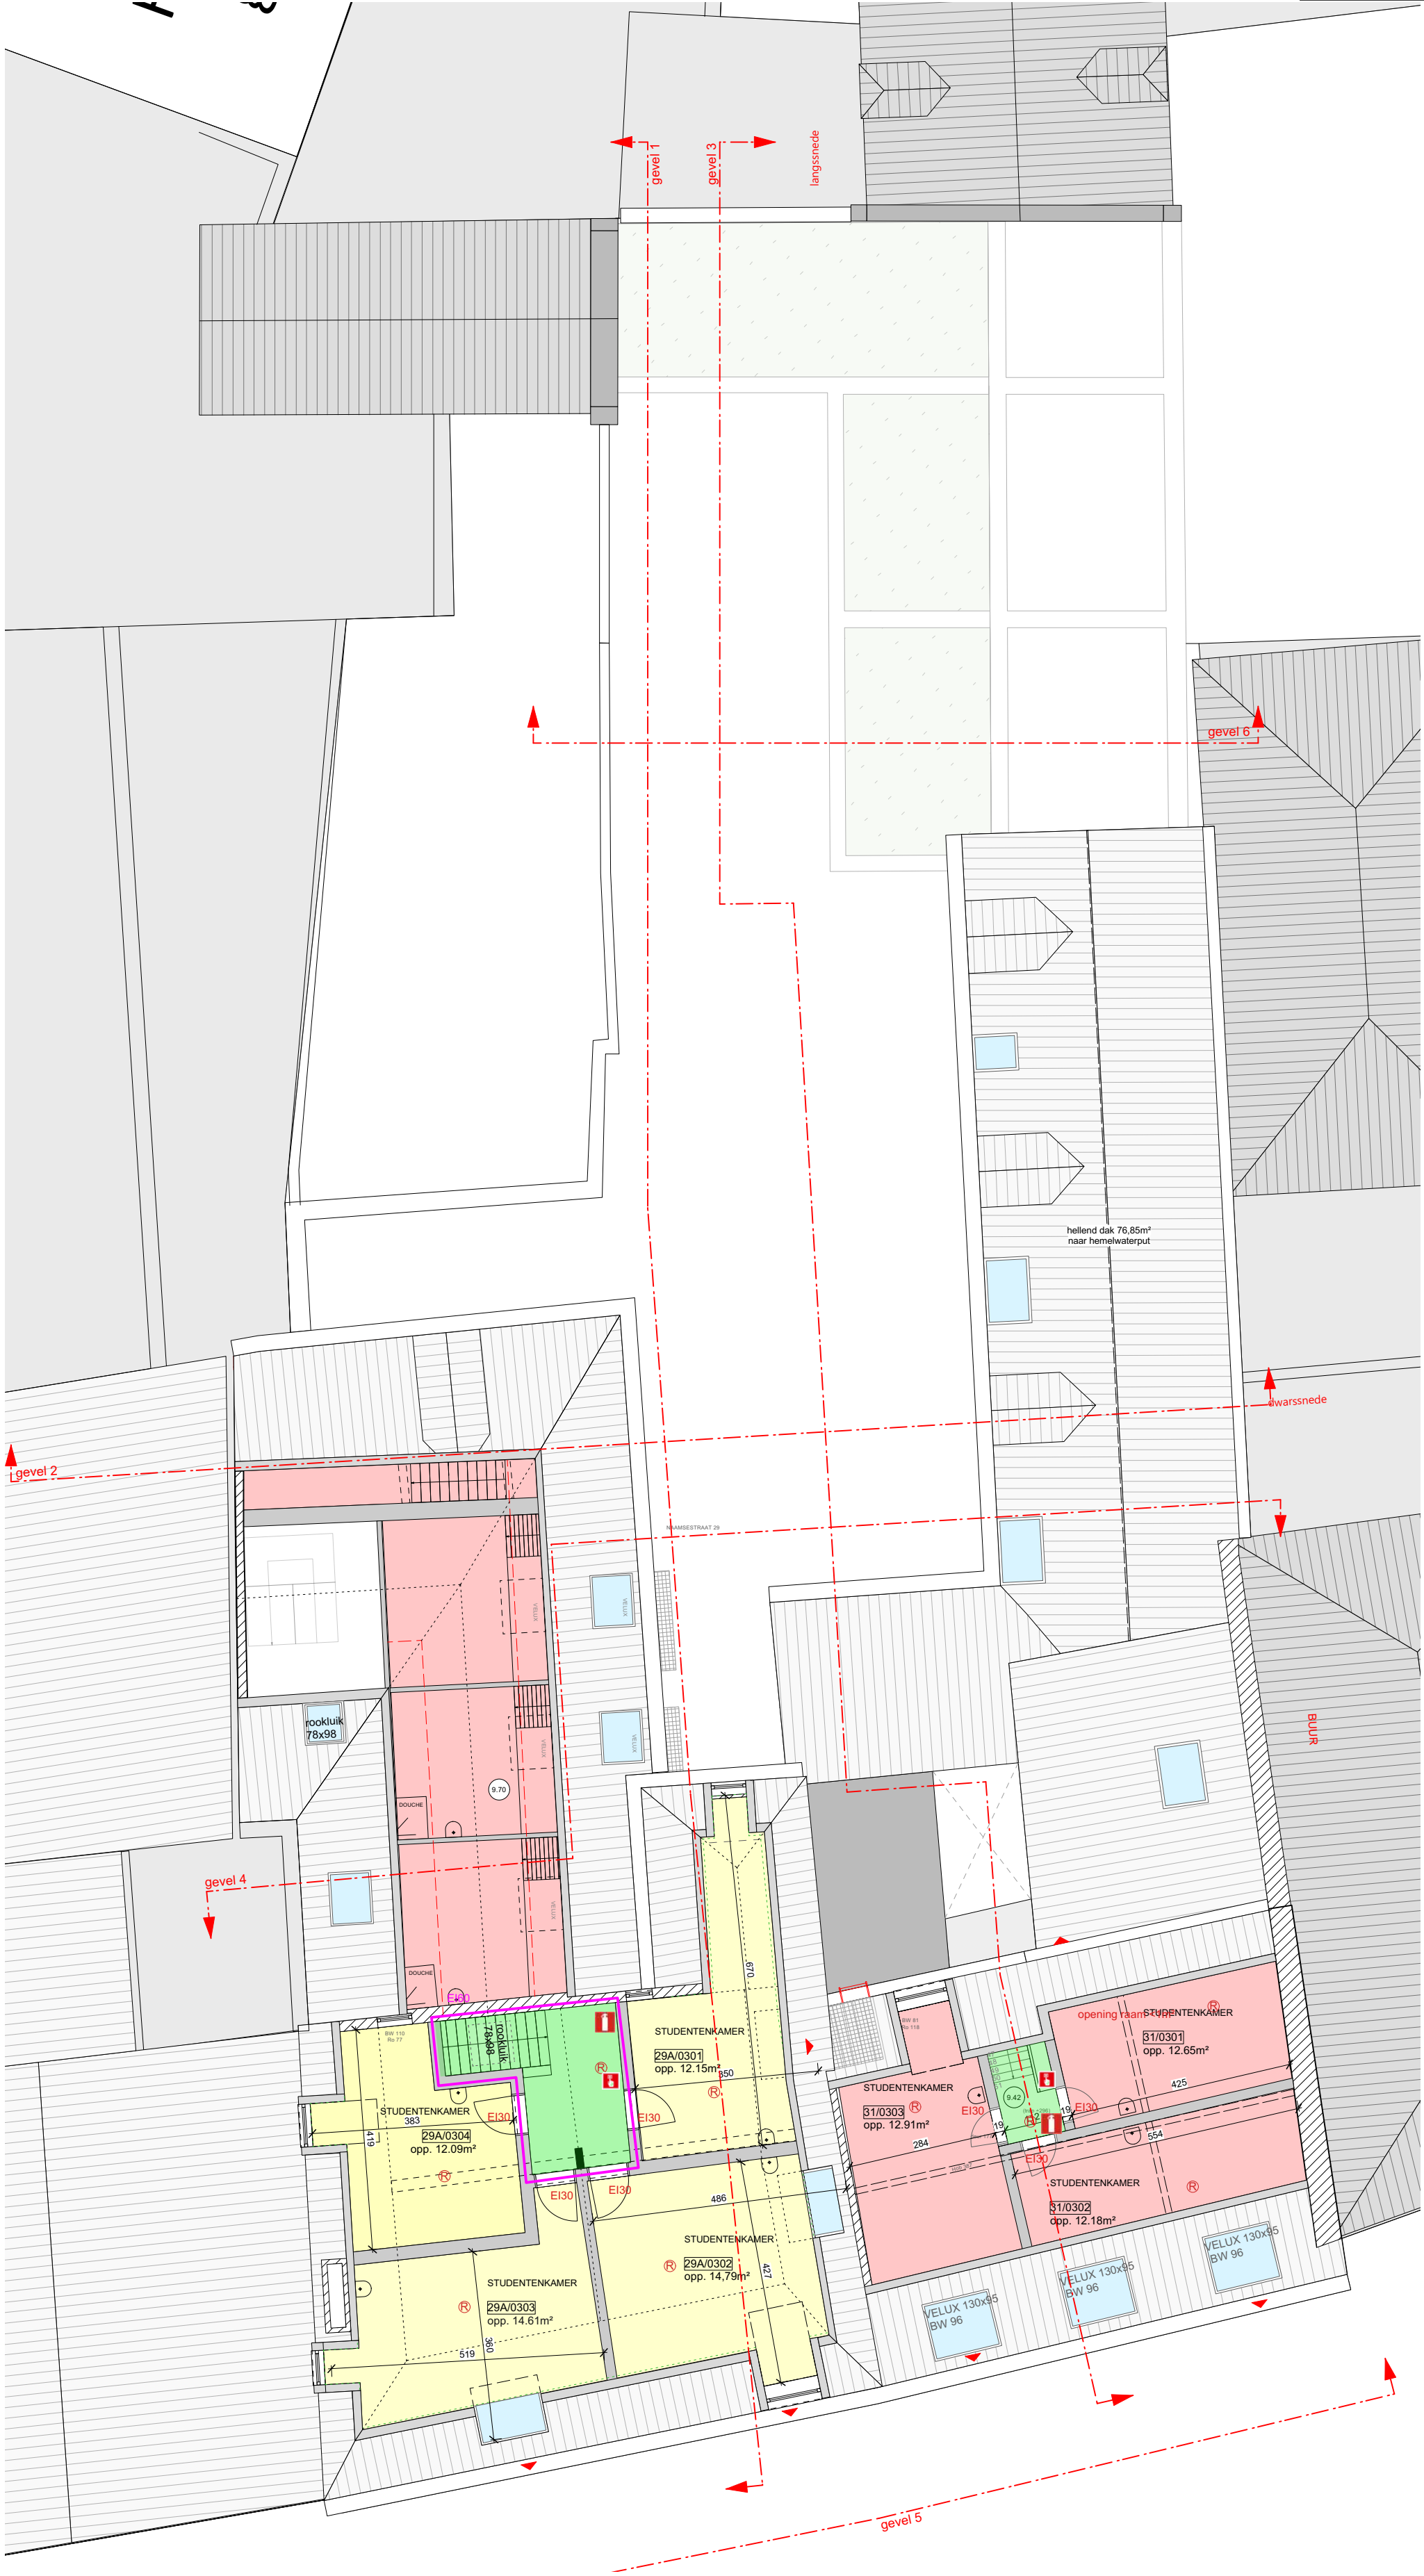

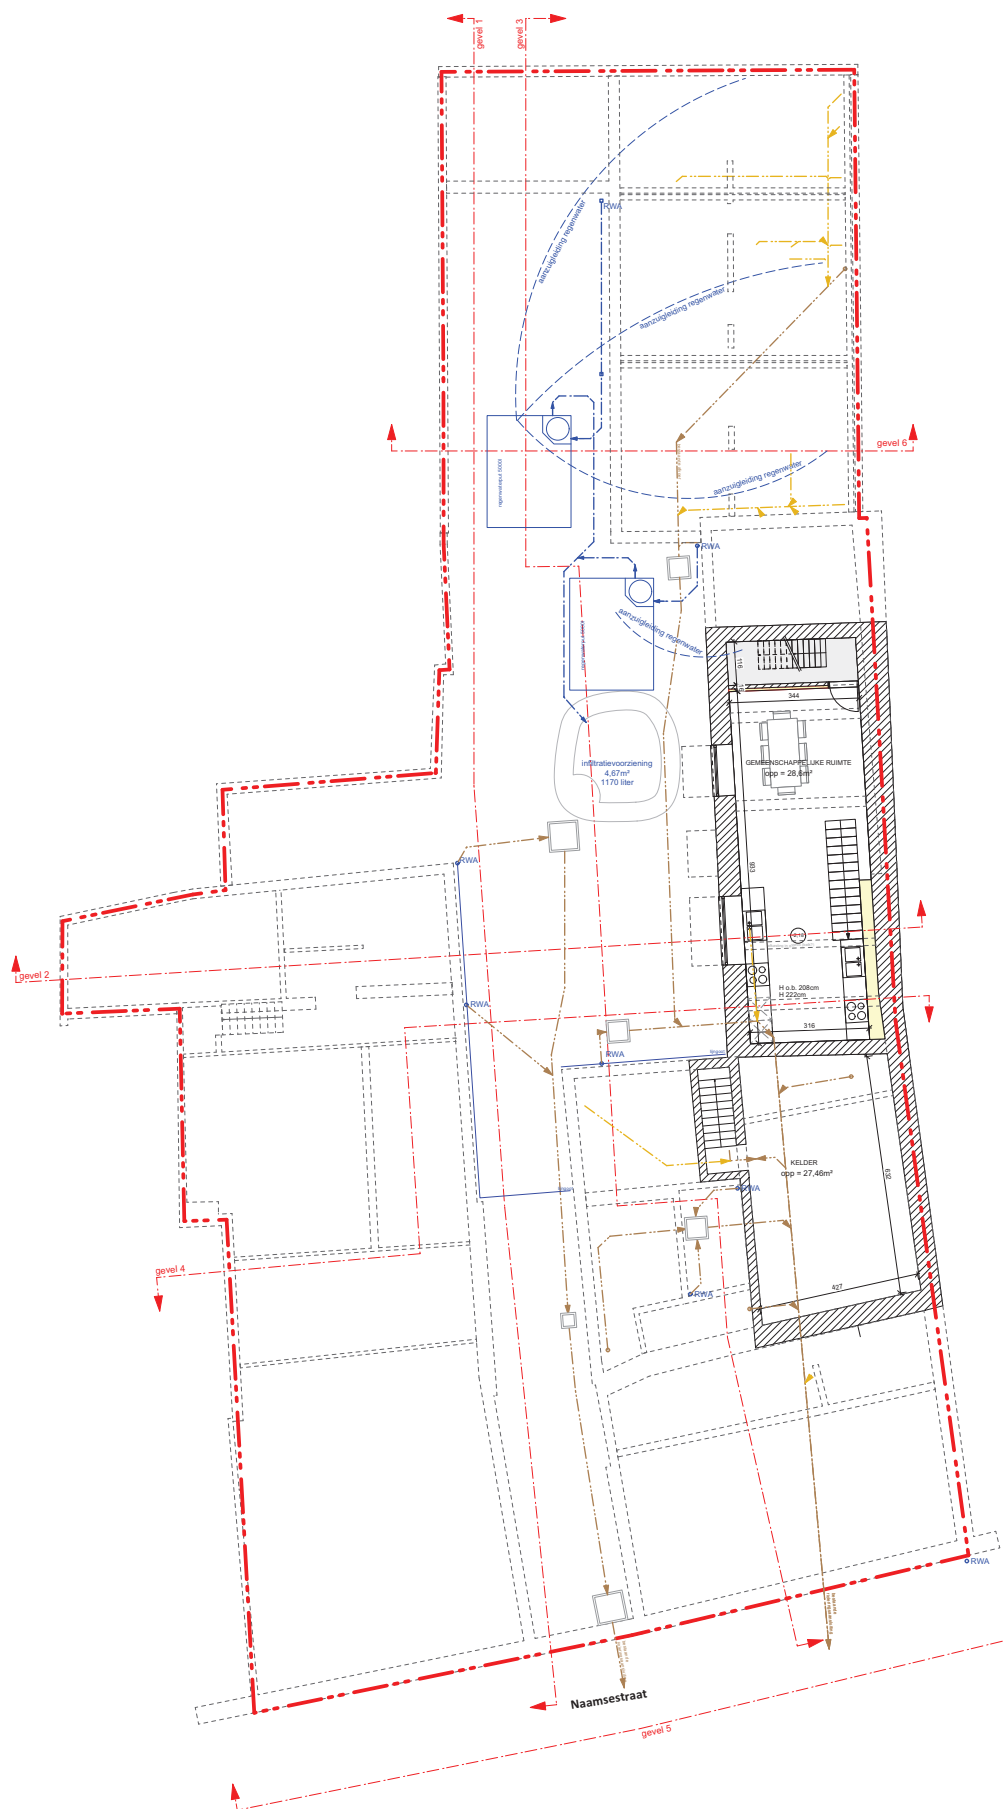

nummering_OMV_2024130246

Dit plan is een bijlage bij het advies van dienst data en gis dat werd uitgebracht in functie van het toekennen van adressen binnen deze aanvraag tot omgevingsvergunning.

Het betreft dus geen vergund plan.


T'JONCK/NILIS
INGENIEUR-ARCHITECTEN

Eraam Ruilensveld 83/002
3031 Hervebeke
T: +32 16 13 45 48

NAAMSESTRAAT 29
GRONDPLAN GELUKVLOERS
nieuw toestand

0 1 5
1:100

26/01/2024
BA_NAAMSE 29-31_P_N_02

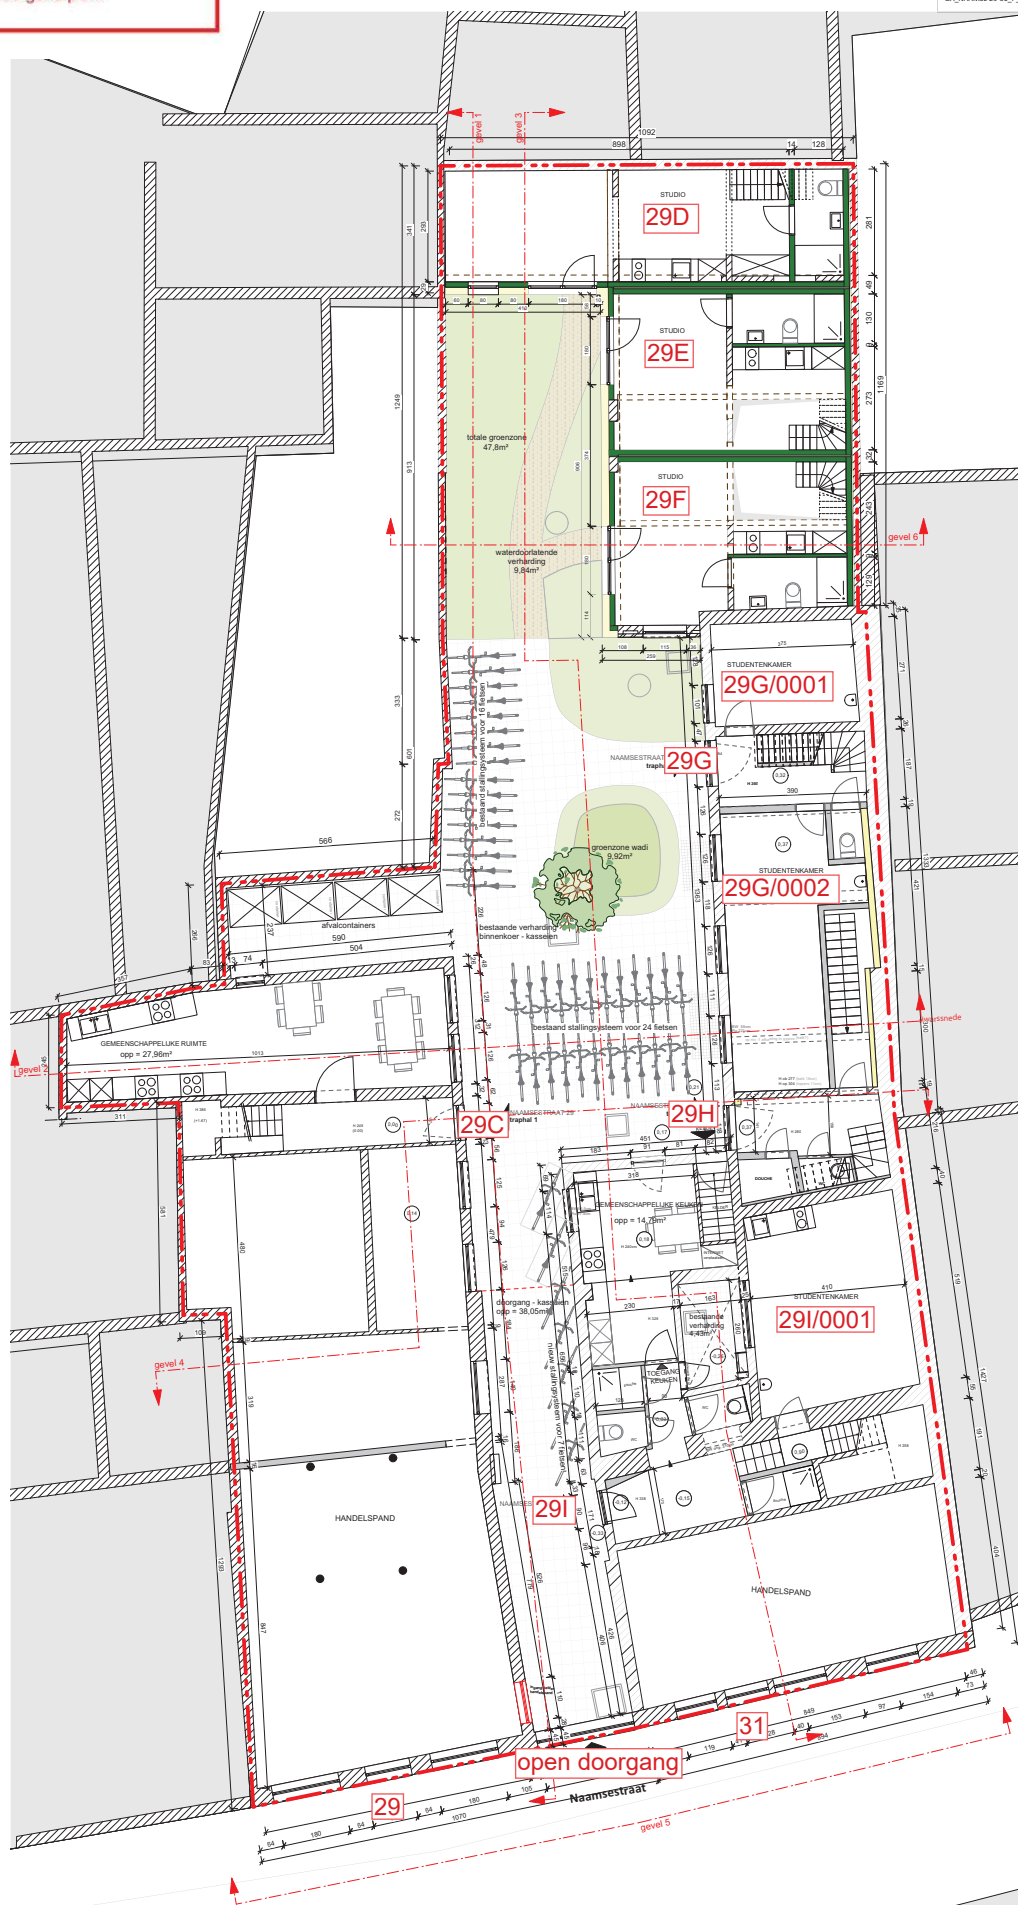

nummering_OMV_ 2024130246

Dit plan is een bijlage bij het advies van dienst data en gis dat werd uitgebracht in functie van het toekennen van adressen binnen deze aanvraag tot omgevingsvergunning.


Het betreft dus geen vergund plan.


T'JONCK/NILIS
INGENIEUR-ARCHITECTEN


Erasmus Ruilenroest 83/002
30021 Hoveville
T: +32 16 23 45 48

NAAMSESTRAAT 29
GRONDPLAN NIVO +1
Nieuwe toestand


0 1 2 3 4 5
1:100
26/01/2024
BA_NAAMSE 29-31_P_N_03

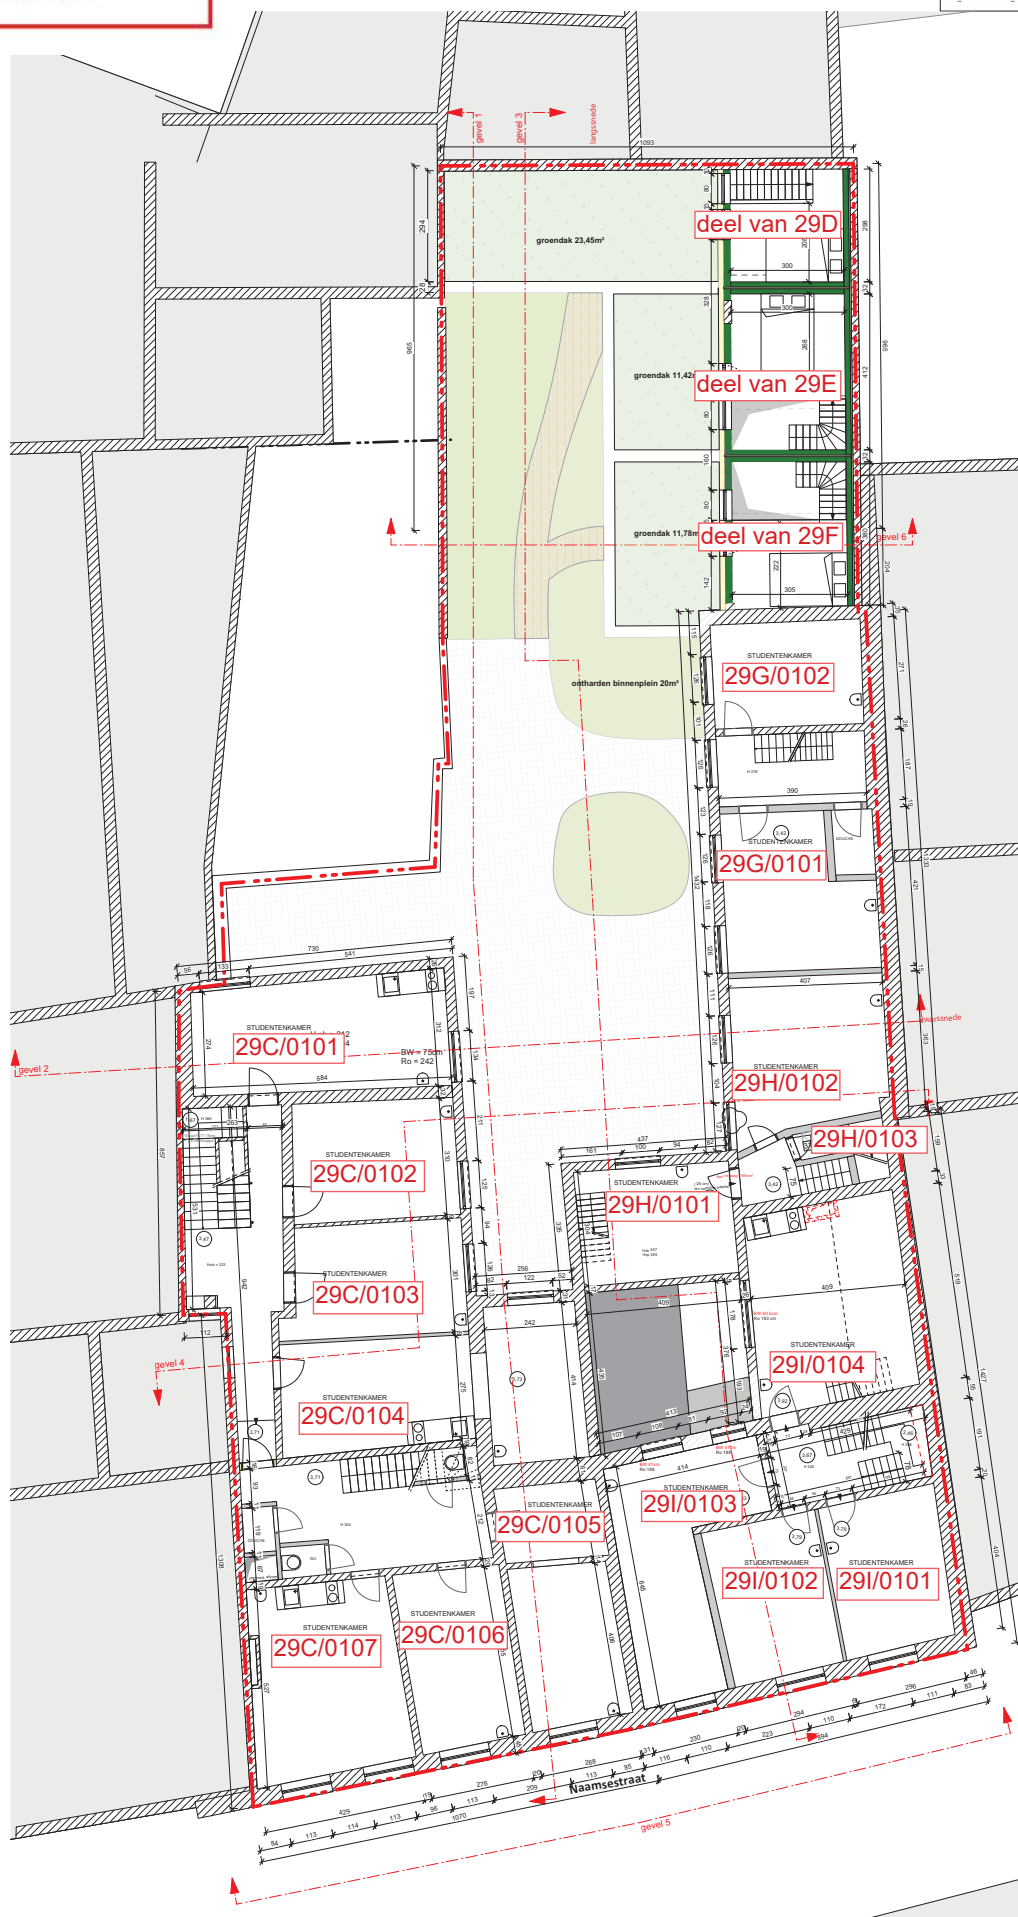

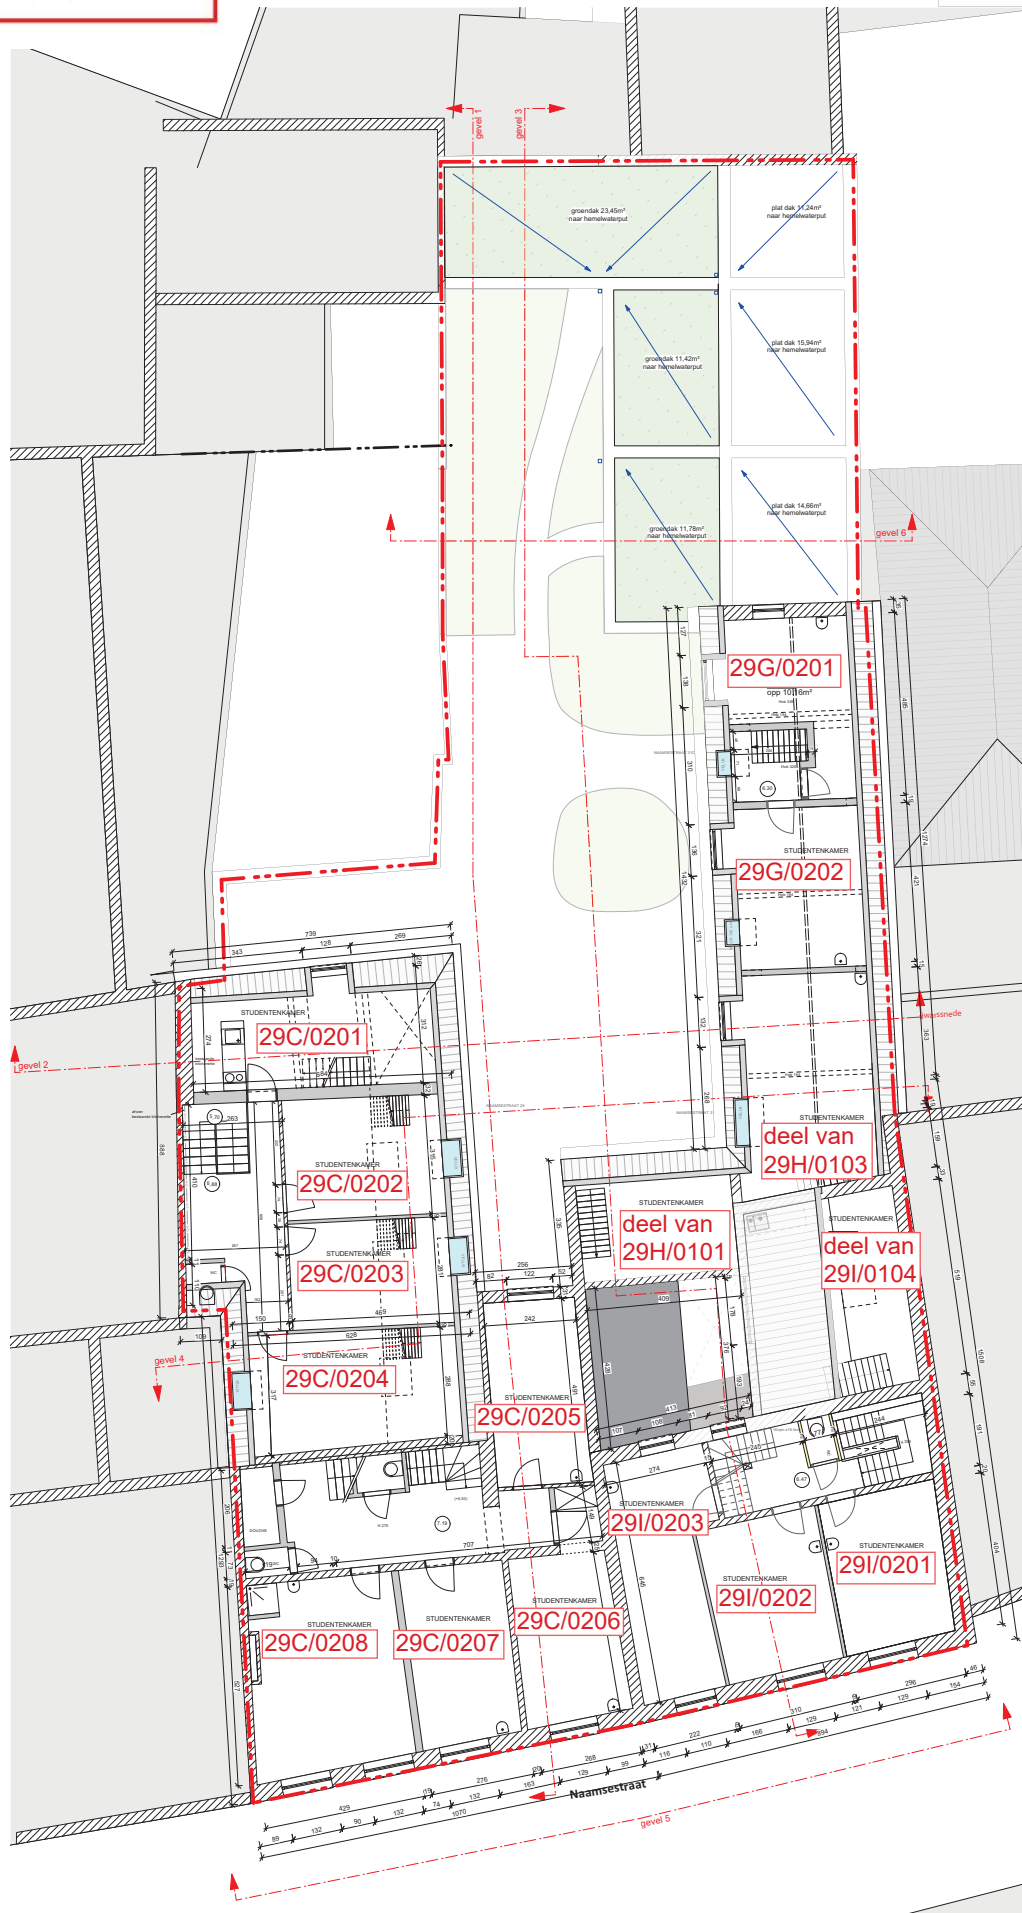

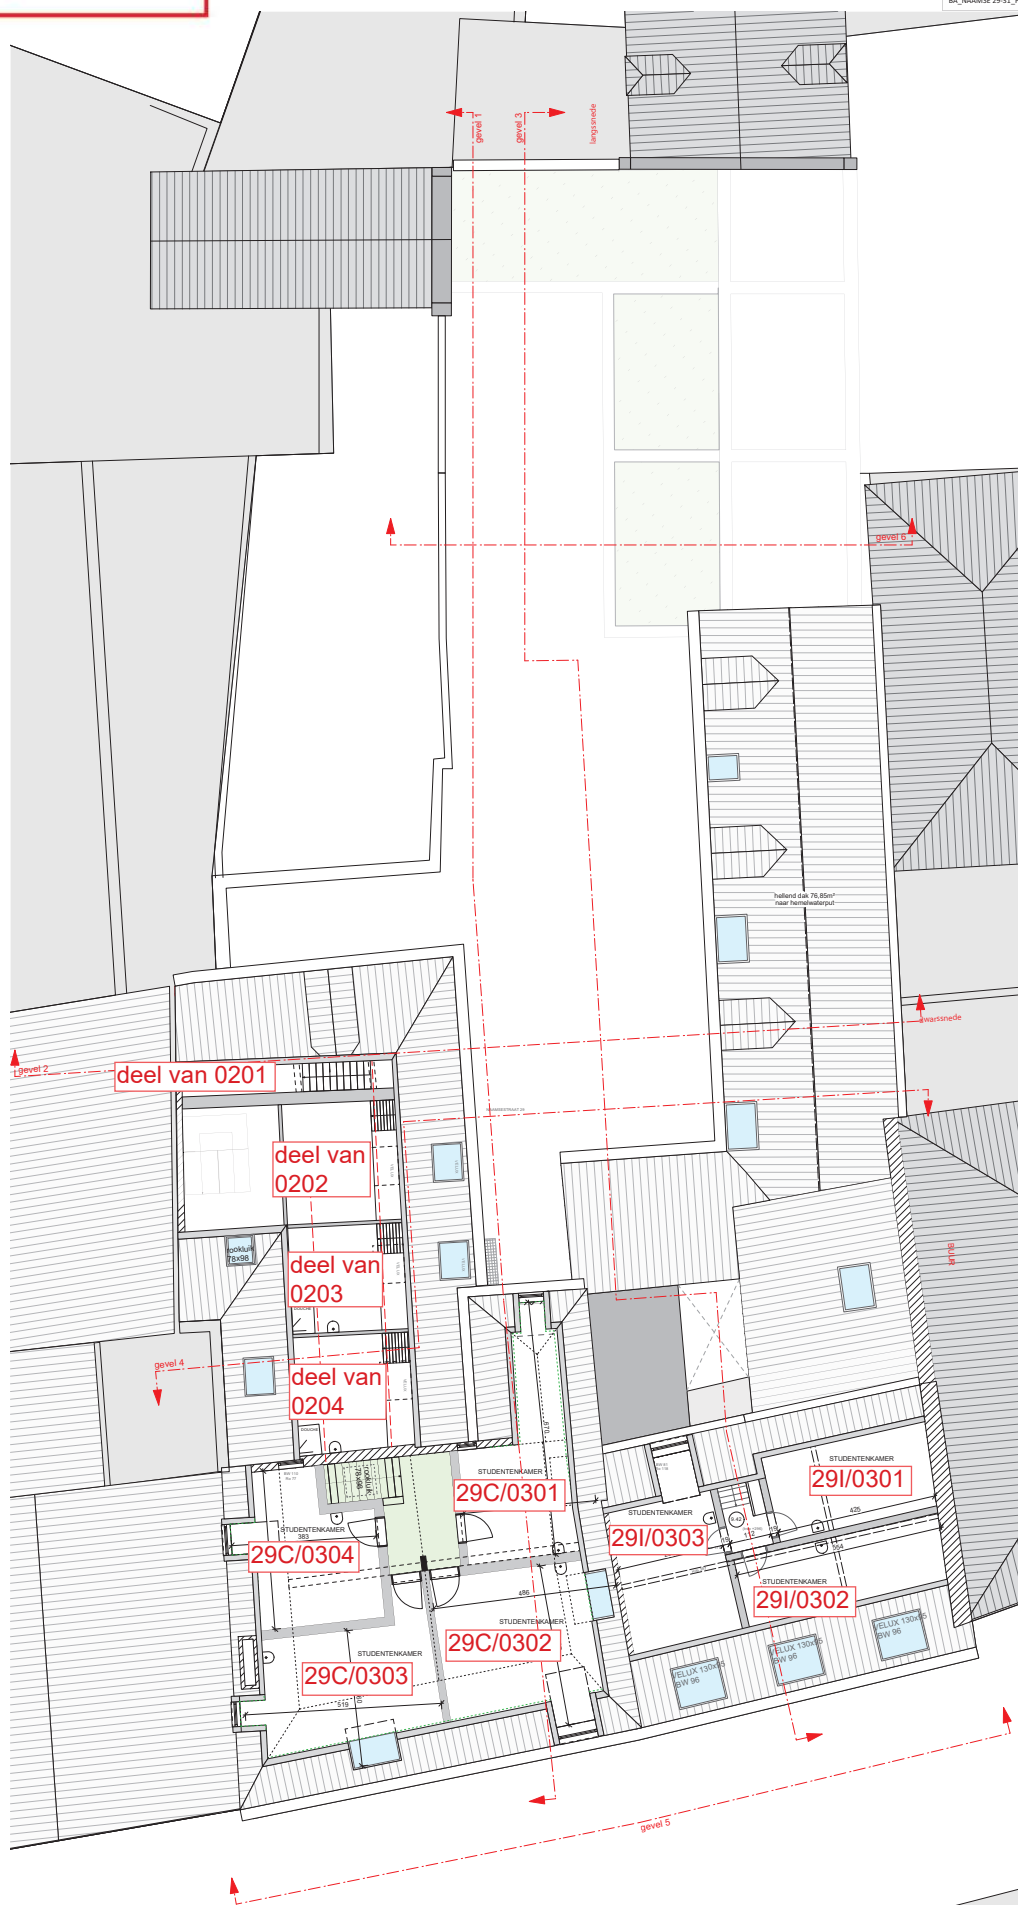



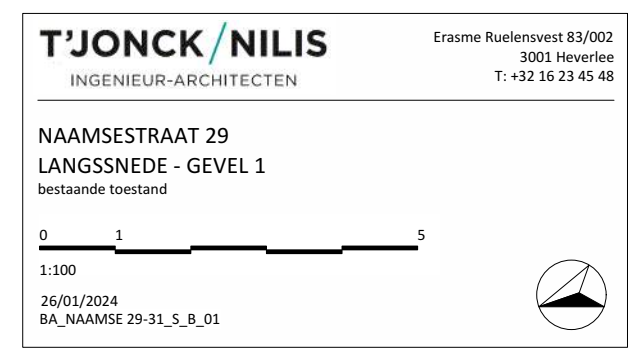



Dit plan is een bijlage bij het advies van de dienst wonen dat werd uitgebracht in functie van de woonkwaliteit binnen deze aanvraag tot omgevingsvergunning.

Het betreft dus geen vergund plan.


Dit plan is een bijlage bij het advies van de dienst wonen dat werd uitgebracht in functie van de woonkwaliteit binnen deze aanvraag tot omgevingsvergunning.


Het betreft dus geen vergund plan.

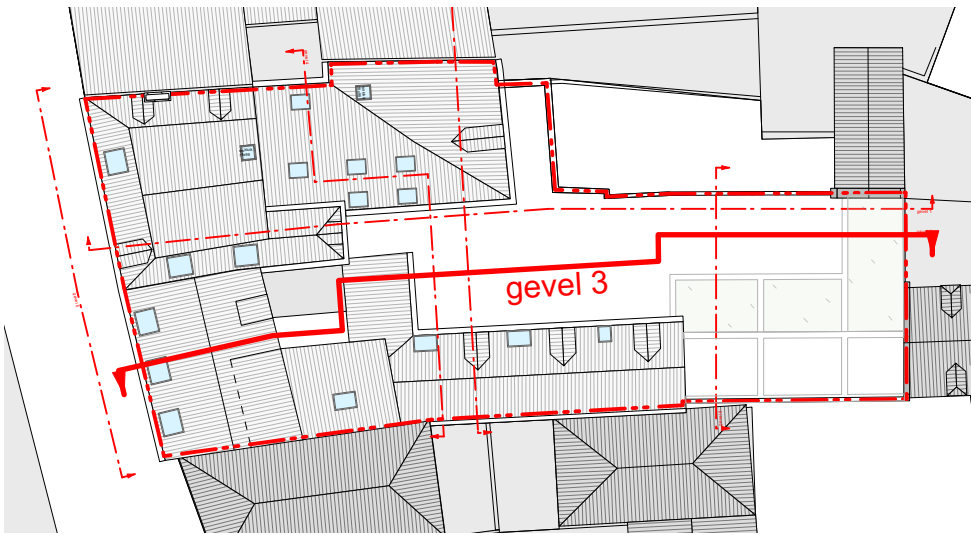

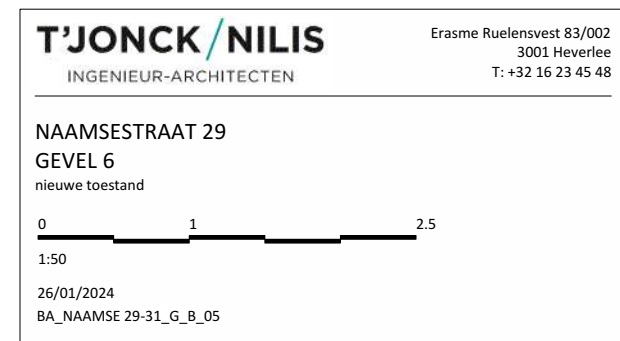

Het betreft dus geen vergund plan.

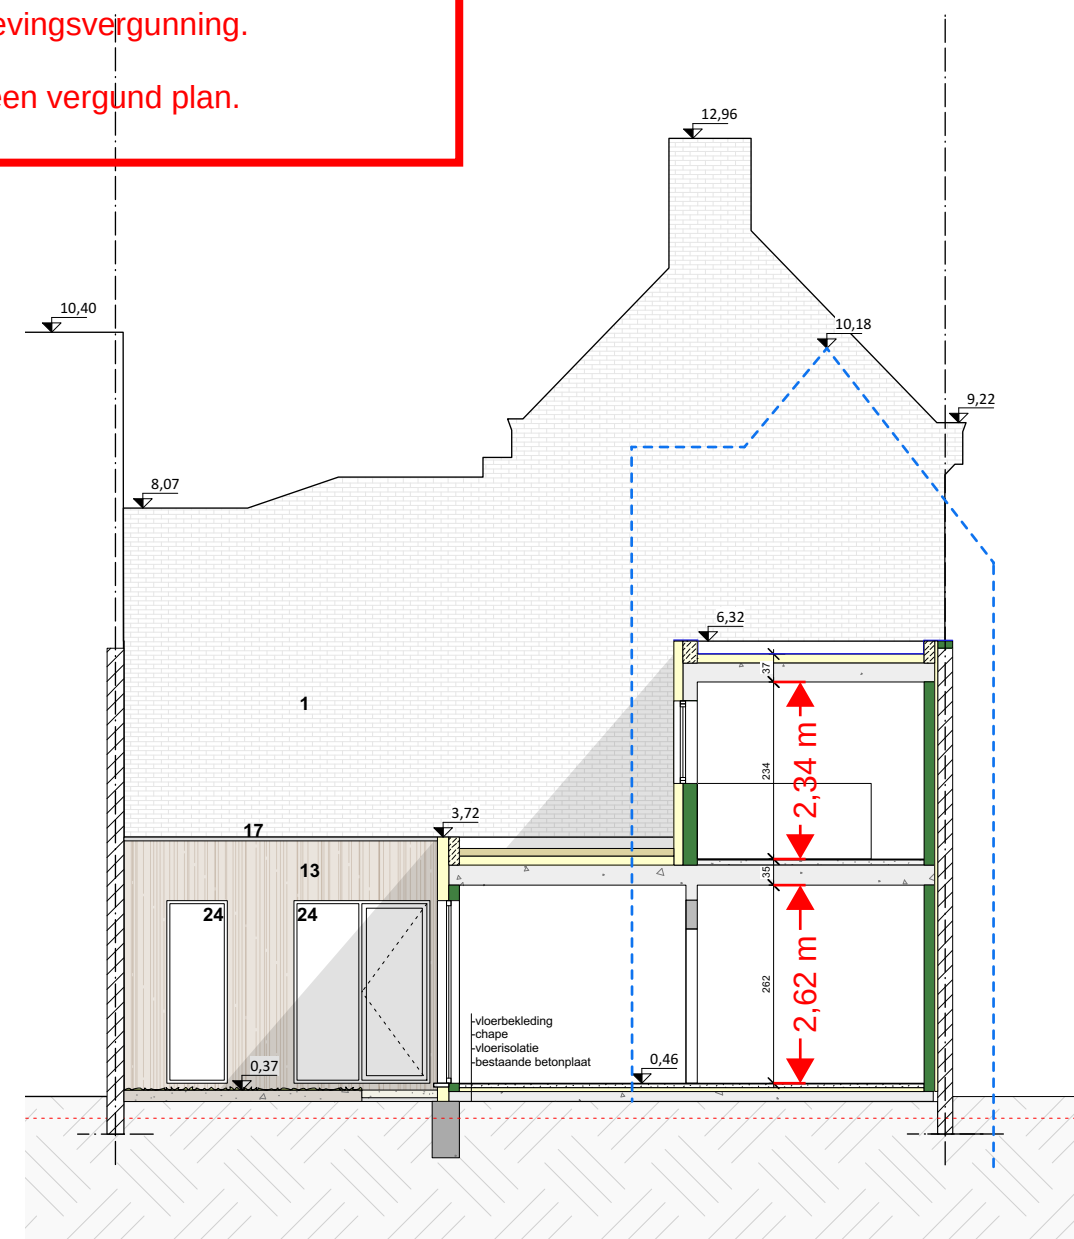

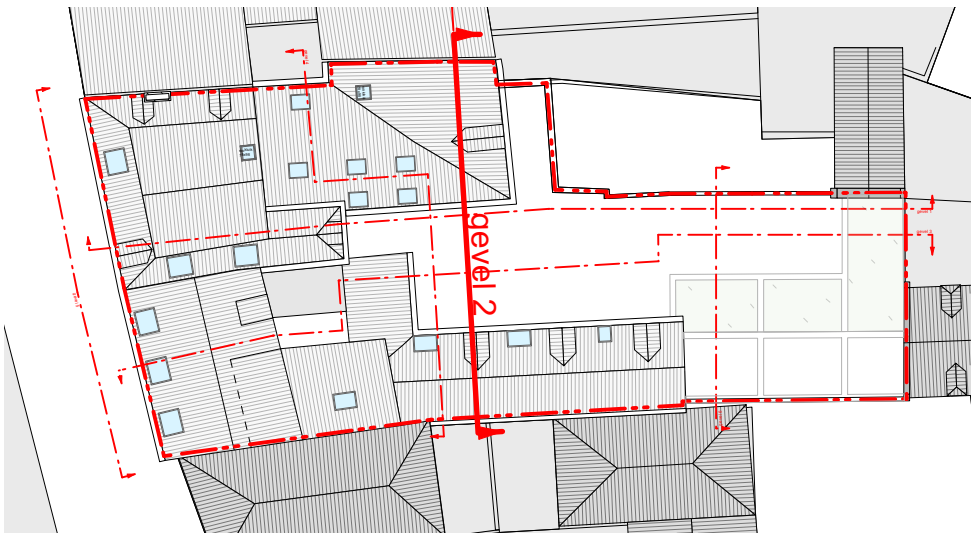



T'JONCK / NILIS
INGENIEUR-ARCHITECTEN

Erasm Ruelensvest 83/002
3001 Heverlee
T: +32 16 23 45 48

NAAMSESTRAAT 29
GEVEL ACHTERBOUW - GEVEL 2 - brandweer
nieuwe toestand

0 1 5
1:100
26/01/2024
BA_NAAMSE 29-31_G_N_01

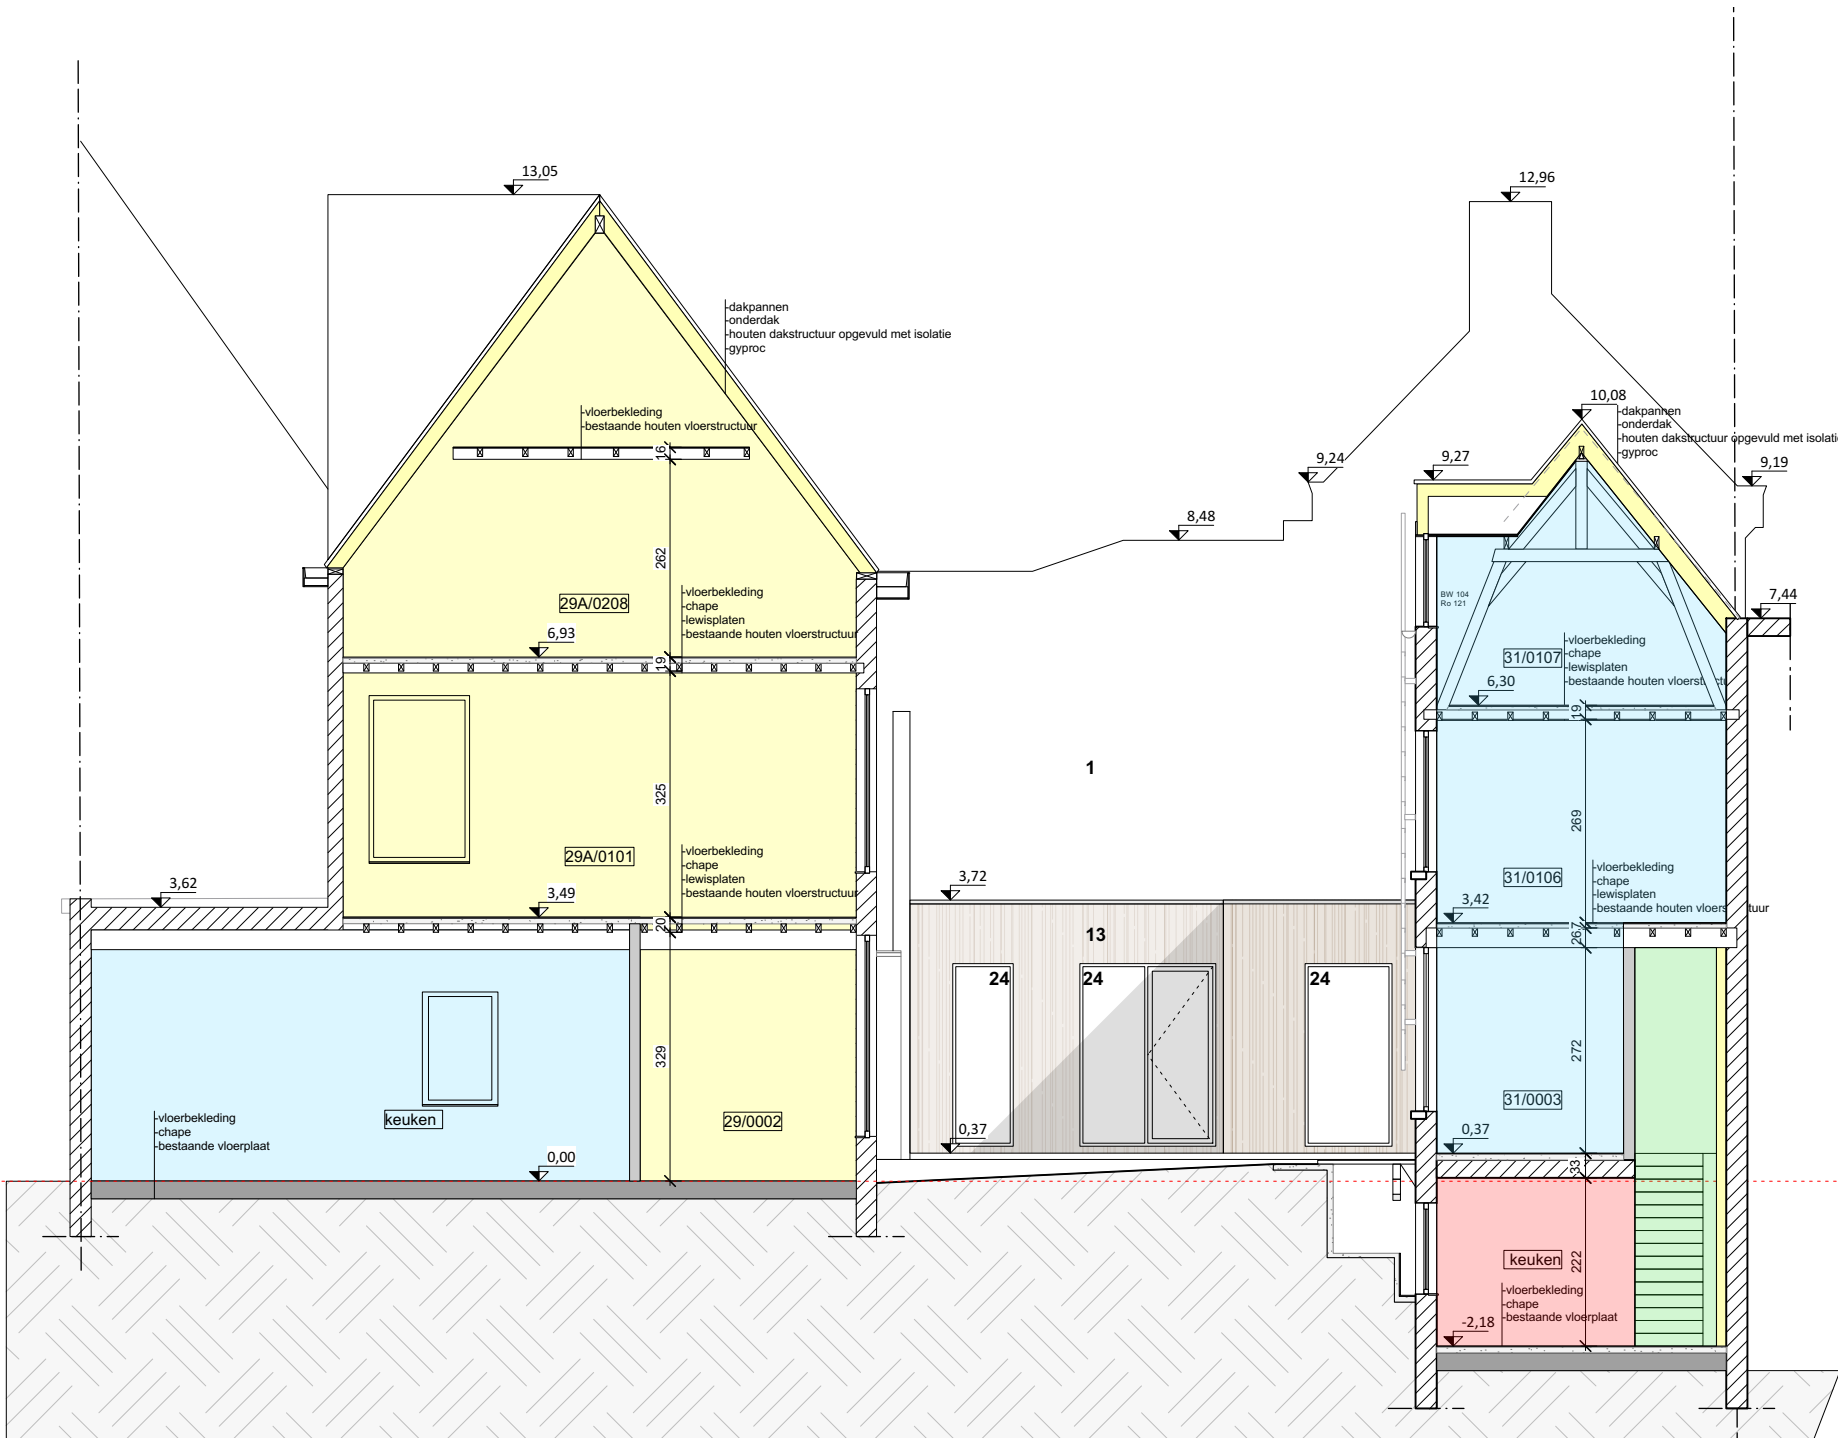

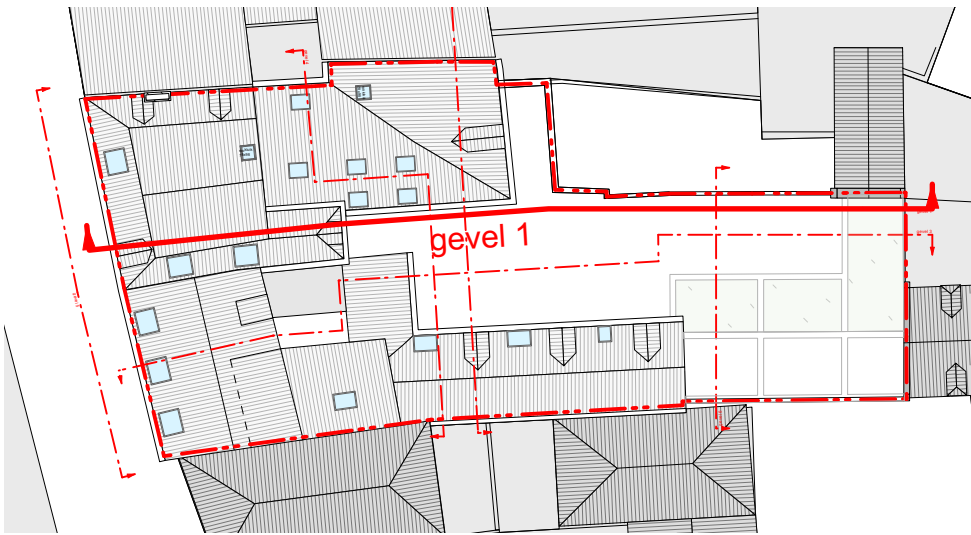


T'JONCK / NILIS
INGENIEUR-ARCHITECTEN

Erasmestraat 83/002
3001 Heverlee
T: +32 16 23 45 48

NAAMSESTRAAT 29
LANGSSNEDE - GEVEL 1 - brandweer
nieuwe toestand

0 1 5
1:100
26/01/2024
BA_NAAMSE 29-31_S_N_01

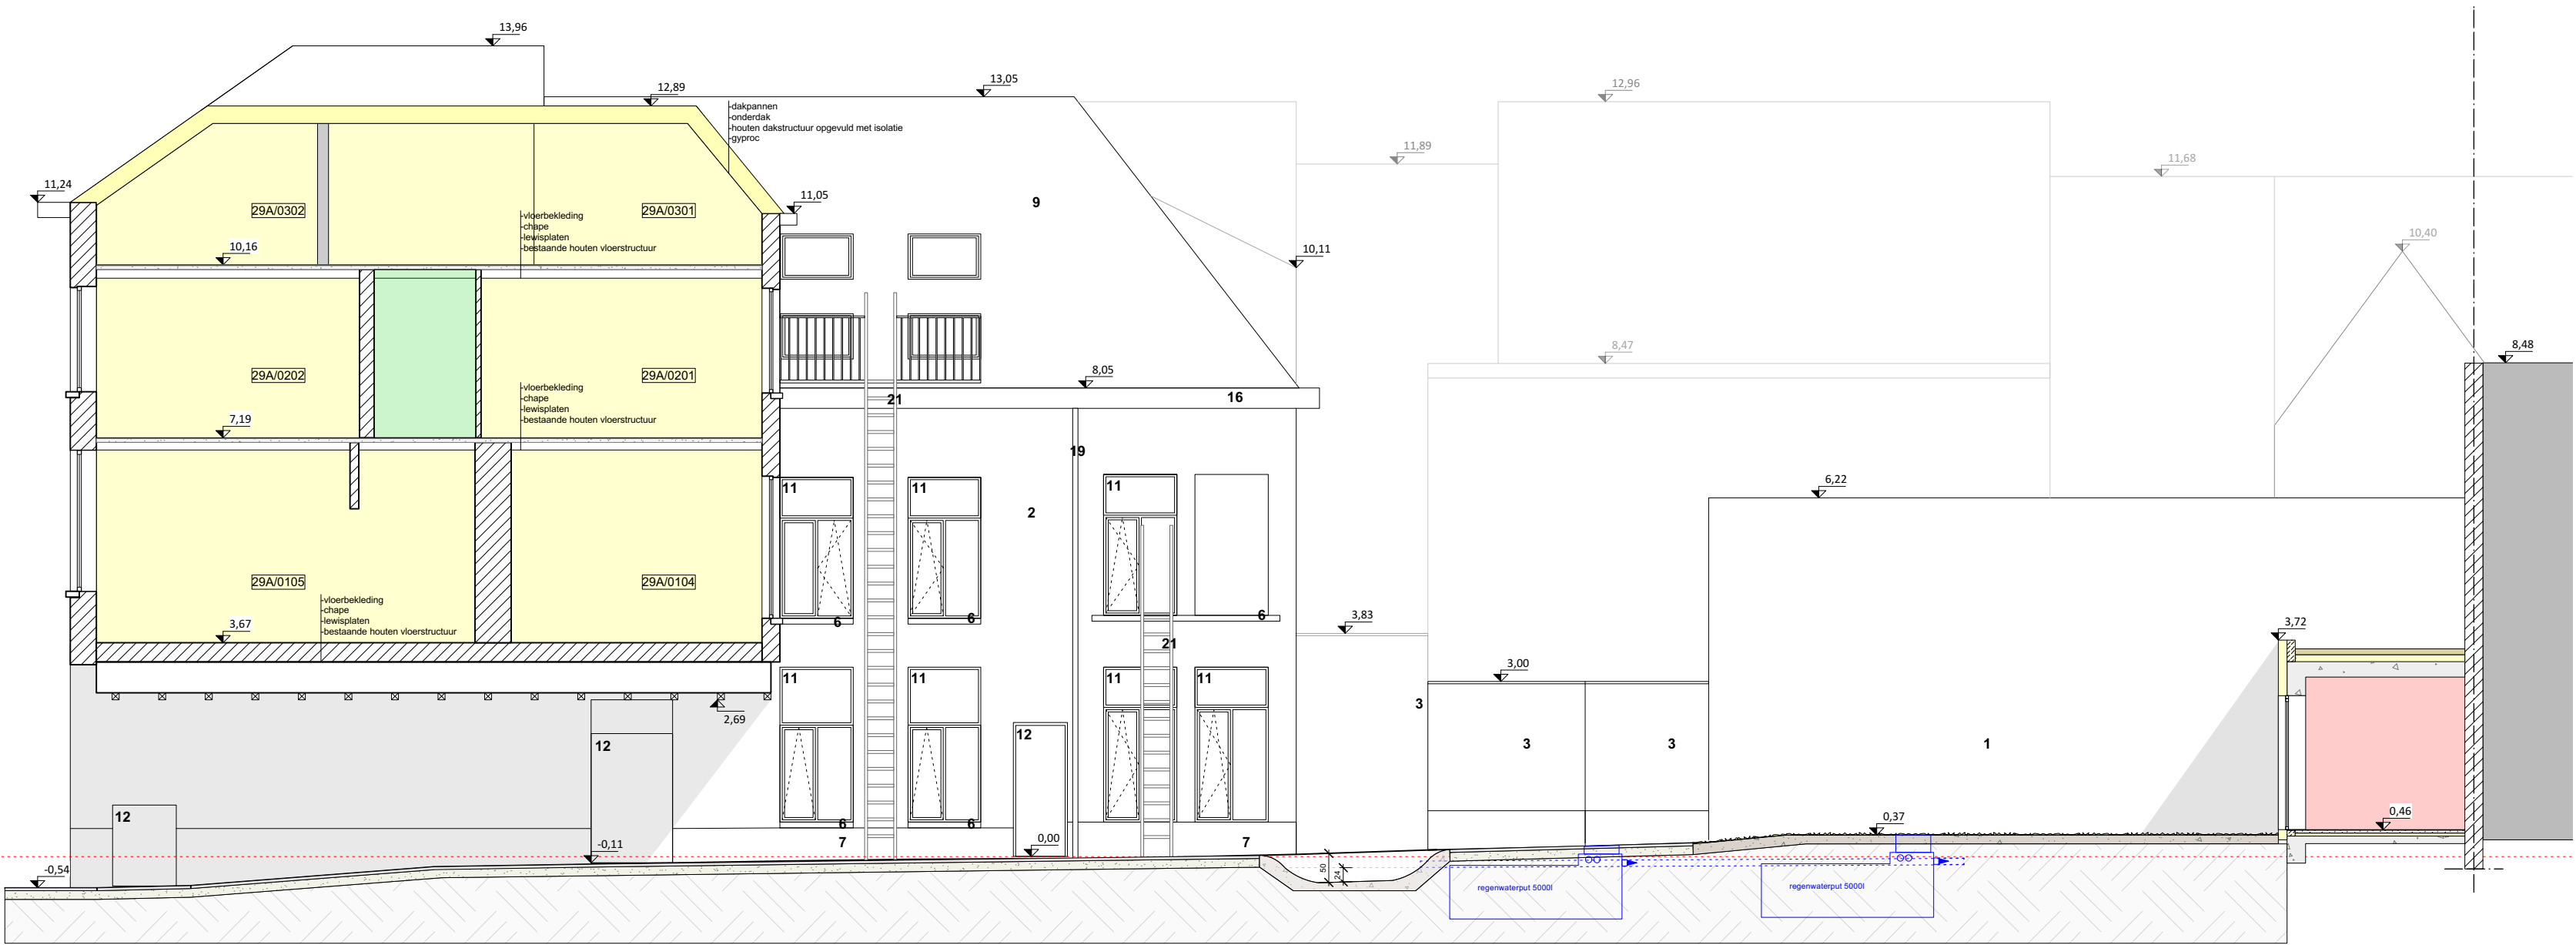

NAAMSESTRAAT 29

INPLANTINGSPLAN

bestaande toestand

01

10x


1:200

26/01/2024

VO_NAAMSE 29-31_I_B_01

1/1



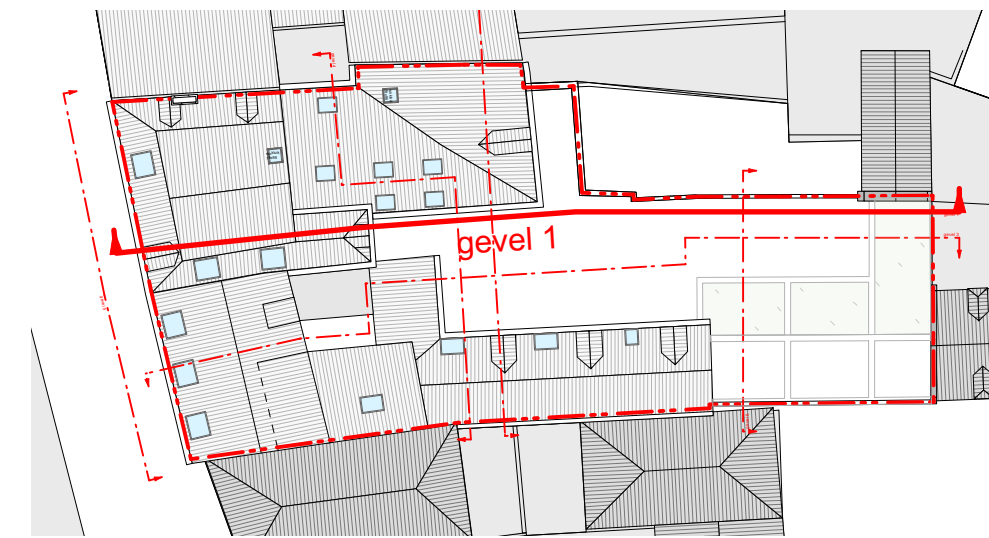

T'JONCK / NILIS
INGENIEUR-ARCHITECTEN

Erasmestraat 83/002
3001 Heverlee
T: +32 16 23 45 48


NAAMSESTRAAT 29
LANGSSNEDE - GEVEL 1
nieuwe toestand

015

1:100

26/01/2024

BA_NAAMSE 29-31_S_N_01

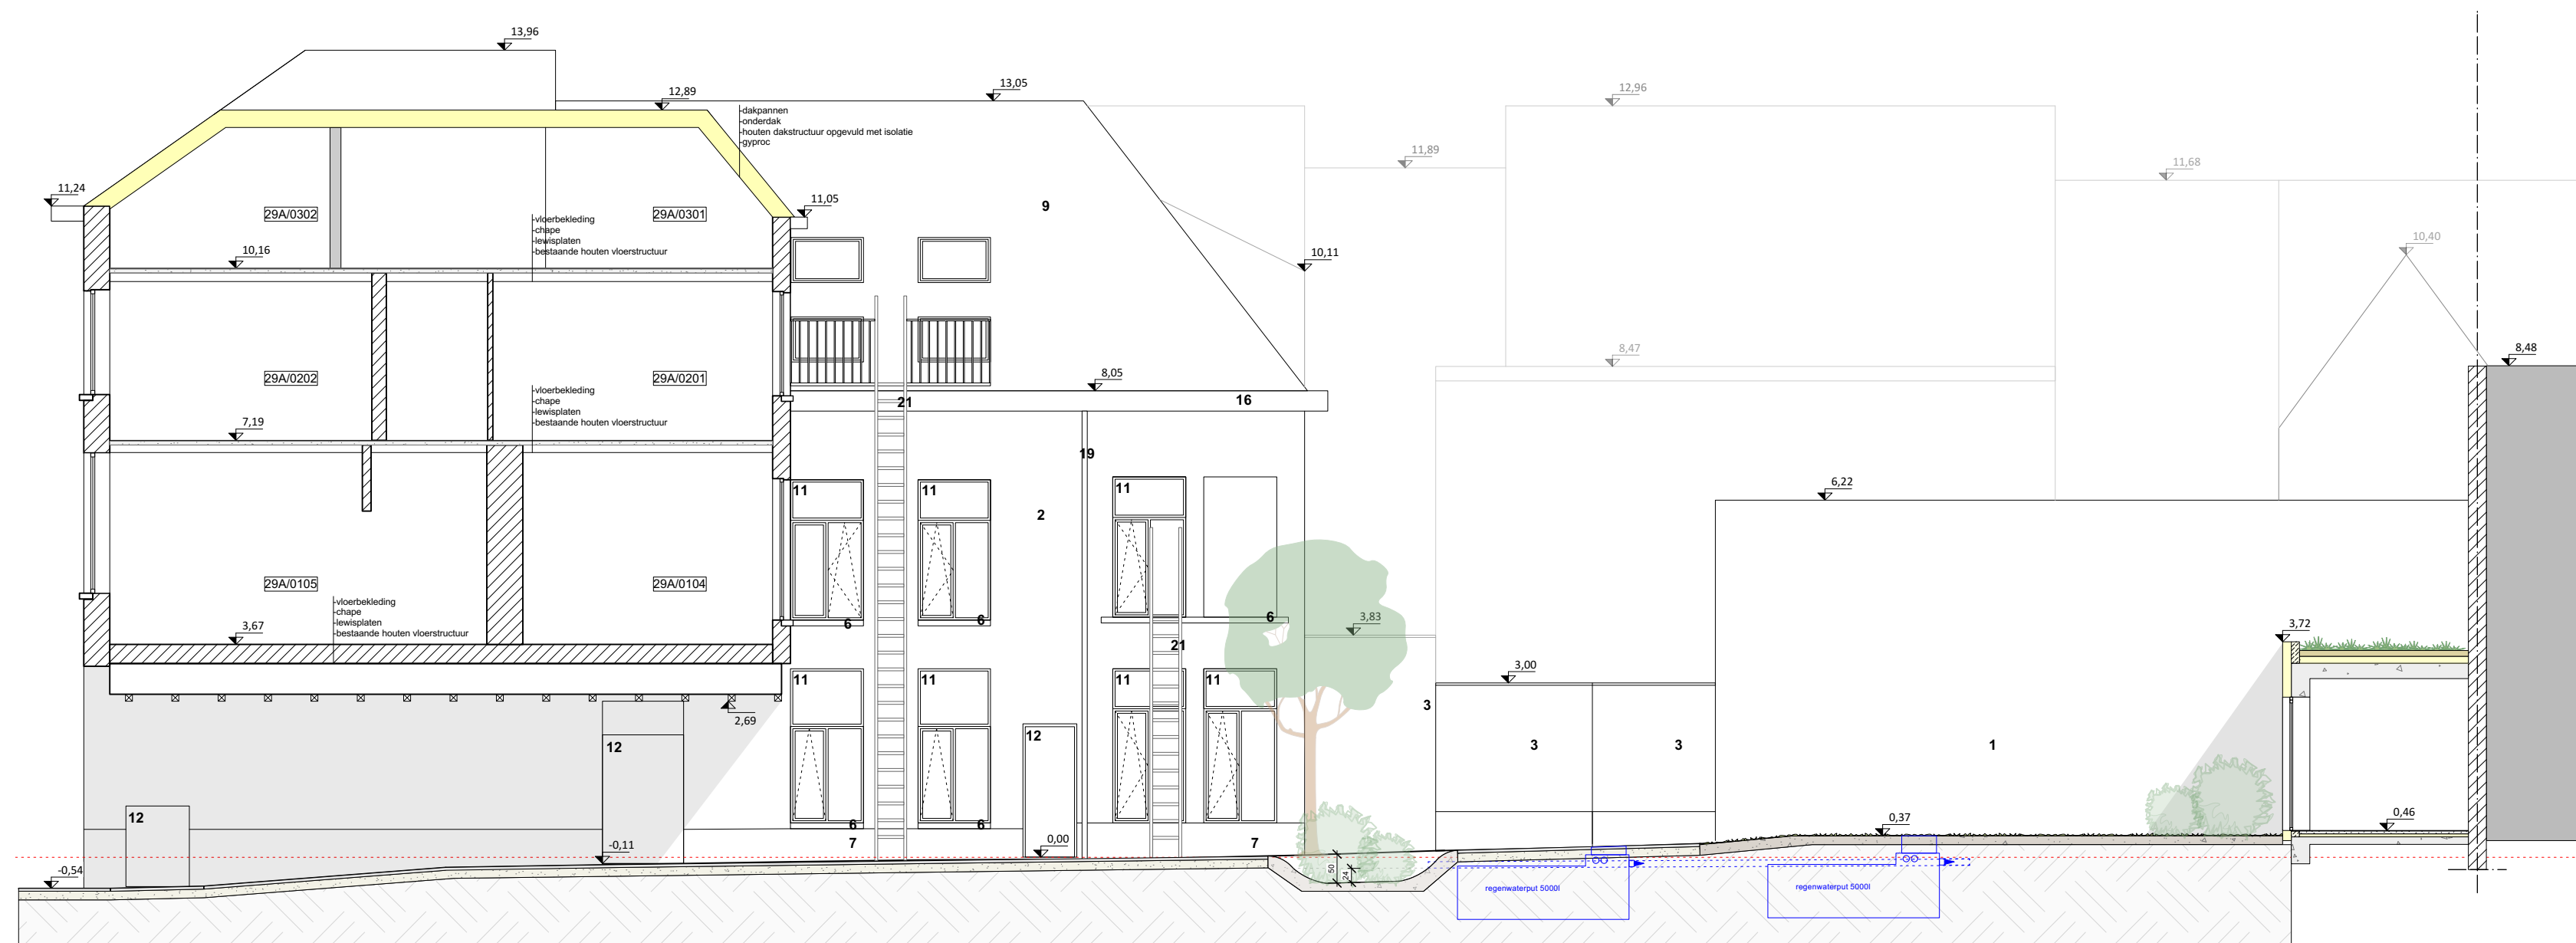



NAAMSESTRAAT 29
GRONDPLAN NIV 2
bestaande toestand

0 2 5
1:100

26/01/2024


BA_NAAMSE 29-31_P_8_04





Dit plan is een bijlage bij het advies van de dienst wonen dat werd uitgebracht in functie van de woonkwaliteit binnen deze aanvraag tot omgevingsvergunning.

Het betreft dus geen vergund plan.

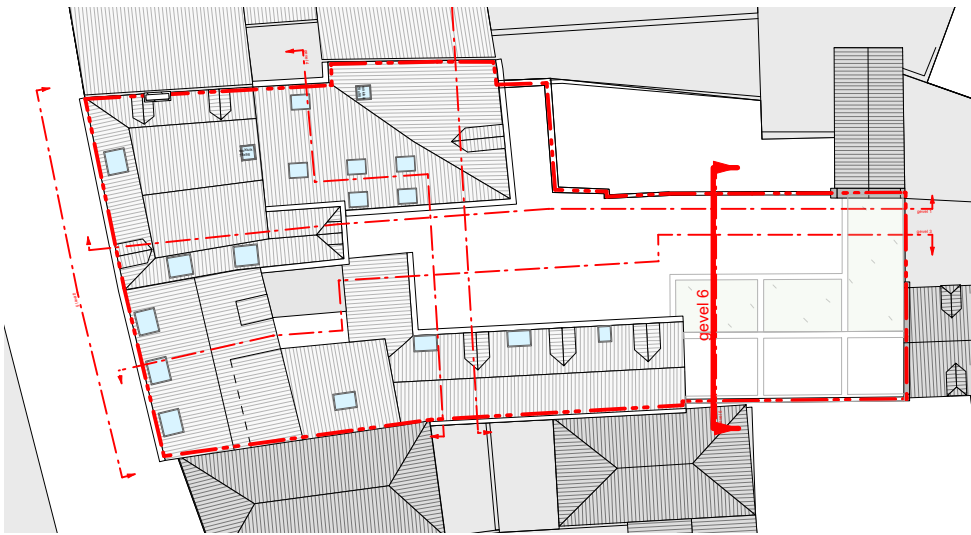

T'JONCK / NILIS

INGENIEUR-ARCHITECTEN

Erasme Ruelensvest 83/002

3001 Heverlee

T. +32 16 23 45 48

NAAMSESTRAAT 29

DWARSSNEDE - brandweer

nieuwe toestand

012.5


01


2.5

1:50

26/01/2024

BA_NAAMSE 29-31_G_8_05

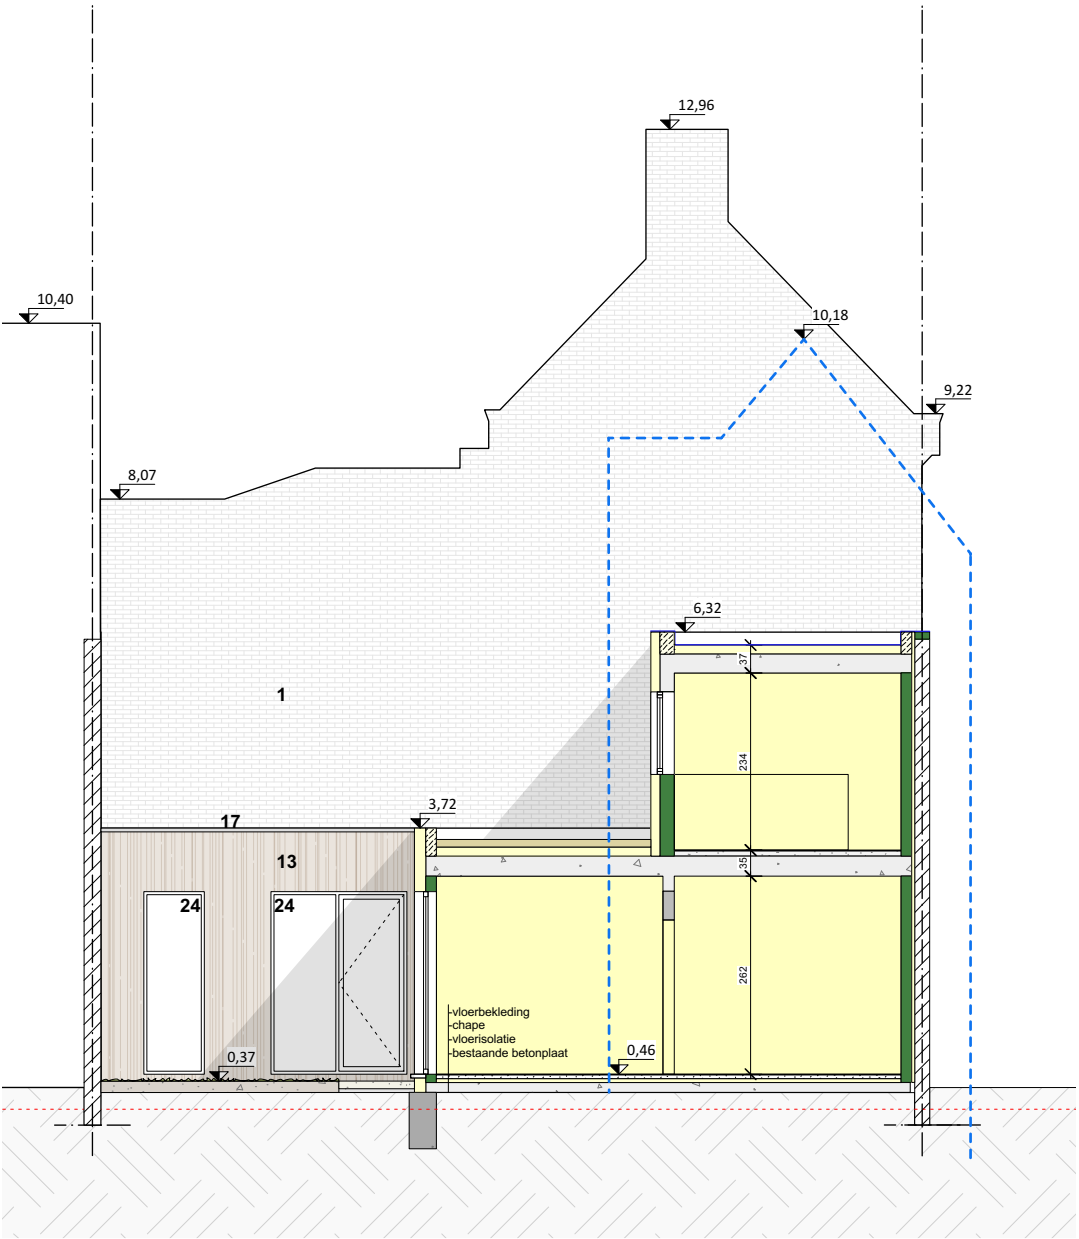

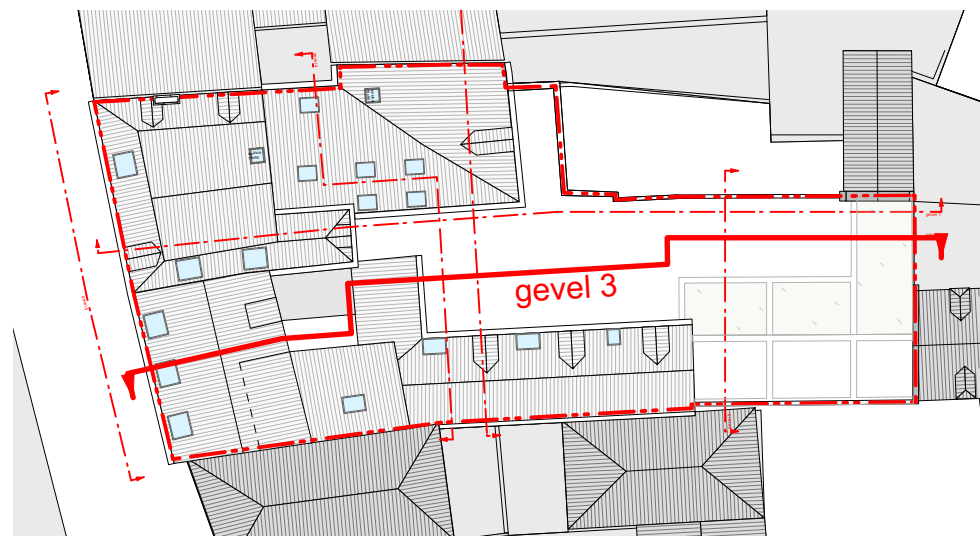

T'JONCK / NILIS

INGENIEUR-ARCHITECTEN

Erasm Ruelensvest 83/002

3001 Heverlee

T: +32 16 23 45 48

NAAMSESTRAAT 29

ZIJGEVEL - GEVEL 3

nieuwe toestand

012345

1:100

26/01/2024


BA_NAAMSE 29-31_G_N_02



NAAMSESTRAAT 29

LEGENDE

bestaande en nieuwe toestand

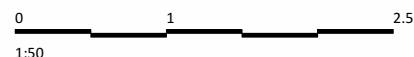

1:50

09/06/2022

BA_NAAMSE 29-31_L_01



GEVELMATERIALEN


- 1 gevelmetselwerk, rood
- 2 gevelmetselwerk, wit gekaleid
- 3 gevelmetselwerk, wit gepleisterd
- 4 gevelmetselwerk, beige gepleisterd
- 5 gevelmetselwerk, grijs gepleisterd
- 6 natuursteen, wit
- 7 plint, grijs
- 8 blauwe steen
- 9 dakpannen, grijs
- 10 buitenschrijnwerk hout, wit
- 11 buitenschrijnwerk pvc, wit
- 12 buitenschrijnwerk hout, grijs
- 13 gevelbekleding hout
- 14 vezelcementplaten, grijs
- 15 dakrand pvc, wit
- 16 dakrand pvc, grijs
- 17 dakrand alu, grijs
- 18 deksteen, beton
- 19 RWA pijp pvc
- 20 RWA pijp zink
- 21 vluchtladder
- 22 borstwering, grijs
- 23 beton
- 24 ramen pvc, grijs

AANDUIDINGEN PLANNEN EN SNEDES

- afbraak
- bestaand metselwerk
- snelbouwmetselwerk
- gevelmetselwerk
- (voorzet)wand gipskarton met minerale wol
- isolatie PIR of PUR
- isolatie minerale wol (MW)
- chape
- bestaand beton

BRANDWEER

- brandcentrale
- compartimenteringwand - REI 60 of REI 30
- REI 30 brandweerstandsklasse, minuten
- nooduitgang
- brandblusser
- brandmelder
- brandhaspel
- optische rookmelder

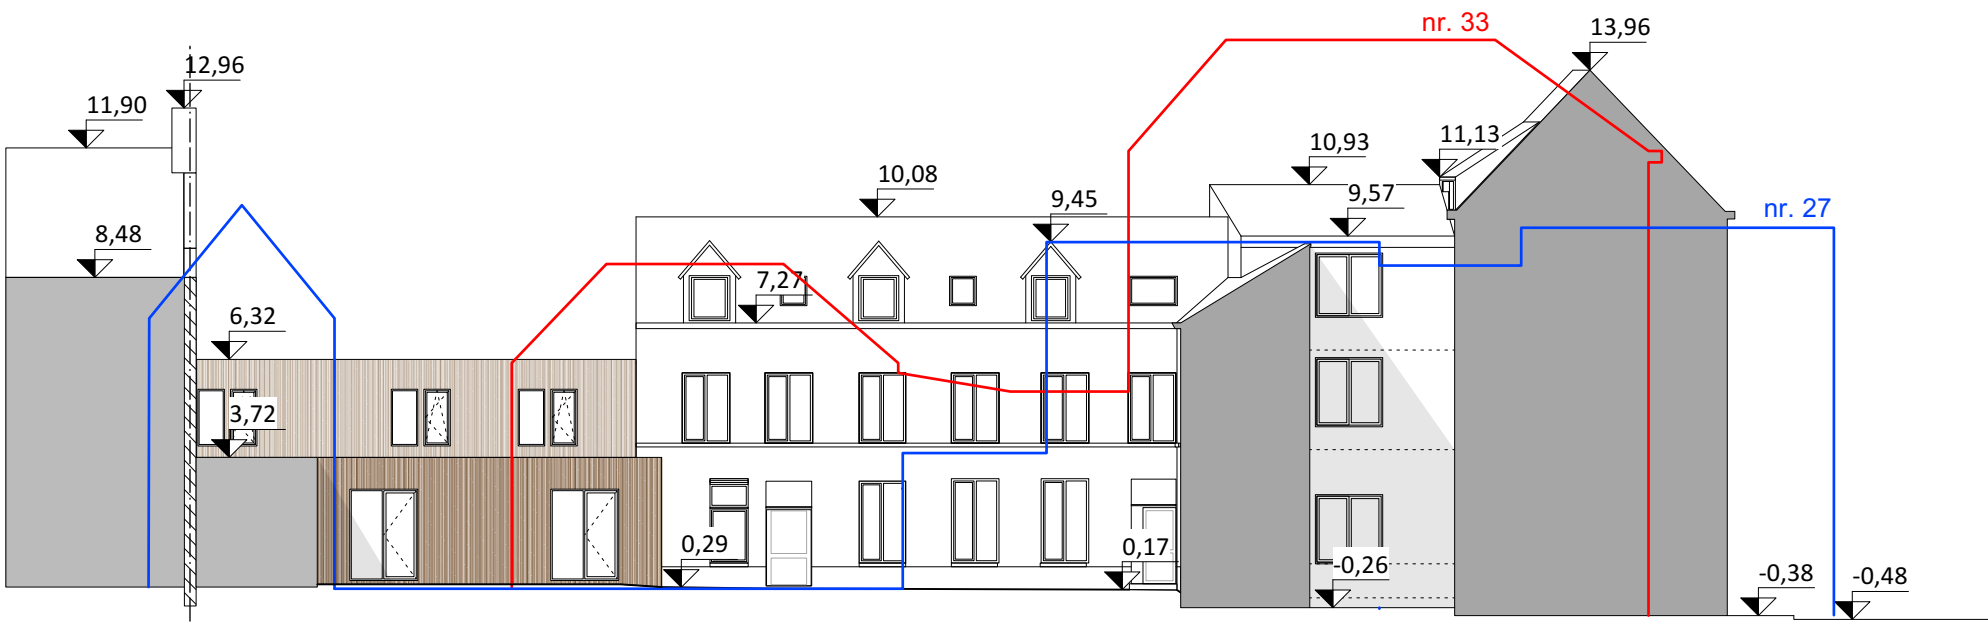

NAAMSESTRAAT 29

GRONDPLAN GELIJKVLOERS

nieuwe toestand

01

1

5

1:100

26/01/2024

BA_NAAMSE 29-31_P_N_02



Dit plan is een bijlage bij het advies van de dienst wonen dat werd uitgebracht in functie van de woonkwaliteit binnen deze aanvraag tot omgevingsvergunning.

Het betreft dus geen vergund plan.

Handtekening(en)